IHOR SAYEVICH

interior designer

ОСНОВНЕ ТЕХНІЧНЕ КРЕСЛЕННЯ

м. Львів, вул. Трускавецька ЖК Парус Smart

2026


Відомість робочих креслень

№	Найменування	Примітка
	Титульний лист	
01	Відомість робочих креслень	
02	Відомість робочих креслень	
03	Обмірний план. Поверх 1	
04	Обмірний план. Поверх 2	
05	План демонтажу. Поверх 2	
06	План демонтажу. 3D схеми	
07	План демонтажу. Поверх 2	
08	План монтажу. Поверх 1	
09	План монтажу. 3D схеми	
10	План монтажу. 3D схеми	
11	План монтажу. Поверх 2	
12	План монтажу. 3D схеми	
13	План розташування гіпсокартонних конструкцій. Поверх 1	
14	План розташування гіпсокартонних конструкцій. Поверх 1	
15	Презентаційний план. Поверх 2	
16	Презентаційний план. Поверх 1	
17	План кондиціонування та вентиляції. Поверх 1	
18	План кондиціонування та вентиляції. Поверх 2	
19	План розташування підігріву підлоги і опалювальних приладів	
20	План розташування підігріву підлоги та опалювальних приладів. Поверх 2	
21	План-схема розташування сантехнічного обладнання. Поверх 1	
22	План-схема розташування сантехнічного обладнання. Поверх 1	
23	План-схема розташування сантехнічного обладнання. Поверх 2	
24	План розташування електрофурнітури. Поверх 1	
25	План розташування електрофурнітури. Поверх 2	
26	Специфікація електрофурнітури	
27	Специфікація електрофурнітури	
28	Специфікація електрофурнітури	

Відомість робочих креслень

№	Найменування	Примітка
29	План розташування освітлювальних приладів. Поверх 1	
30	План розташування освітлювальних приладів. Поверх 2	
31	План управління освітленням. Поверх 1	
32	План управління освітленням. Поверх 2	
33	План оздоблення стель. Поверх 1	
34	План оздоблення стель. Поверх 1	
35	Перерізи стель	
36	План оздоблення підлоги. Поверх 1	
37	План оздоблення підлоги. Поверх 1	
38	План відкривання дверей та влаштування плінтусів. Поверх 1	
39	План відкривання дверей та влаштування плінтусів. Поверх 1	
40	Відомість дверних полотен	
41	План розташування розгорток. Поверх 1	
42	План розташування розгорток. Поверх 2	
43	Розгортки приміщення 1 (передпокій)	
44	Розгортки приміщення 2 (ванна кімната)	
45	Розгортки приміщення 2 (ванна кімната)	
46	Розгортки приміщення 3 (кухня-вітальня)	
47	Розгортки приміщення 3 (кухня-вітальня)	
48	Розгортки приміщення 4 (сходова частина)	
49	Розгортки приміщення 4 (сходова частина)	
50	Розгортки приміщення 6 (коридор, 2 поверх)	
51	Розгортки приміщення 7 (ванна кімната, 2 поверх)	
52	Розгортки приміщення 7 (ванна кімната, 2 поверх)	
53	Розгортки приміщення 9 (спальня)	
54	Розгортки приміщення 10 (кабінет)	

Обмірний план. Поверх 1
М1:35

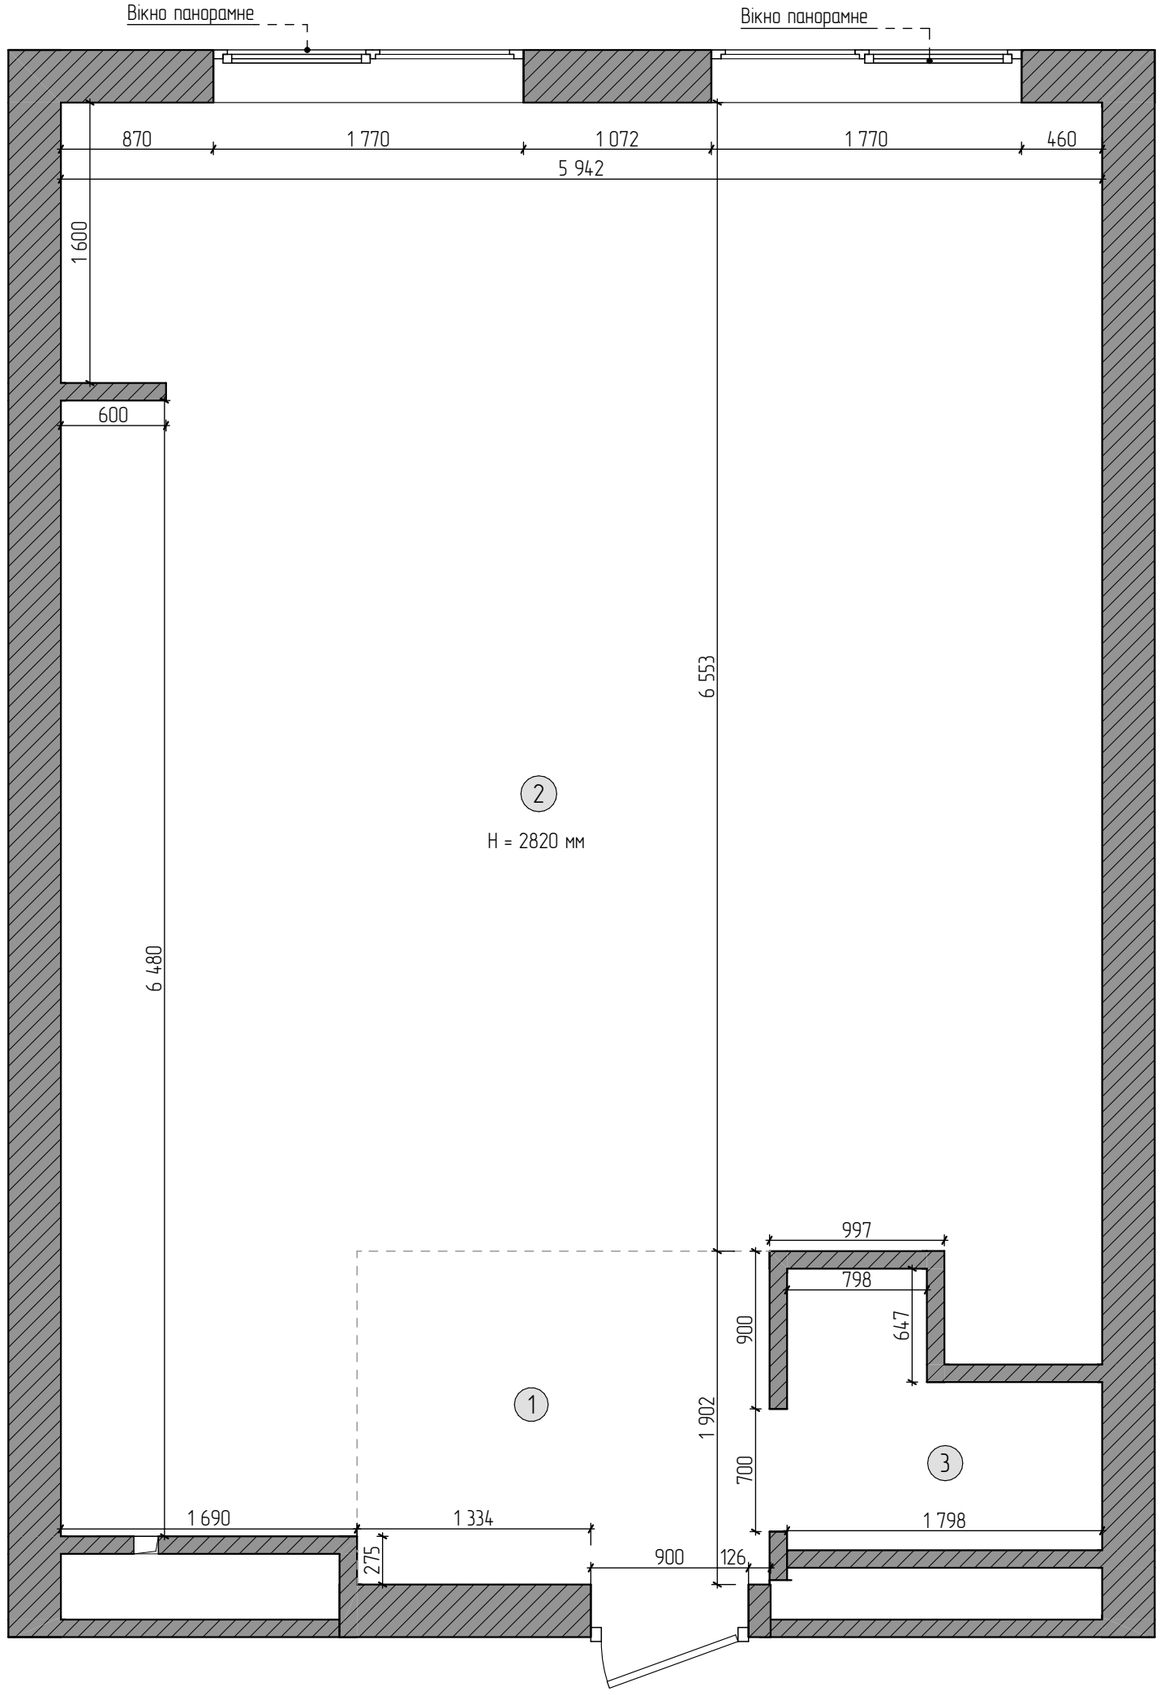

Експлікація приміщення

№	Найменування	Площа м.кв.	Примітка
1	Вхідна зона	4,49	
2	Кухня-студія	42,20	
3	Санвузол	2,23	
5	Коридор	10,36	
6	Ванна кімната	8,20	
7	Гардероб	4,96	
8	Кабінет	16,76	
9	Спальня	14,98	
		104,18 m^2	

Умовні позначення:


– існуючі стіни

Примітки:

Розміри вказані для прорахунку основних будівельних та оздоблювальних матеріалів.
Перед початком роботи і закупівлею матеріалів розміри перевірити на об'єкті!

iSD IHOR SAYEVICH interior designer	м. Львів, вул. Трускавецька ЖК Парус Smart	Розділ	Аркуш	Аркушів
	Обмірний план. Поверх 1	РП-ТК	03	55
	Ihor Sayevich Designer	@ihor_sayevich_designer	+380 97 585 91 01	

Обмірний план. Поверх 2

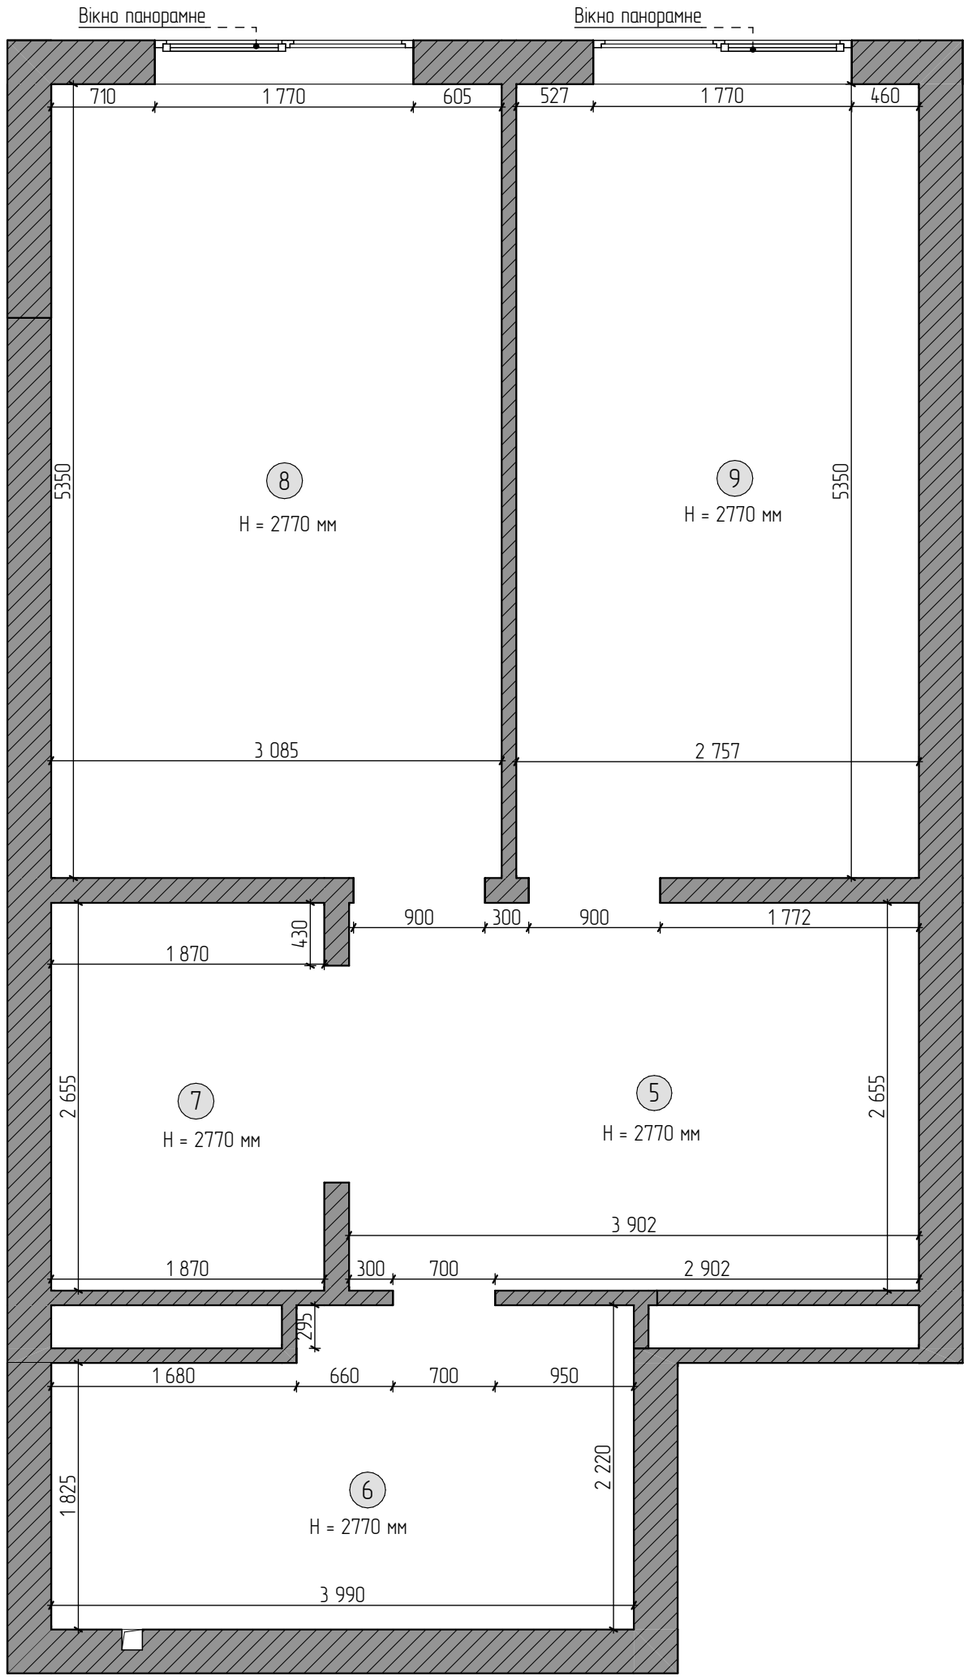

Експлікація приміщення

№	Найменування	Площа м.кв.	Примітка
1	Вхідна зона	4,49	
2	Кухня–студія	42,20	
3	Санвузол	2,23	
5	Коридор	10,36	
6	Ванна кімната	8,20	
7	Гардероб	4,96	
8	Кабінет	16,76	
9	Спальня	14,98	
		104,18 m^2	

Умовні позначення:

– існуючі стіни


Примітки:

Розміри вказані для прорахунку основних будівельних та оздоблювальних матеріалів.
Перед початком роботи і закупівлею матеріалів розміри перевірити на об'єкті!

IHOR SAYEVICH interior designer	м. Львів, вул. Трускавецька ЖК Парус Smart	Розділ	Аркуш	Аркушів
	Обмірний план. Поверх 2	РП–ТК	04	55
	Ihor Sayevich Designer	@ihor_sayevich_designer	+380 97 585 91 01	

План демонтажу. Поверх 1

М1:35

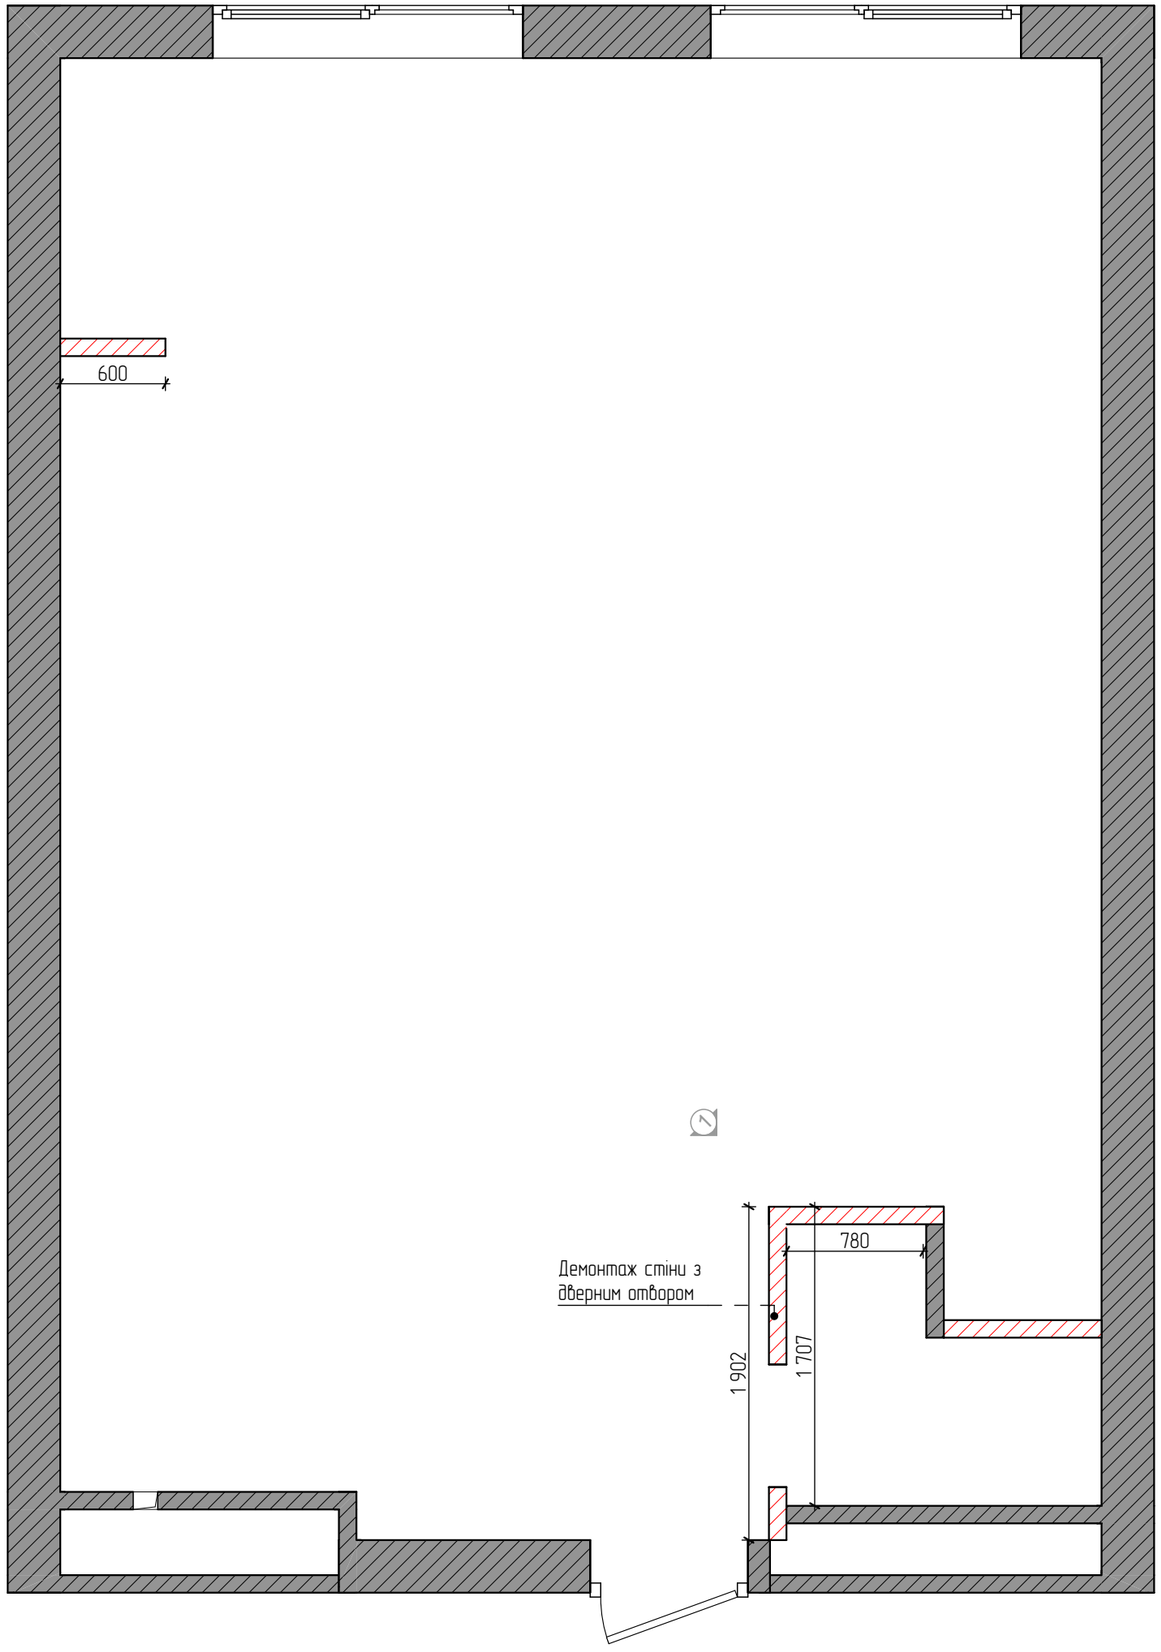

Умовні позначення:

– існуючі стіни

– елементи, що демонтуються

Примітки:


Розміри вказані для прорахунку основних будівельних та оздоблювальних матеріалів.
Перед початком роботи і закупівлею матеріалів розміри перевірити на об'єкті!

м. Львів, вул. Трускавецька ЖК Парус Smart	Розділ	Аркуш	Аркушів
План демонтажу. Поверх 2	РП-ТК	05	55


IHOR SAYEVICH interior designer

Ihor Sayevich Designer @ihor_sayevich_designer +380 97 585 91 01

3D схема демонтажу. Поверх 1

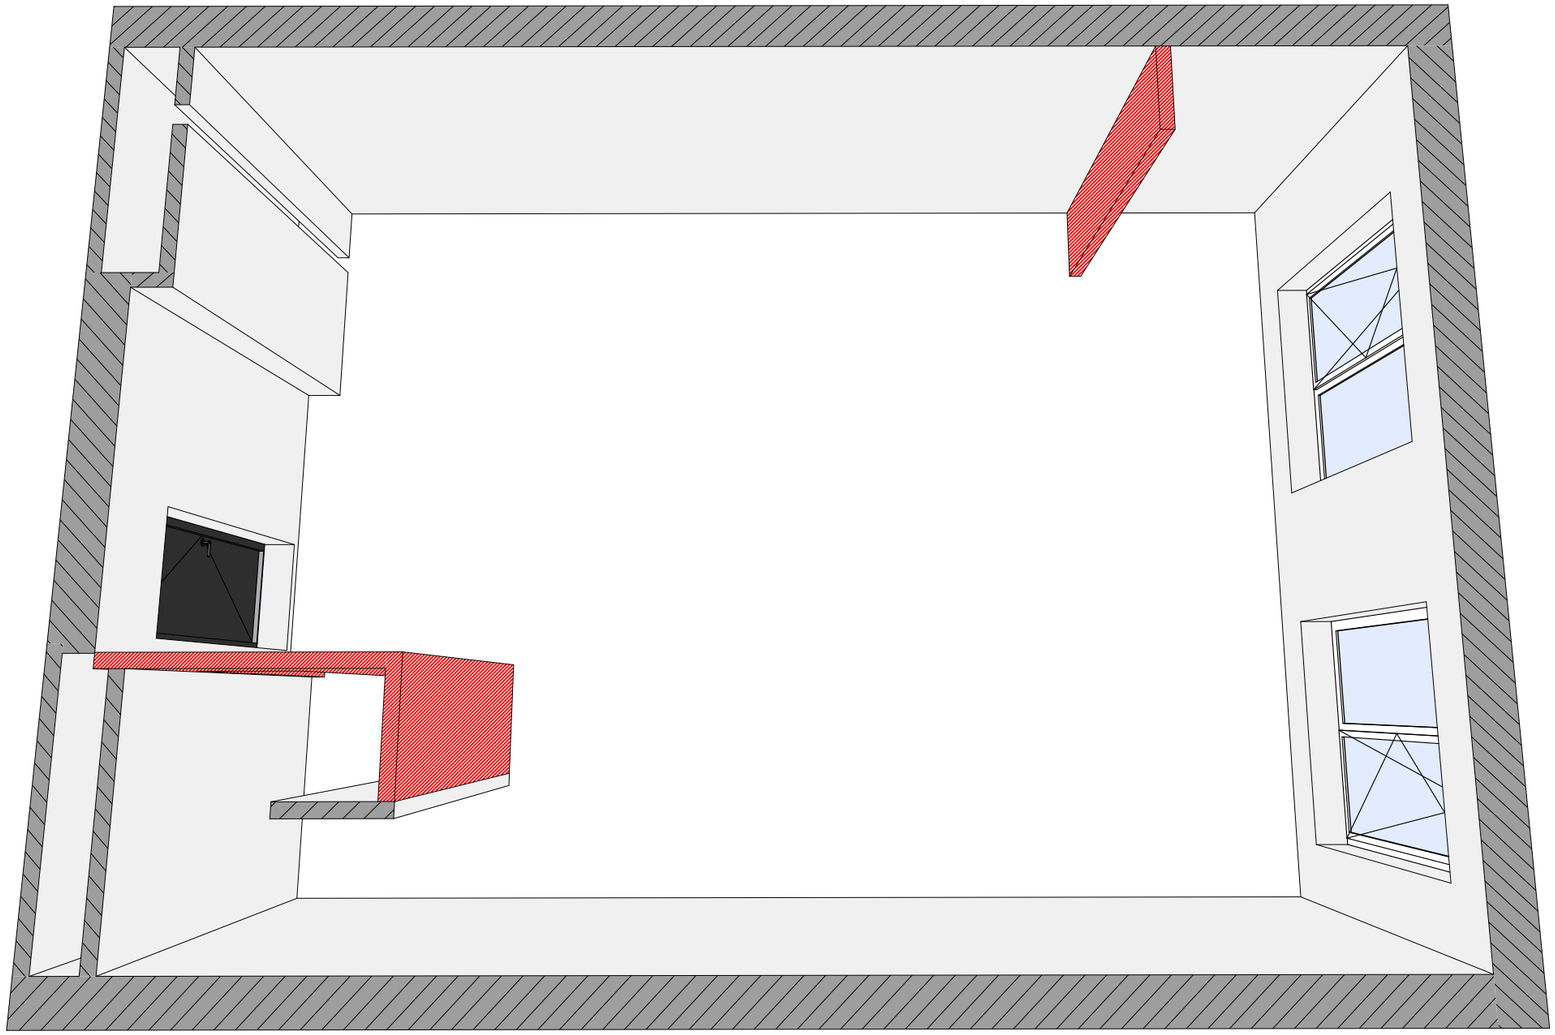


Демонтаж. Вигляд 1

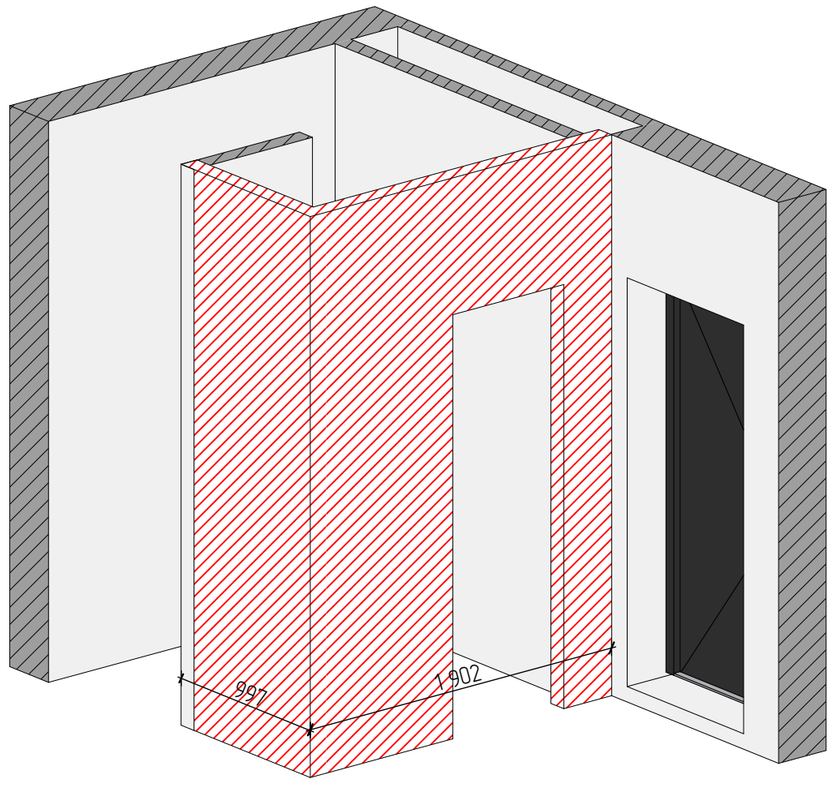

iSD IHOR SAYEVICH interior designer	м. Львів, вул. Трускавецька ЖК Парус Smart	Розділ	Аркуш	Аркушів
	План демонтажу. 3D схеми	РП-ТК	06	55
	Ihor Sayevich Designer	@ihor_sayevich_designer	+380 97 585 91 01	

План демонтажу. Поверх 2

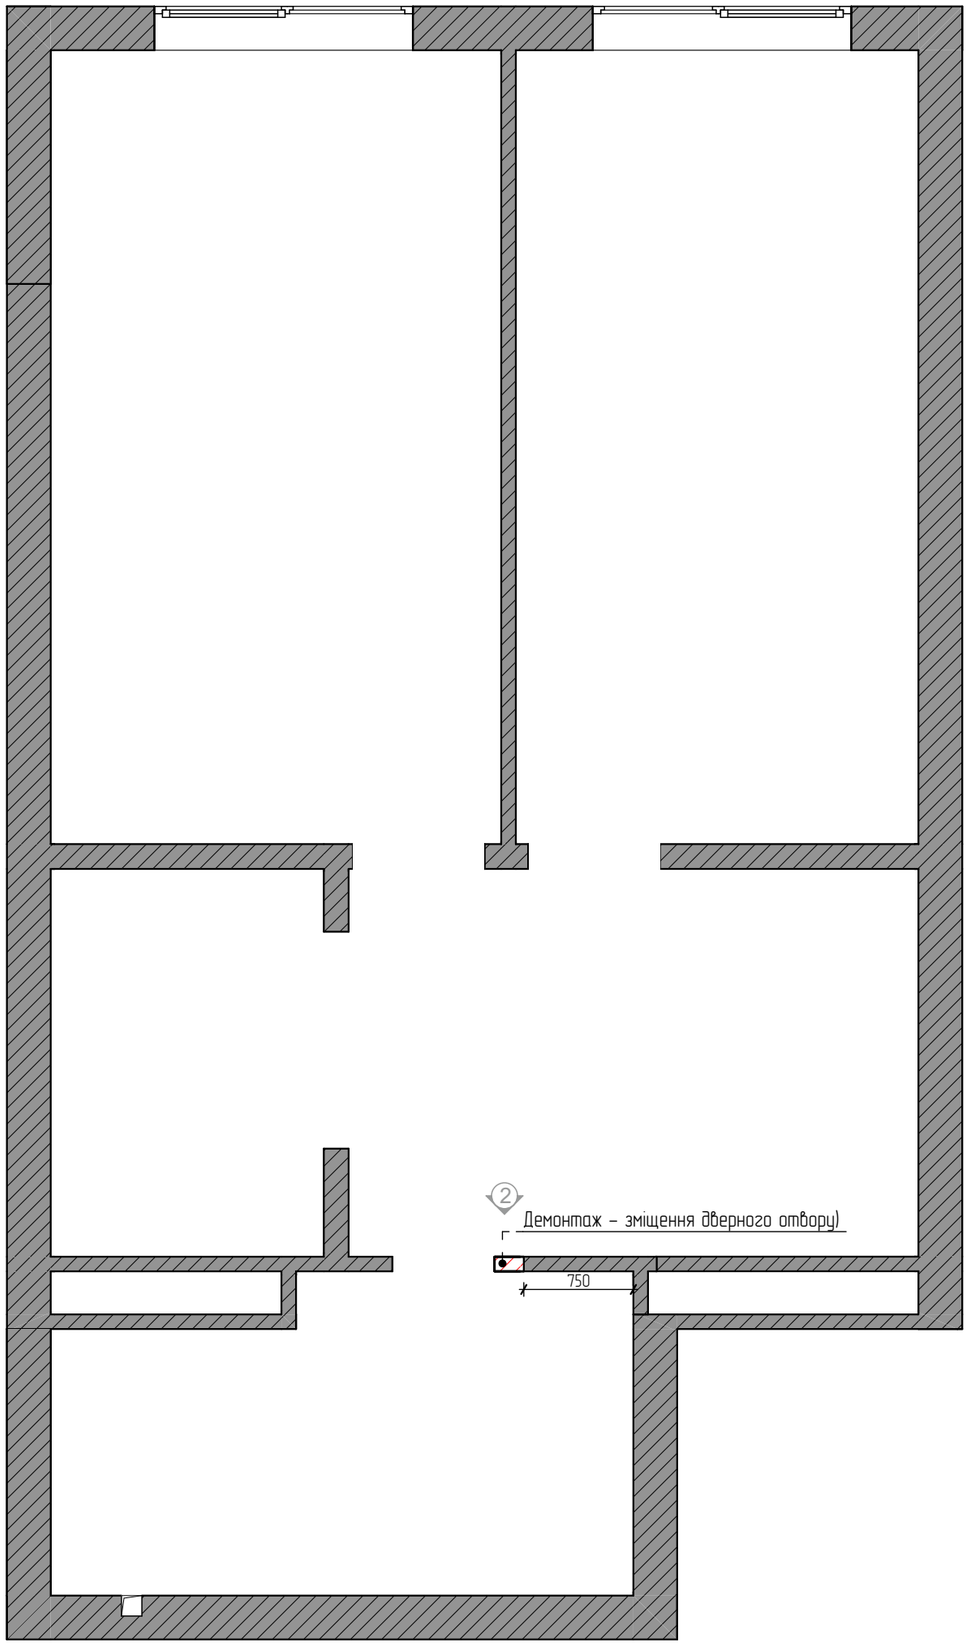


Умовні позначення:

– існуючі стіни

– елементи, що демонтуються

Демонтаж. Вигляд 2

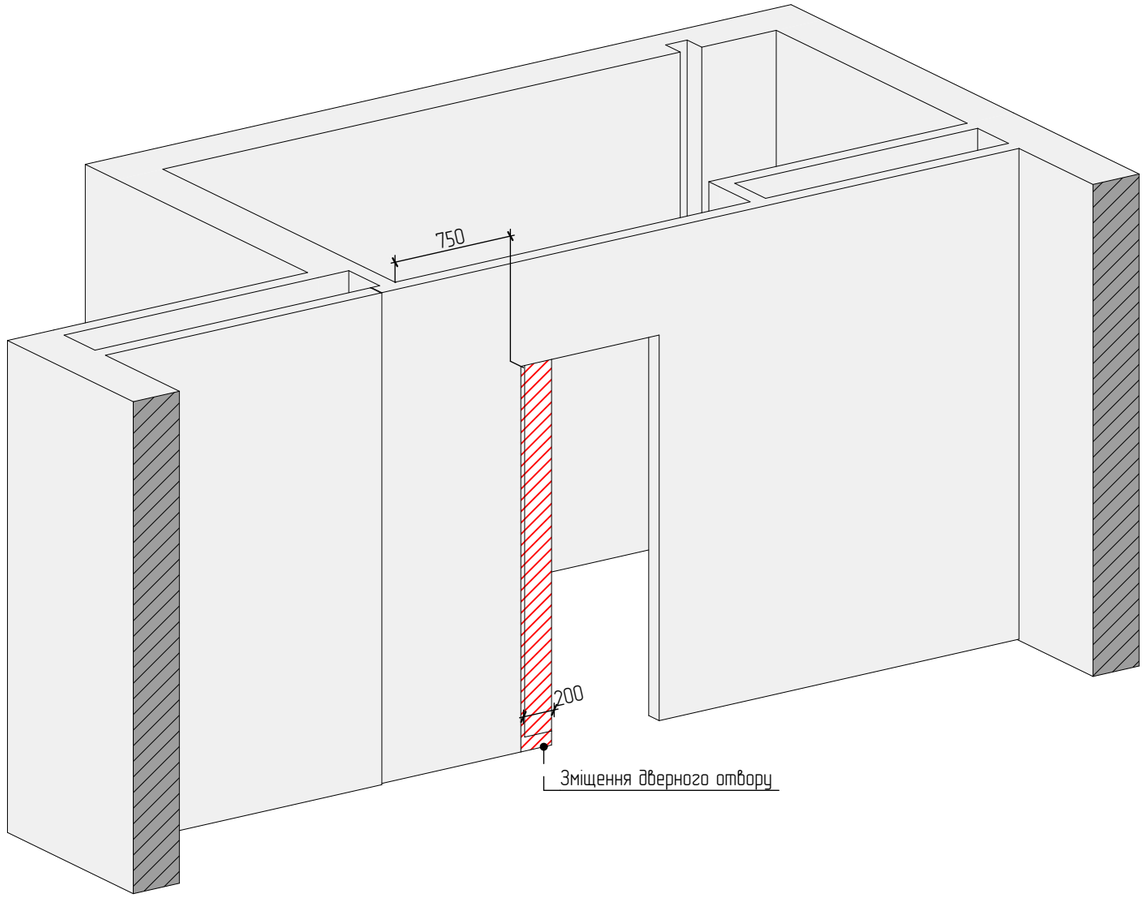


Примітки:

Розміри вказані для прорахунку основних будівельних та оздоблювальних матеріалів.
Перед початком роботи і закупівлею матеріалів розміри перевірити на об'єкті!

IHOR SAYEVICH interior designer	м. Львів, вул. Трускавецька ЖК Парус Smart	Розділ	Аркуш	Аркушів
	План демонтажу. Поверх 2	РП-ТК	07	55

Ihor Sayevich Designer @ihor_sayevich_designer +380 97 585 91 01

План монтажу
М1:35

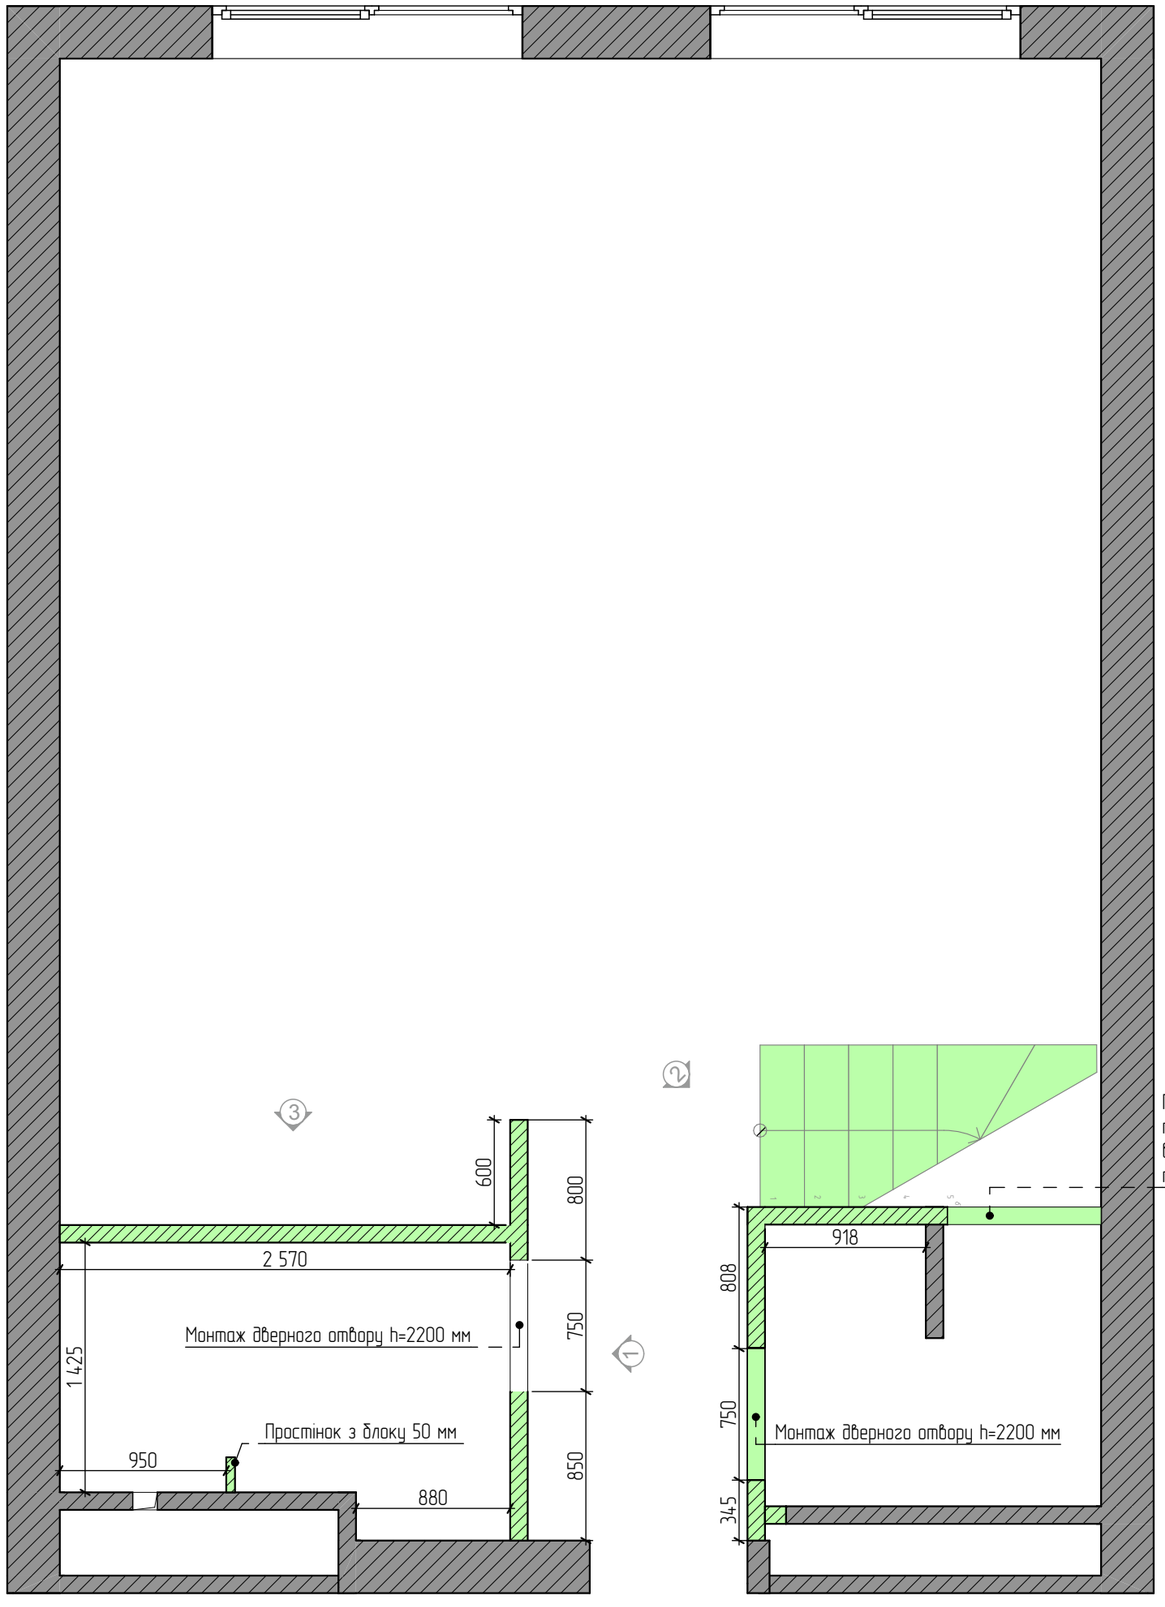

Умовні позначення:

– існуючі стіни

– нові елементи


Примітки:

Розміри вказані для прорахунку основних будівельних та оздоблювальних матеріалів.
Перед початком роботи і закупівлею матеріалів розміри перевірити на об'єкті!

Товщина нових перегородок 100 мм, якщо не вказано інше!


iSD IHOR SAYEVICH interior designer	м. Львів, вул. Трускавецька ЖК Парус Smart	Розділ	Аркуш	Аркушів
	План монтажу. Поверх 1	РП-ТК	08	55
	Ihor Sayevich Designer	@ihor_sayevich_designer	+380 97 585 91 01	

3D схема монтажу. Поверх 1

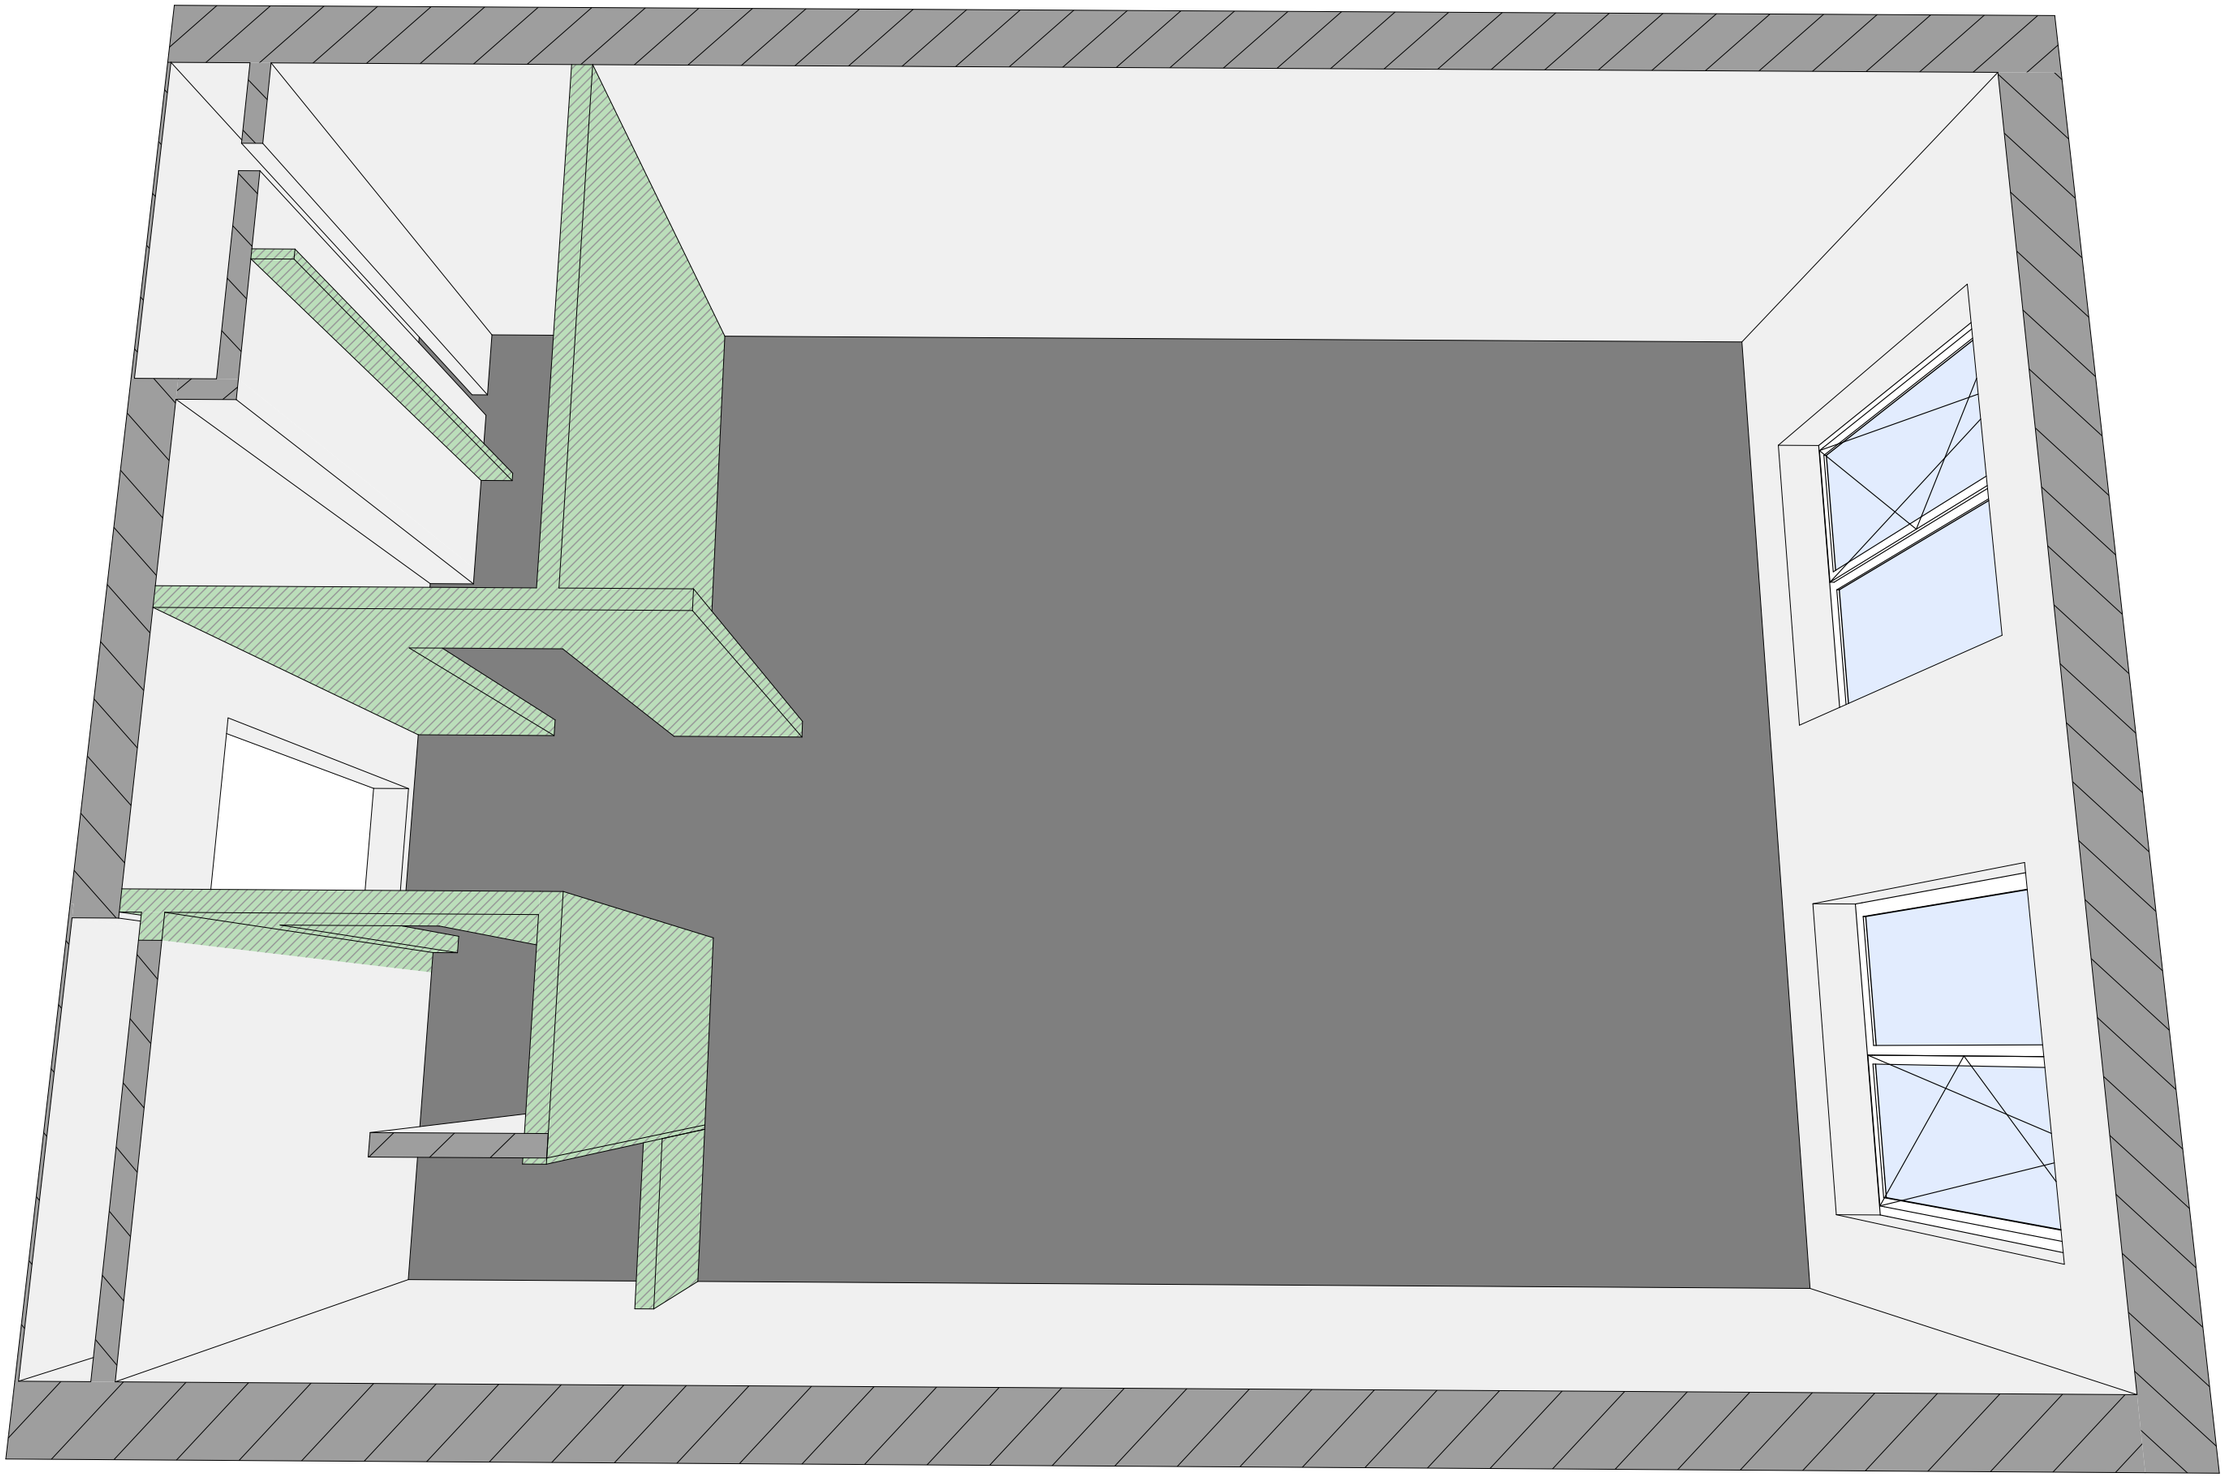


iSD IHOR SAYEVICH interior designer	м. Львів, вул. Трускавецька ЖК Парус Smart	Розділ	Аркуш	Аркушів
	План монтажу. 3D схеми	РП-ТК	09	55
	Ihor Sayevich Designer	@ihor_sayevich_designer	+380 97 585 91 01	


Монтаж. Вигляд 1

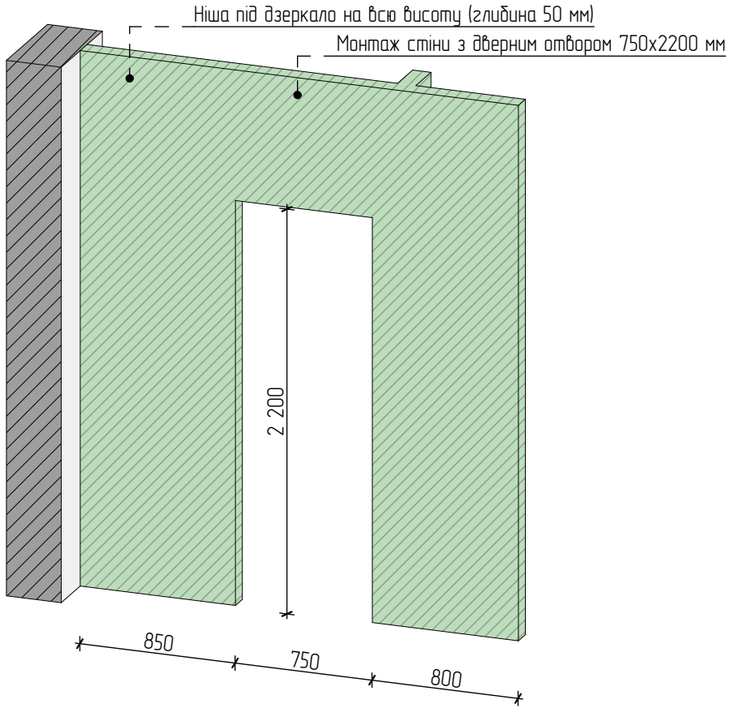

Монтаж. Вигляд 2

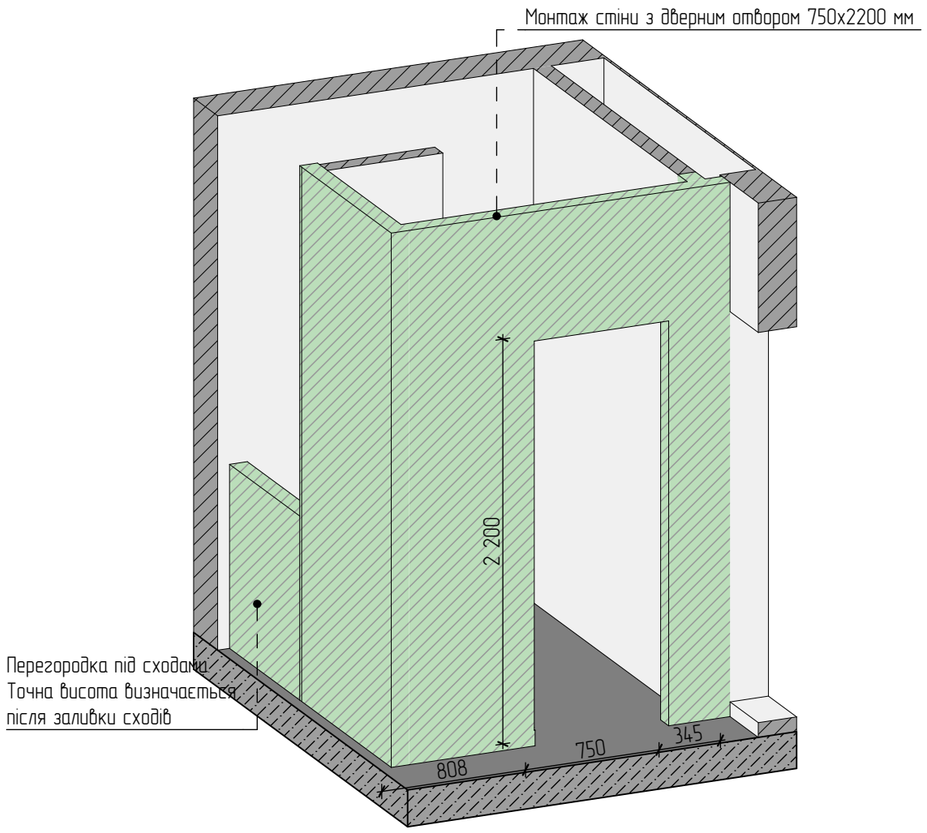


Монтаж. Вигляд 3

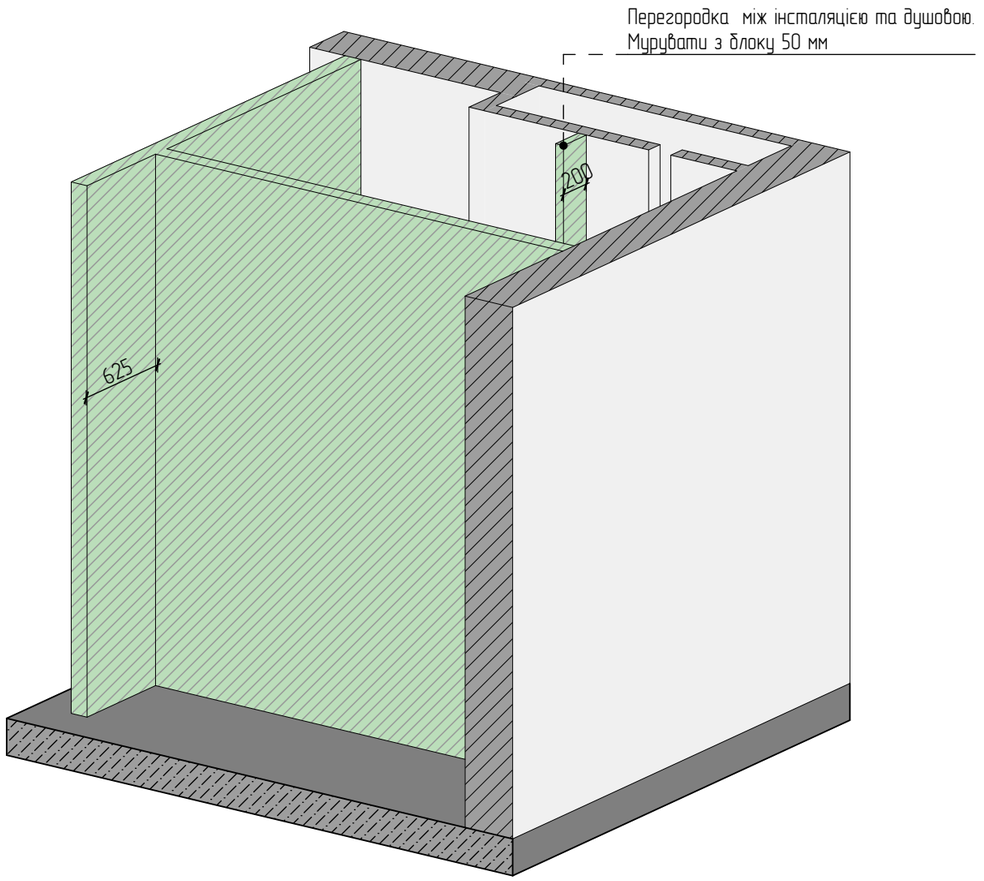

м. Львів, вул. Трускавецька ЖК Парус Smart	Розділ	Аркуш	Аркушів
План монтажу. 3D схеми	РП-ТК	10	55

IHOR SAYEVICH interior designer
Ihor Sayevich Designer @ihor_sayevich_designer +380 97 585 91 01

План монтажу. Поверх 2

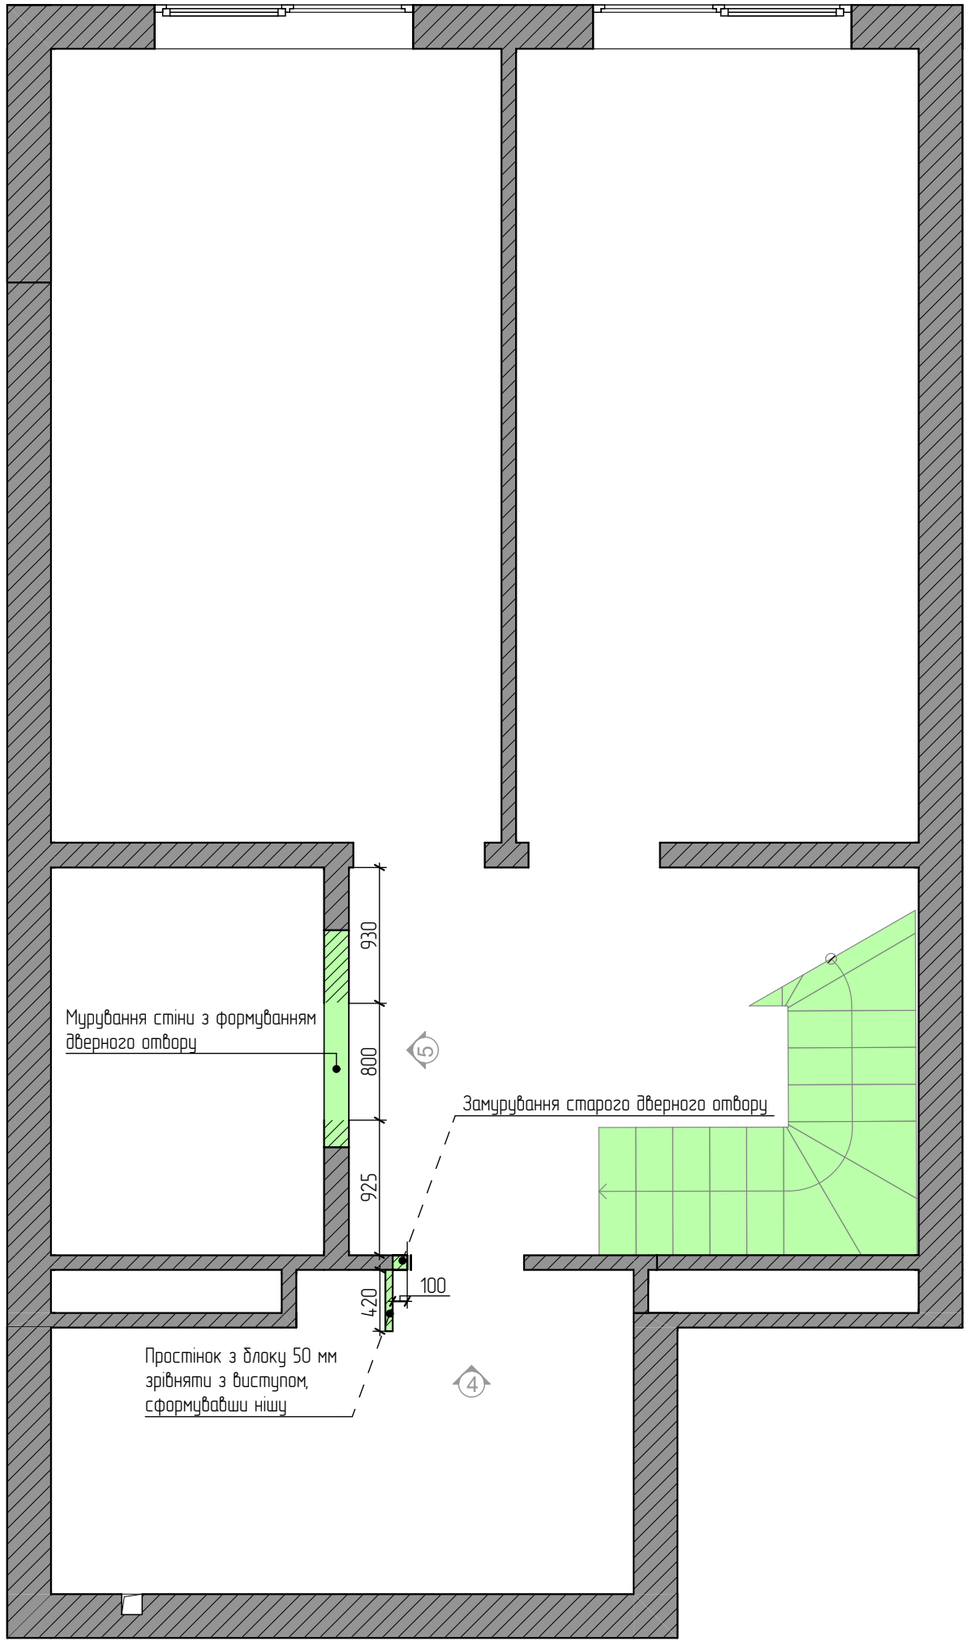

Умовні позначення:

– існуючі стіни

– нові елементи


Примітки:

Розміри вказані для прорахунку основних будівельних та оздоблювальних матеріалів.
Перед початком роботи і закупівлею матеріалів розміри перевірити на об'єкті!


Товщина нових перегородок 100 мм, якщо не вказано інше!

IHOR SAYEVICH interior designer	м. Львів, вул. Трускавецька ЖК Парус Smart	Розділ	Аркуш	Аркушів
	План монтажу. Поверх 2	РП–ТК	11	55
	Ihor Sayevich Designer	@ihor_sayevich_designer	+380 97 585 91 01	

3D схема монтажу. Поверх 2

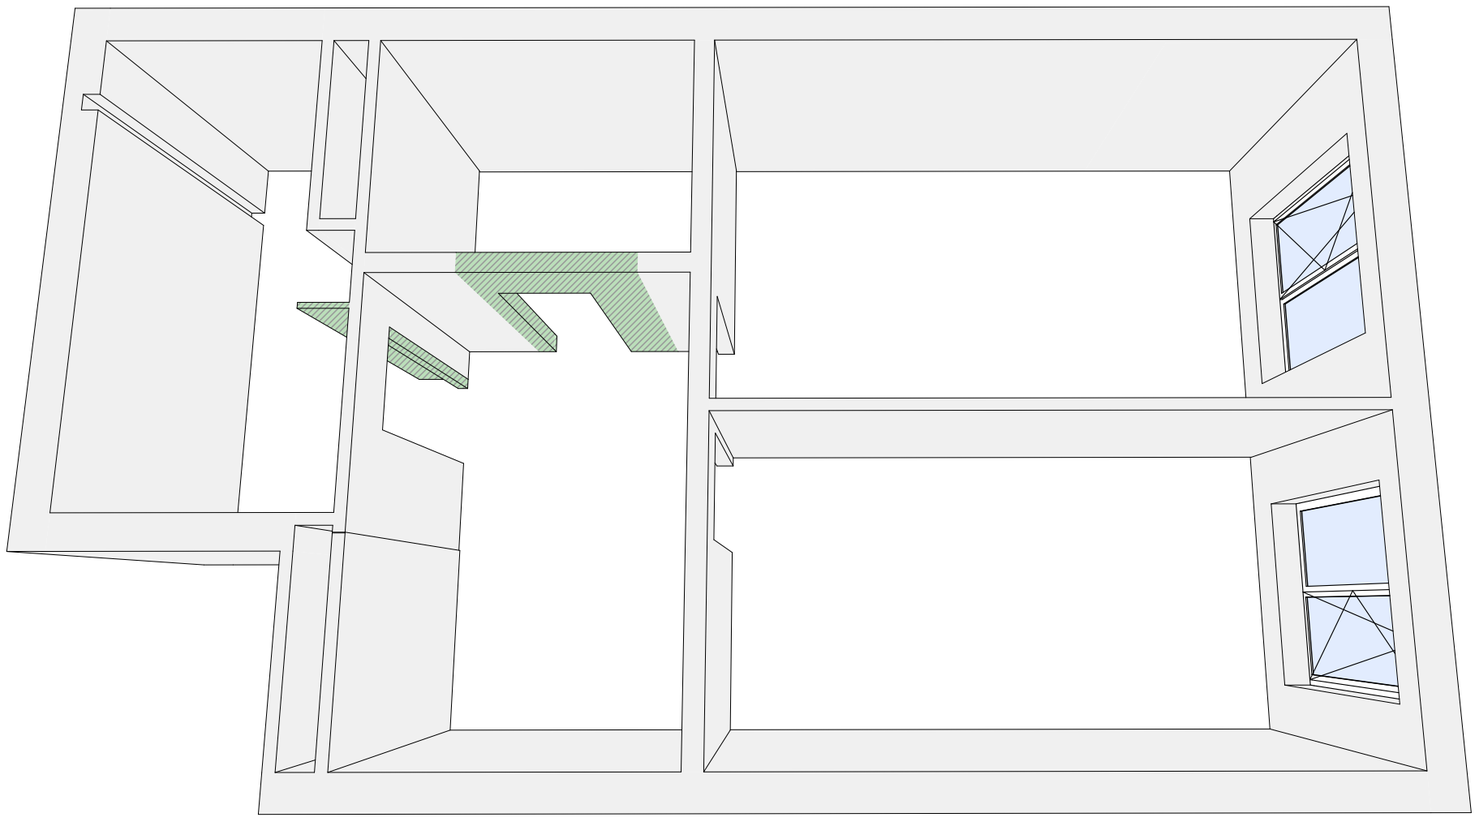


Монтаж. Вигляд 4

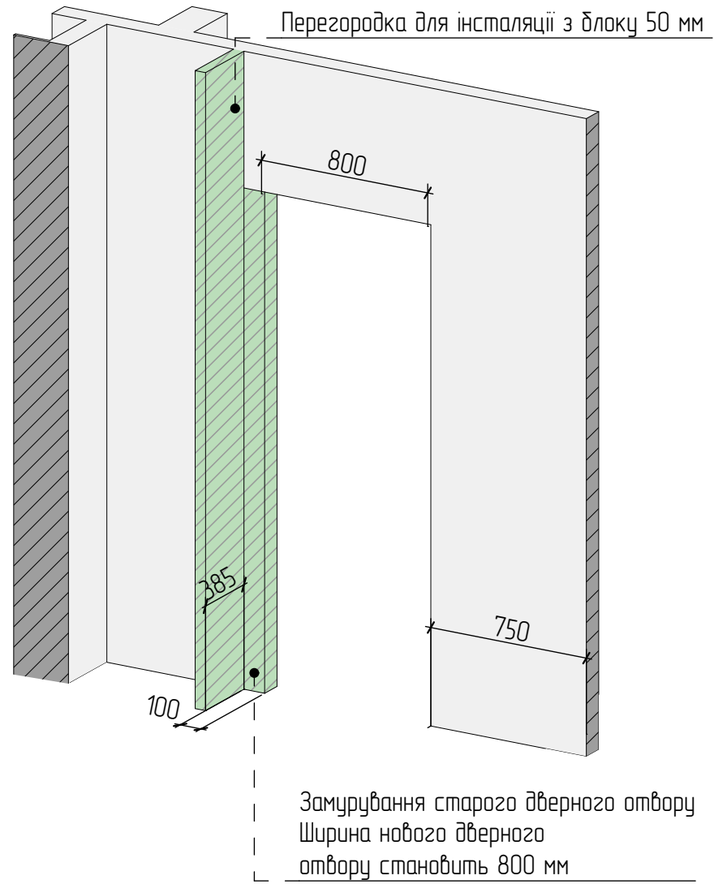

Замурування старого дверного отвору
Ширина нового дверного
отвору становить 800 мм


Монтаж. Вигляд 5

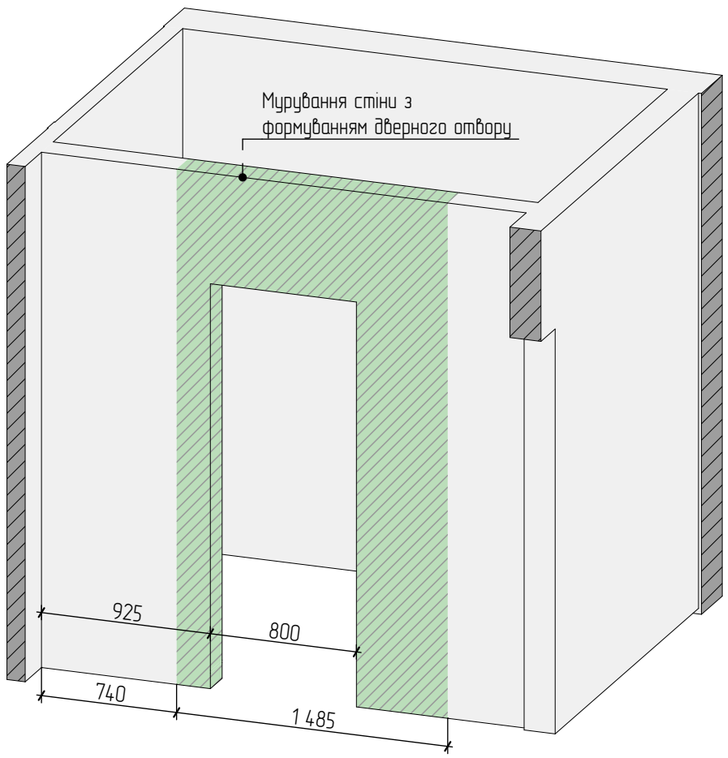

iSD IHOR SAYEVICH interior designer	м. Львів, вул. Трускавецька ЖК Парус Smart	Розділ	Аркуш	Аркушів
	План монтажу. 3D схеми	РП-ТК	12	55
	Ihor Sayevich Designer @ihor_sayevich_designer +380 97 585 91 01			

План розташування гіпсокартонних конструкцій. Поверх 1

М1:35

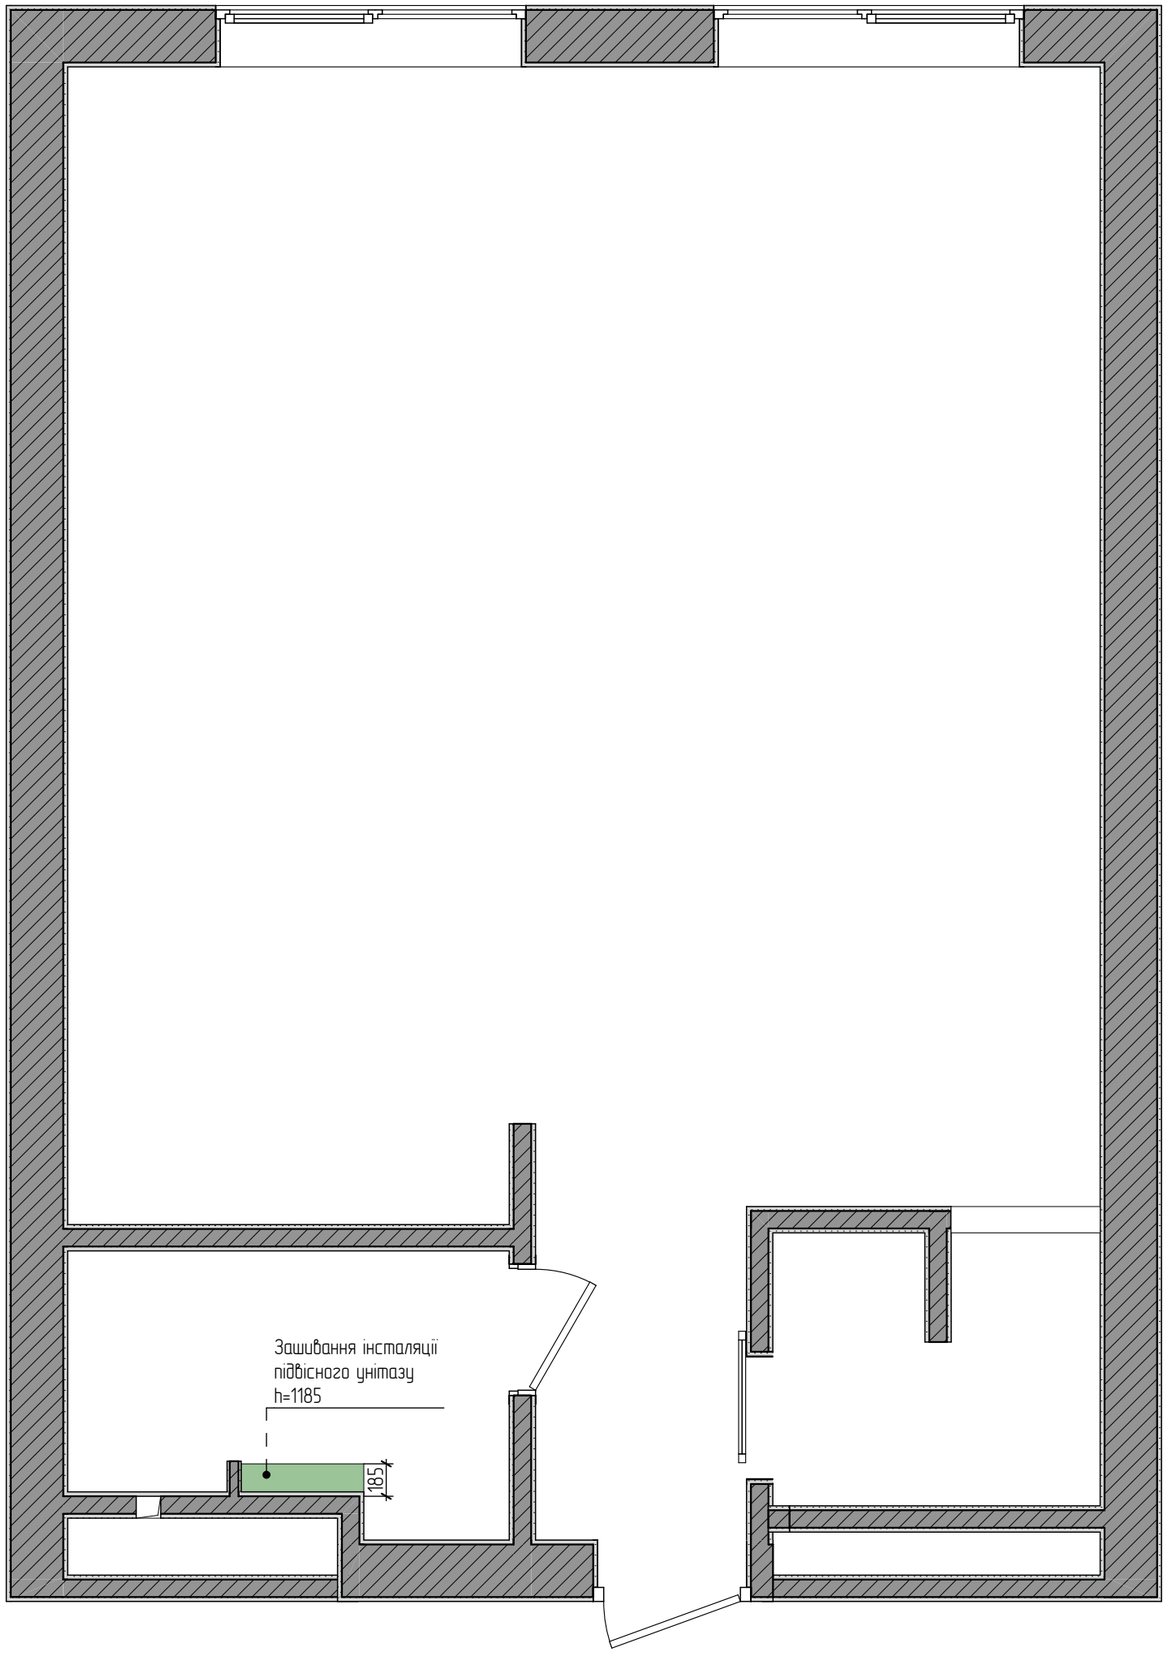

Умовні позначення:


– гіпсокартонні конструкції

Примітки:

Розміри вказані для прорахунку основних будівельних та оздоблювальних матеріалів.
Перед початком роботи і закупівлею матеріалів розміри перевірити на об'єкті!

IHOR SAYEVICH interior designer	м. Львів, вул. Трускавецька ЖК Парус Smart	Розділ	Аркуш	Аркушів
	План розташування гіпсокартонних конструкцій. Поверх 1	РП-ТК	13	55
	Ihor Sayevich Designer	@ihor_sayevich_designer	+380 97 585 91 01	

План розташування гіпсокартонних конструкцій. Поверх 2

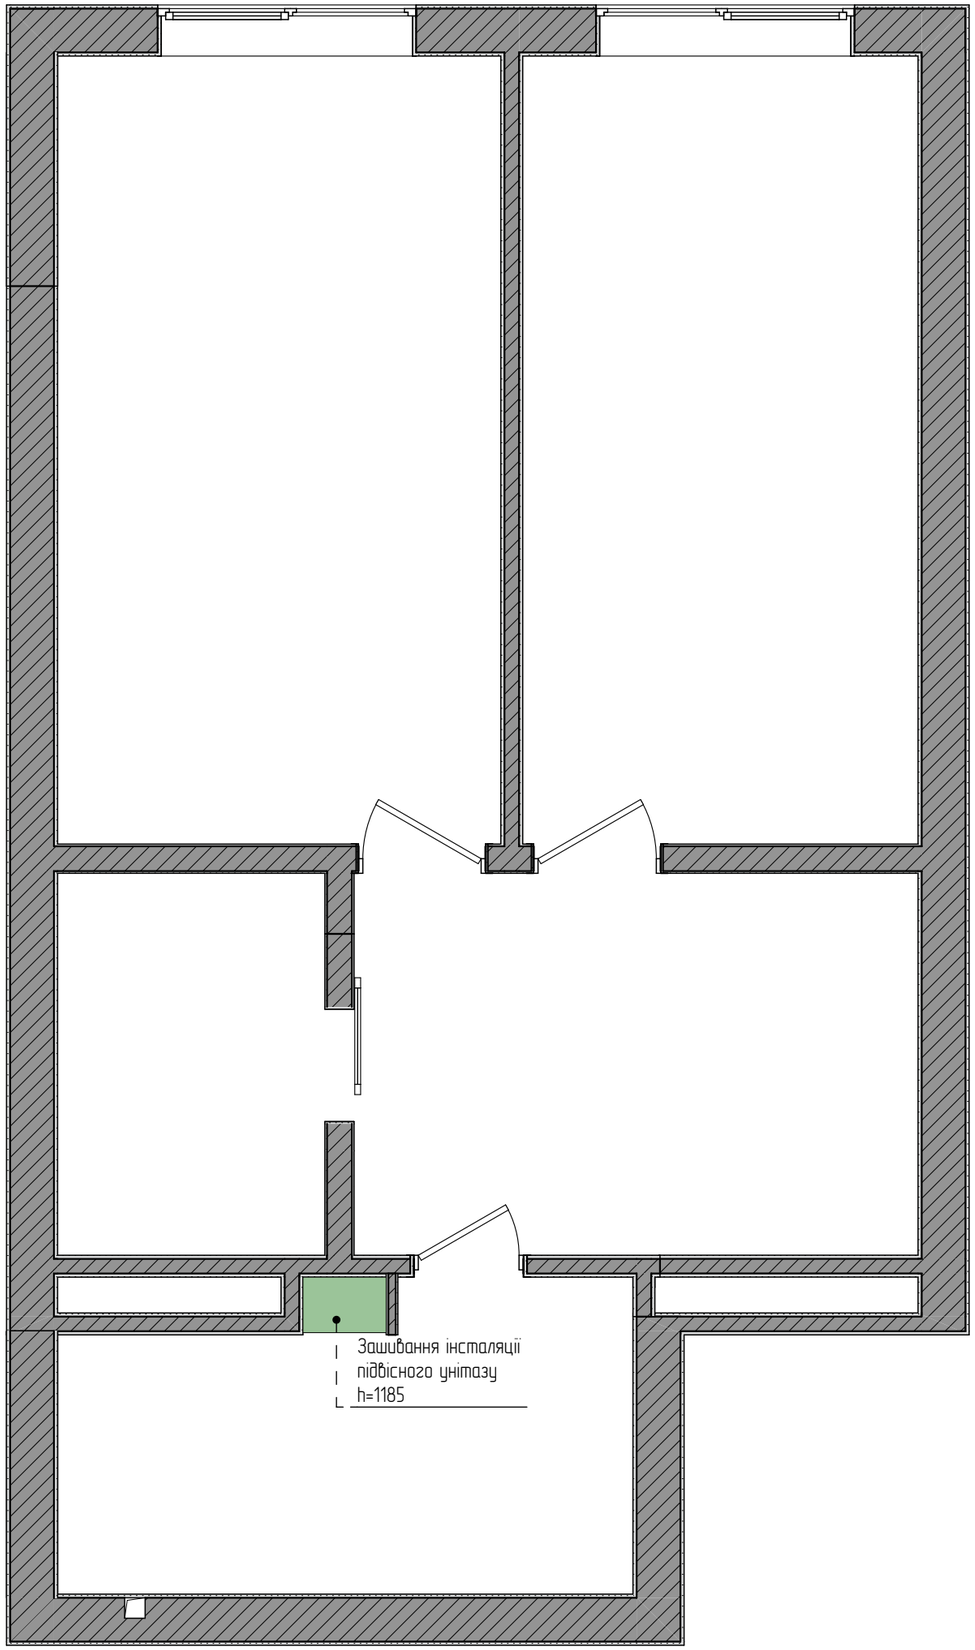

Умовні позначення:


– гіпсокартонні конструкції

Примітки:

Розміри вказані для прорахунку основних будівельних та оздоблювальних матеріалів.
Перед початком роботи і закупівлею матеріалів розміри перевірити на об'єкті!

IHOR SAYEVICH interior designer	м. Львів, вул. Трускавецька ЖК Парус Smart	Розділ	Аркуш	Аркушів
	План розташування гіпсокартонних конструкцій. Поверх 1	РП-ТК	14	55
	Ihor Sayevich Designer	@ihor_sayevich_designer	+380 97 585 91 01	

Презентаційний план. Поверх 1
М1:35

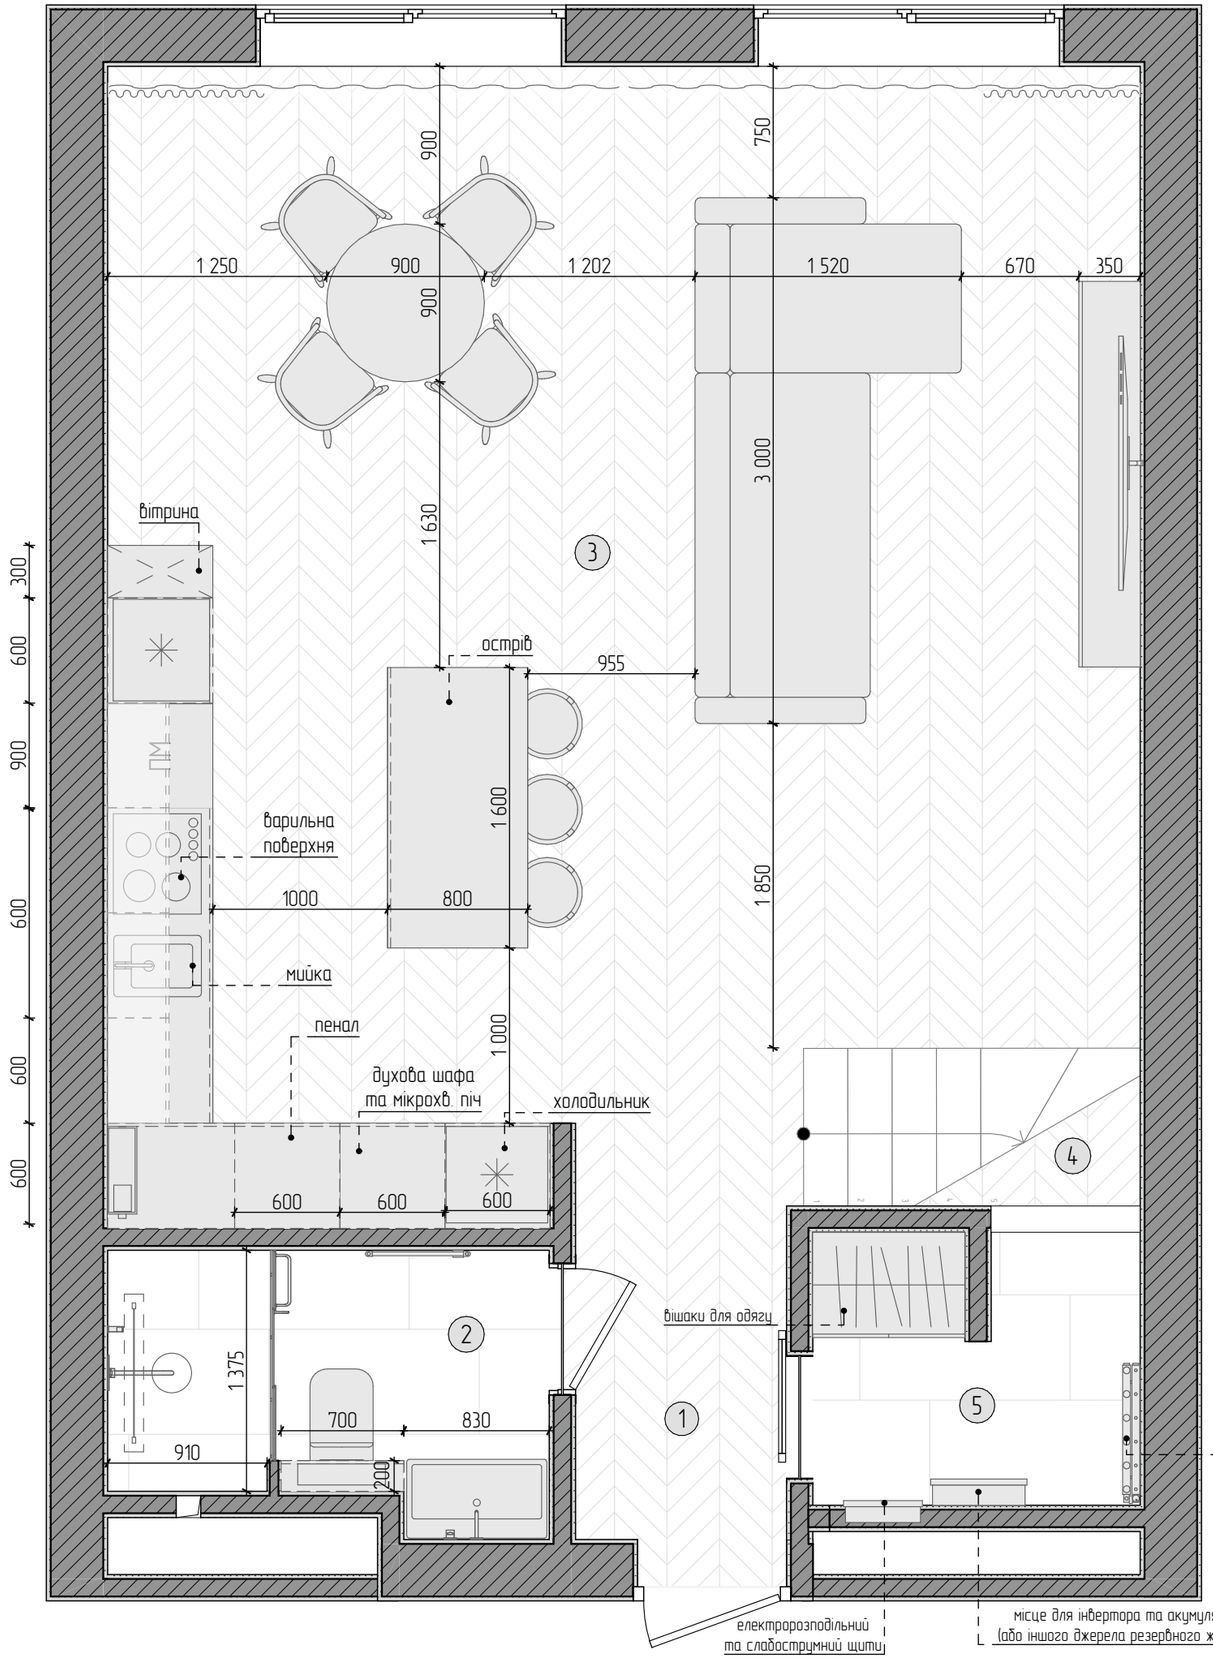

Експлікація приміщення

№	Найменування	Площа м.кв.	Примітка
1	Вхідна група	2,57	
2	Ванна кімната	3,90	
3	Кухня-студія	39,31	
4	Сходова частина	4,05	
5	Кладова-гардероб	3,02	
6	Коридор	6,83	
7	Ванна кімната	8,18	
8	Гардероб	4,96	
9	Спальня	16,76	
10	Кабінет	14,98	
		104,56 м²	

Умовні позначення:


– існуючі стіни

Примітки:

Розміри вказані для прорахунку основних будівельних та оздоблювальних матеріалів.
Дане креслення дивитись з візуалізаціями, розгортками та специфікацією.
Детальні розміри та конструкції меблевих та сантехнічних елементів вказані у специфікації та в технічній частині проєкту.

IHOR SAYEVICH interior designer	м. Львів, вул. Трускавецька ЖК Парус Smart	Розділ	Аркуш	Аркушів
	Презентаційний план. Поверх 2	РП-ТК	15	55
	Ihor Sayevich Designer	@ihor_sayevich_designer	+380 97 585 91 01	

Презентаційний план. Поверх 2

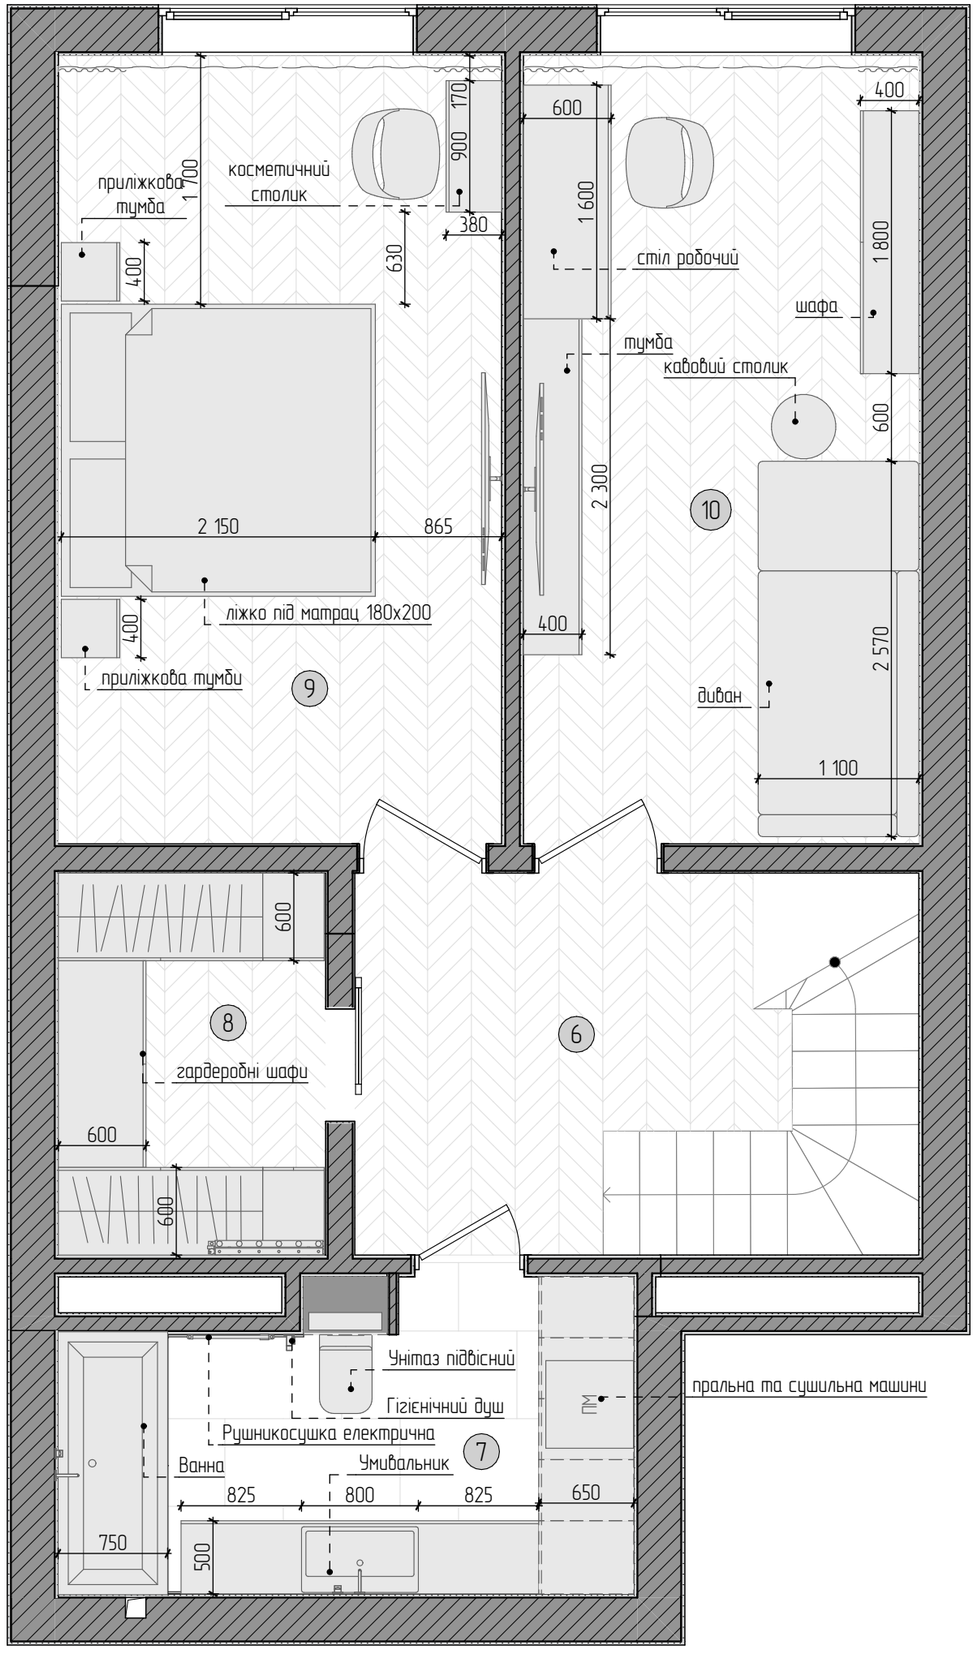

Експлікація приміщення

№	Найменування	Площа м.кв.	Примітка
1	Вхідна група	2,57	
2	Ванна кімната	3,90	
3	Кухня-студія	39,31	
4	Сходова частина	4,05	
5	Кладова-гардероб	3,02	
6	Коридор	6,83	
7	Ванна кімната	8,18	
8	Гардероб	4,96	
9	Спальня	16,76	
10	Кабінет	14,98	
		104,56 м²	

Умовні позначення:


– існуючі стіни

Примітки:

Розміри вказані для прорахунку основних будівельних та оздоблювальних матеріалів.
Дане креслення дивитись з візуалізаціями, розгортками та специфікацією.
Детальні розміри та конструкції меблевих та сантехнічних елементів вказані у специфікації та в технічній частині проєкту.

IHOR SAYEVICH interior designer	м. Львів, вул. Трускавецька ЖК Парус Smart	Розділ	Аркуш	Аркушів
	Презентаційний план. Поверх 1	РП-ТК	16	55
	Ihor Sayevich Designer	@ihor_sayevich_designer	+380 97 585 91 01	

План кондиціонування і вентиляції
М1:35

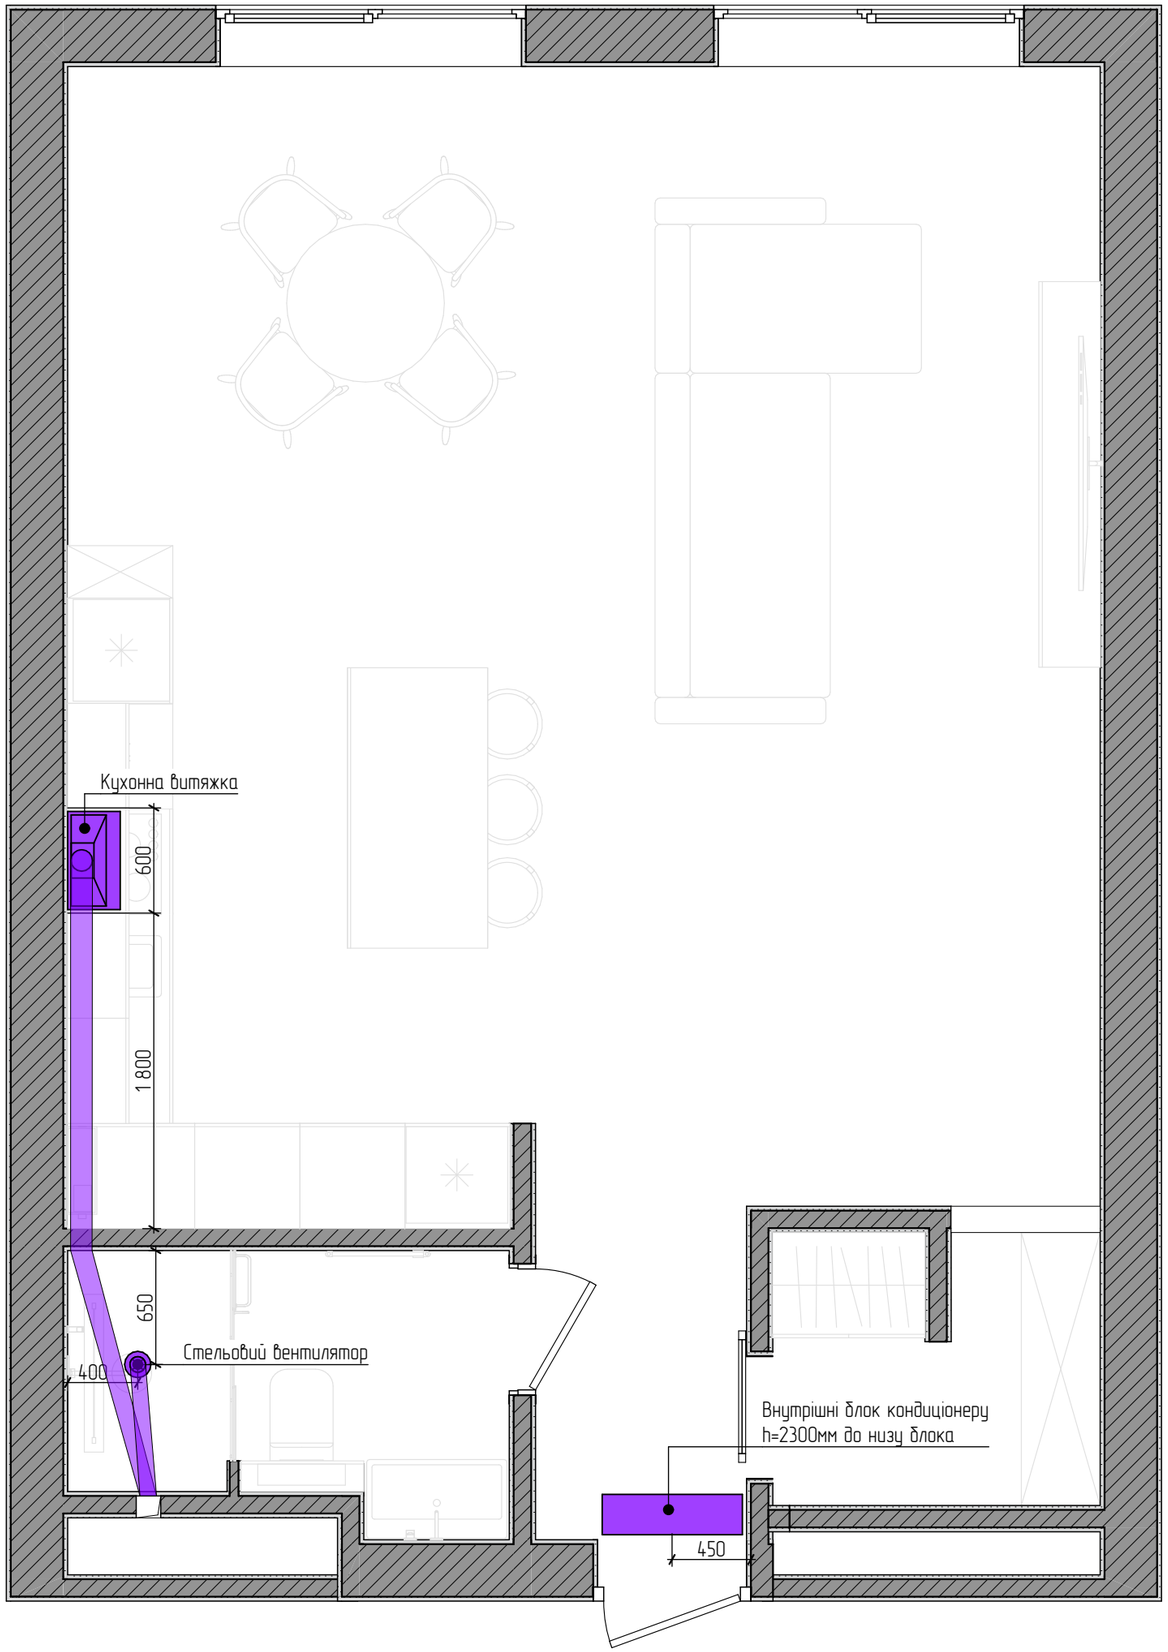

Умовні позначення:

– внутрішній блок кондиціонера


– стельовий вентилятор

Примітки:

1. Усі розміри вказані у мм усі розміри та прив'язки уточнити по місцю
2. Усі висотні відмітки дані від рівня чистової підлоги;
3. Необхідні параметри та потужність кондиціонерів узгодити зі спеціалістами. Рекомендується до початку ремонтних робіт звернутись до підрядника з кондиціонування для піддору оптимального варіанту.
4. Розміщення зовнішніх блоків згідно норм забудовника;
5. Сховати траси комунікацій в стінах та стелі. Схеми розміщення трас комунікацій визначається монтажником обладнання;
6. Потужність стельового вентилятора визначає підрядник згідно потреб приміщення

iSD IHOR SAYEVICH interior designer	м. Львів, вул. Трускавецька ЖК Парус Smart	Розділ	Аркуш	Аркушів
	План кондиціонування та вентиляції. Поверх 1	РП-ТК	17	55
	Ihor Sayevich Designer	@ihor_sayevich_designer	+380 97 585 91 01	

План кондиціонування та вентиляції

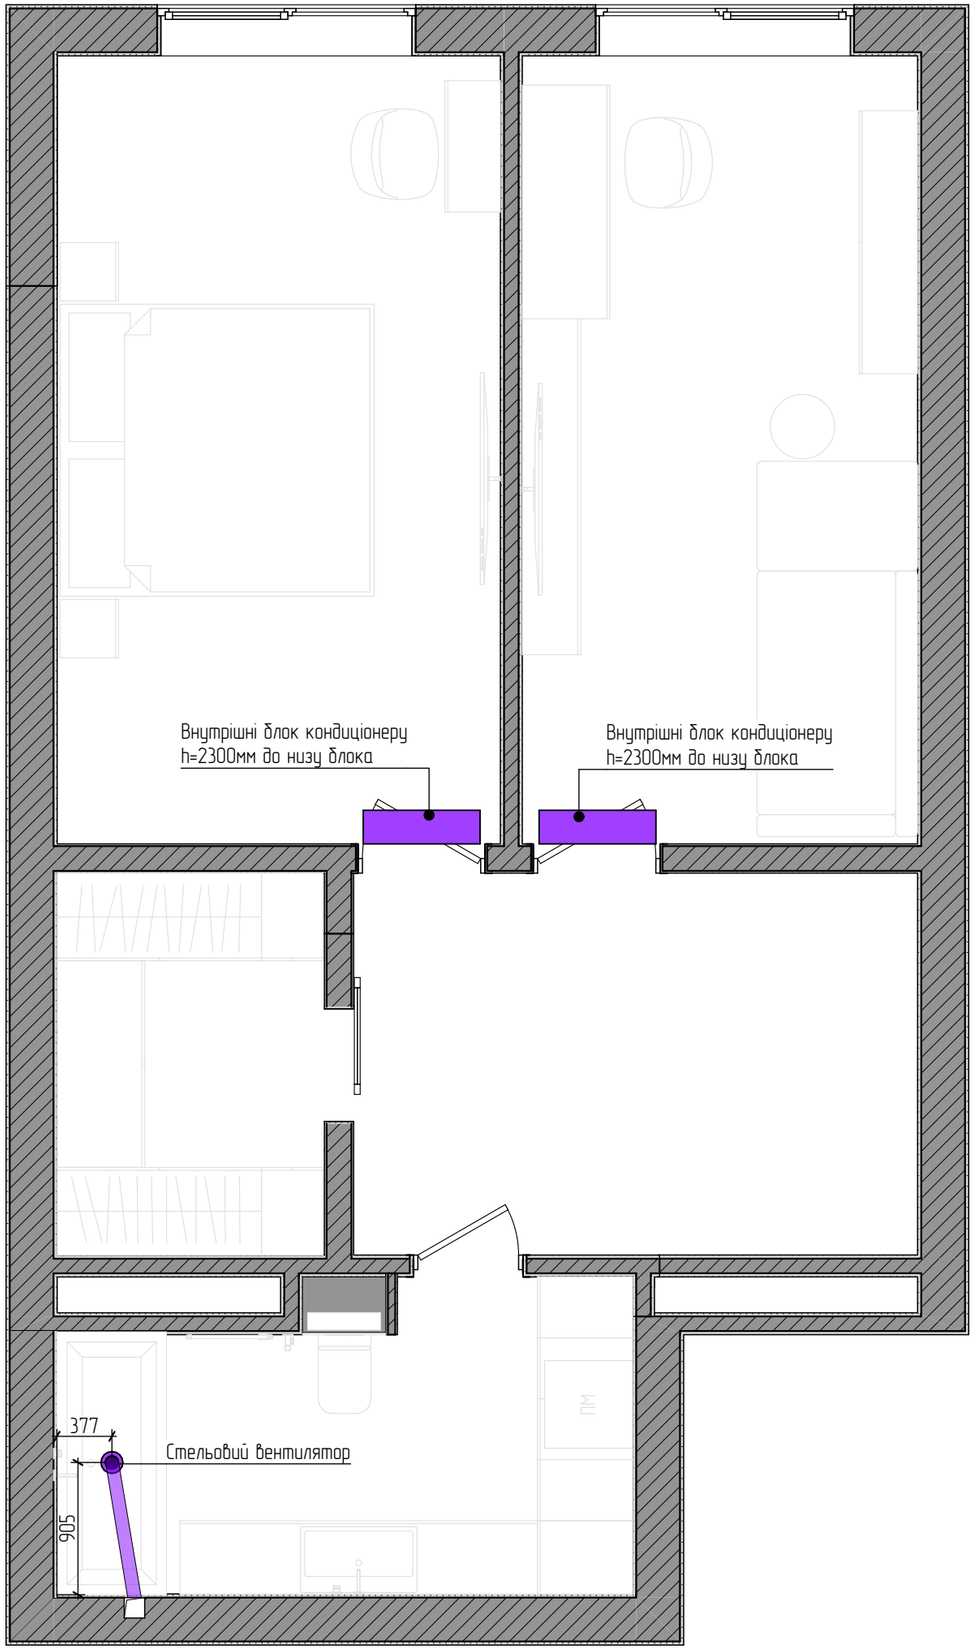

Умовні позначення:

– внутрішній блок кондиціонера

– стельовий вентилятор


Примітки:

1. Усі розміри вказані у мм усі розміри та прив'язки уточнити по місцю
2. Усі висотні відмітки дані від рівня чистової підлоги;
3. Необхідні параметри та потужність кондиціонерів узгодити зі спеціалістами. Рекомендується до початку ремонтних робіт звернутись до підрядника з кондиціонування для підбору оптимального варіанту.
4. Розміщення зовнішніх блоків згідно норм забудовника;
5. Сховати траси комунікацій в стінах та стелі. Схеми розміщення трас комунікацій визначається монтажником обладнання;
6. Потужність стельового вентилятора визначає підрядник згідно потреб приміщення

iSD IHOR SAYEVICH interior designer	м. Львів, вул. Трускавецька ЖК Парус Smart	Розділ	Аркуш	Аркушів
	План кондиціонування та вентиляції. Поверх 2	РП-ТК	18	55
	Ihor Sayevich Designer	@ihor_sayevich_designer	+380 97 585 91 01	

План розташування підігріву підлоги і опалювальних приладів. Поверх 1

М1:35

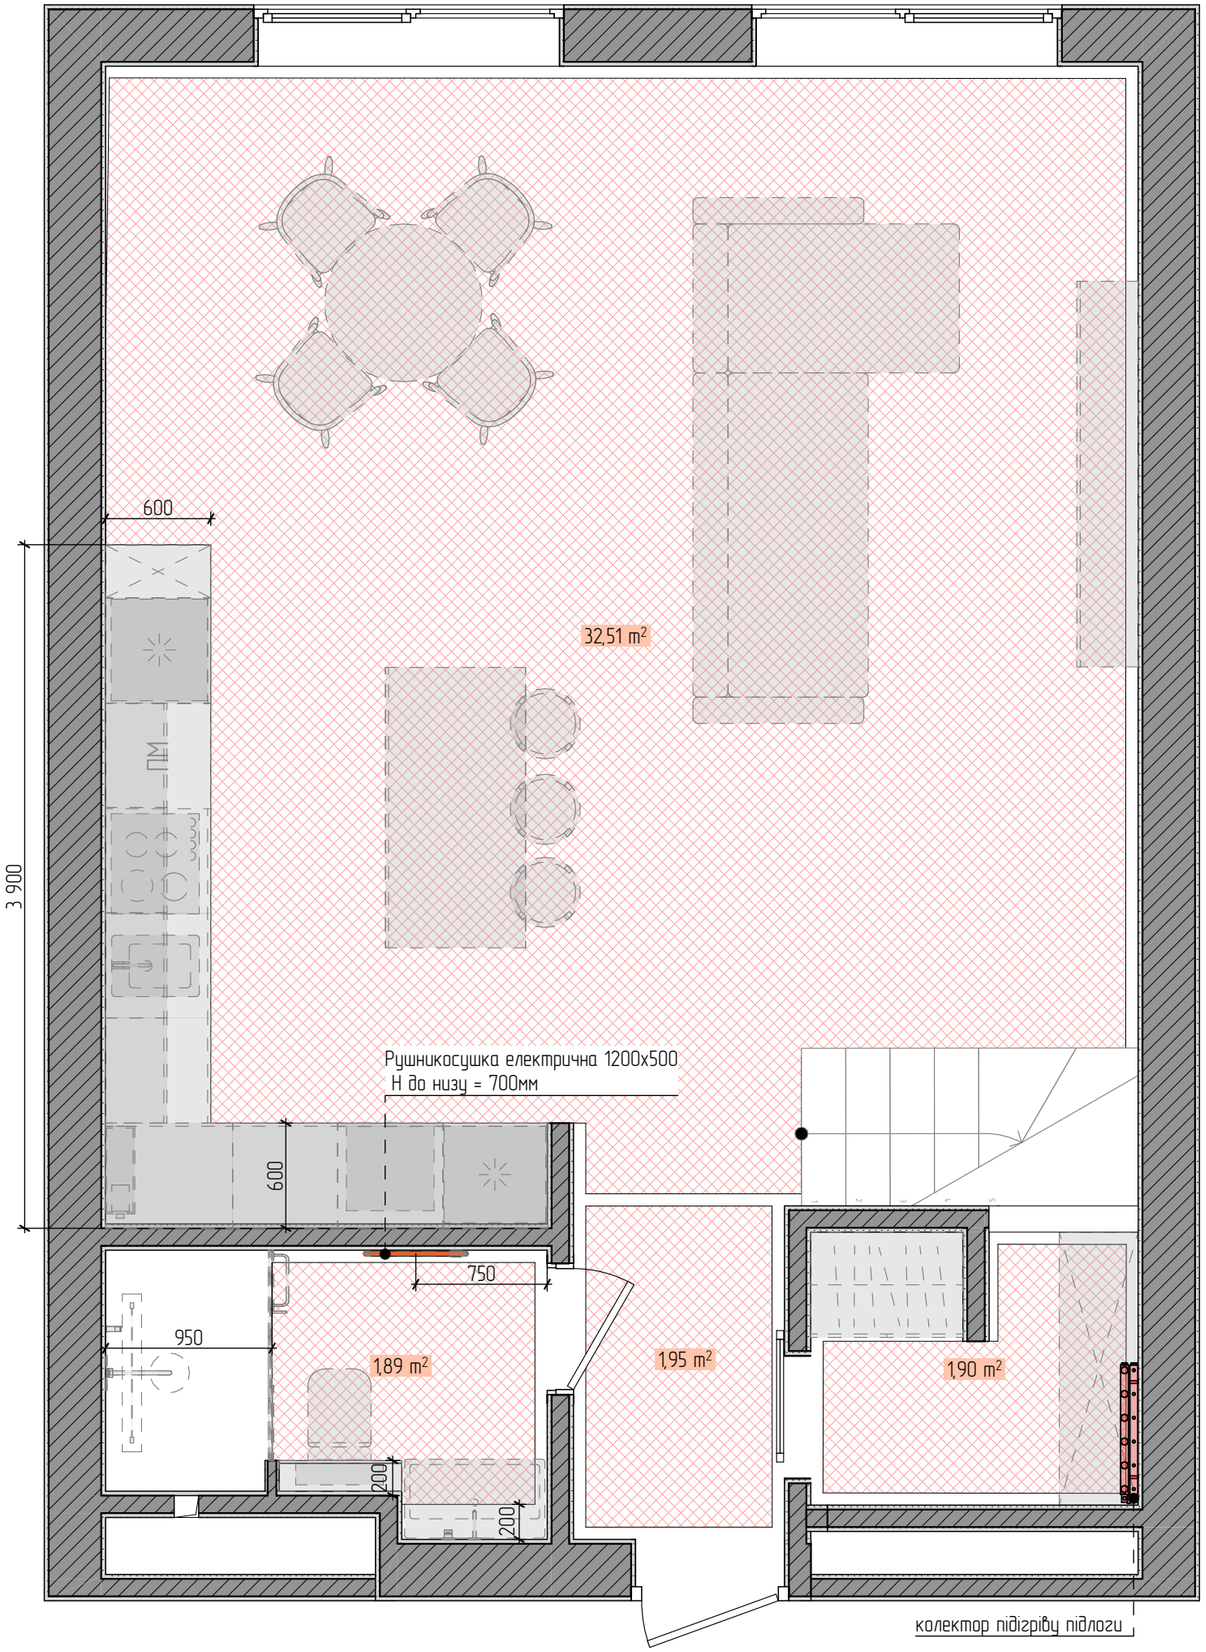

Умовні позначення:

– тепла підлога

– колектор теплої підлоги


Площа теплої підлоги (поверх 1) – 38,15 м²
Площа теплої підлоги (поверх 2) – 41,63 м²
Загальна площа теплої підлоги – 79,78 м²

Примітки:

1. Усі розміри вказані у мм;
2. Тип, необхідні параметри та потужність теплої підлоги узгодити із профільними спеціалістами;
3. Зони є автономними
4. Розміри радіаторів опалення закласти відповідно до розрахунку інженера-сантехніка.Точні розміри та потужність радіаторів підібрати інженеру по опаленні відносно тепловтратам!!!

IHOR SAYEVICH interior designer	м. Львів, вул. Трускавецька ЖК Парус Smart	Розділ	Аркуш	Аркушів
	План розташування підігріву підлоги і опалювальних приладів	РП-ТК	19	55
	Ihor Sayevich Designer	@ihor_sayevich_designer	+380 97 585 91 01	

План розташування підігріву підлоги та опалювальний приладів. Поверх 2

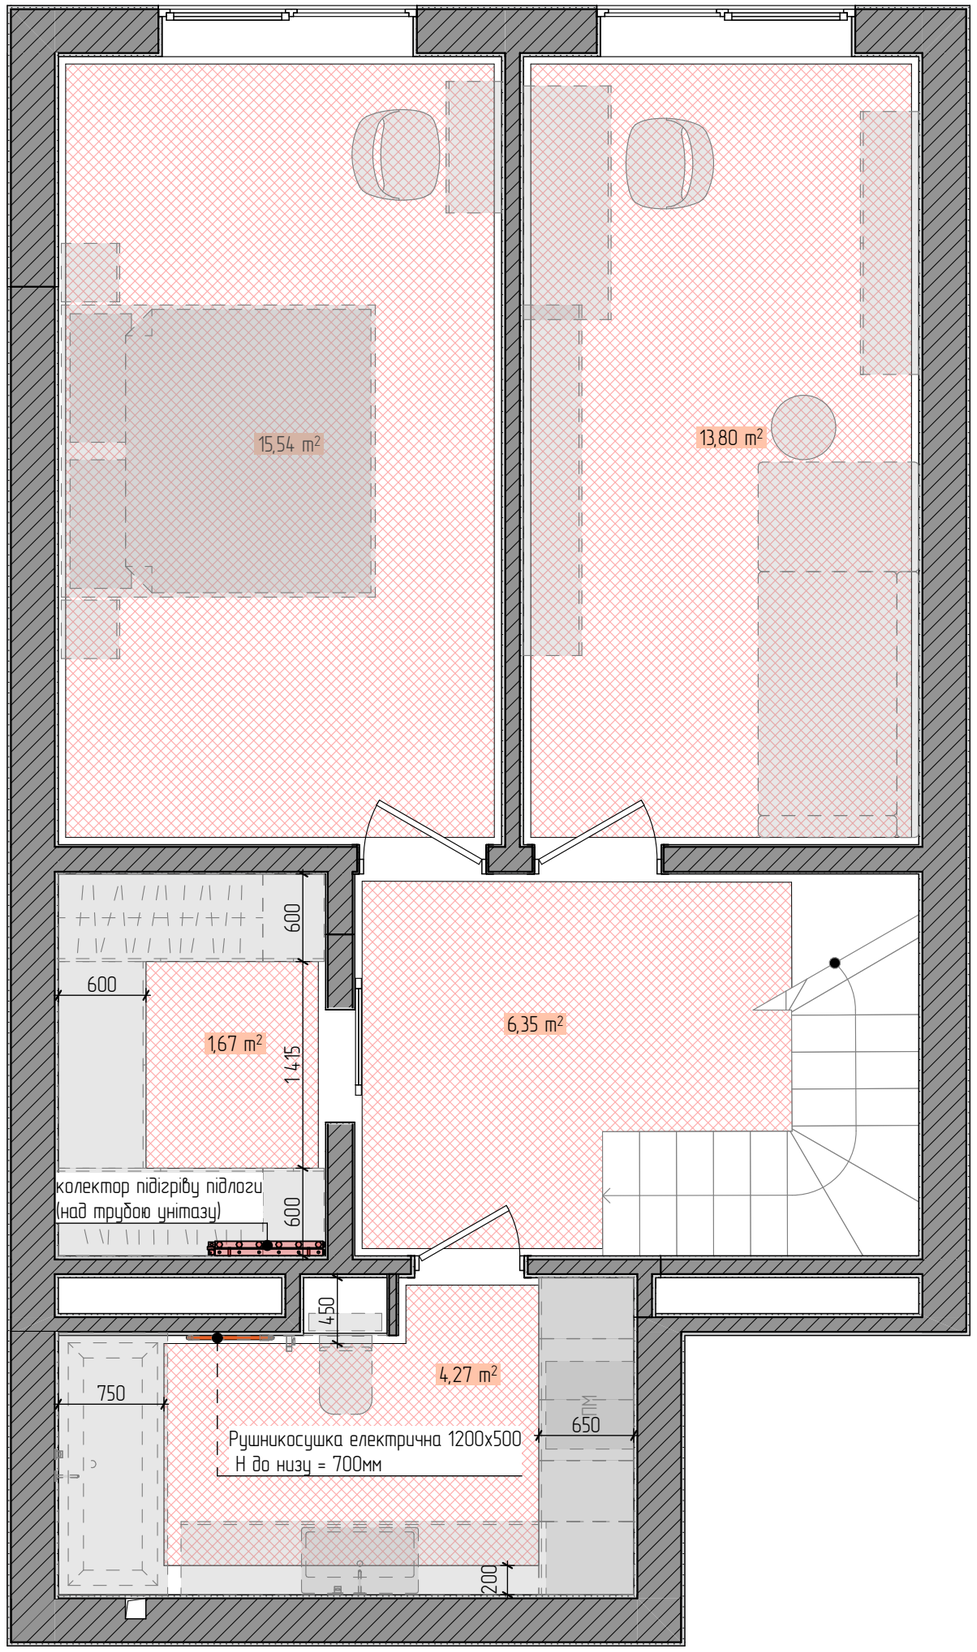

Умовні позначення:

– тепла підлога

– колектор теплої підлоги


Площа теплої підлоги (поверх 1) – 38,15 м²
Площа теплої підлоги (поверх 2) – 41,63 м²
Загальна площа теплої підлоги – 79,78 м²

Примітки:

1. Усі розміри вказані у мм;
2. Тип, необхідні параметри та потужність теплої підлоги узгодити із профільними спеціалістами;
3. Зони є автономними
4. Розміри радіаторів опалення закласти відповідно до розрахунку інженера-сантехніка.Точні розміри та потужність радіаторів підібрати інженеру по опаленні відносно тепловтратам!!!

IHOR SAYEVICH interior designer	м. Львів, вул. Трускавецька ЖК Парус Smart	Розділ	Аркуш	Аркушів
	План розташування підігріву підлоги та опалювальних приладів. Поверх 2	РП-ТК	20	55
	Ihor Sayevich Designer	@ihor_sayevich_designer	+380 97 585 91 01	

Приміщення 2 (Ванна кімната)

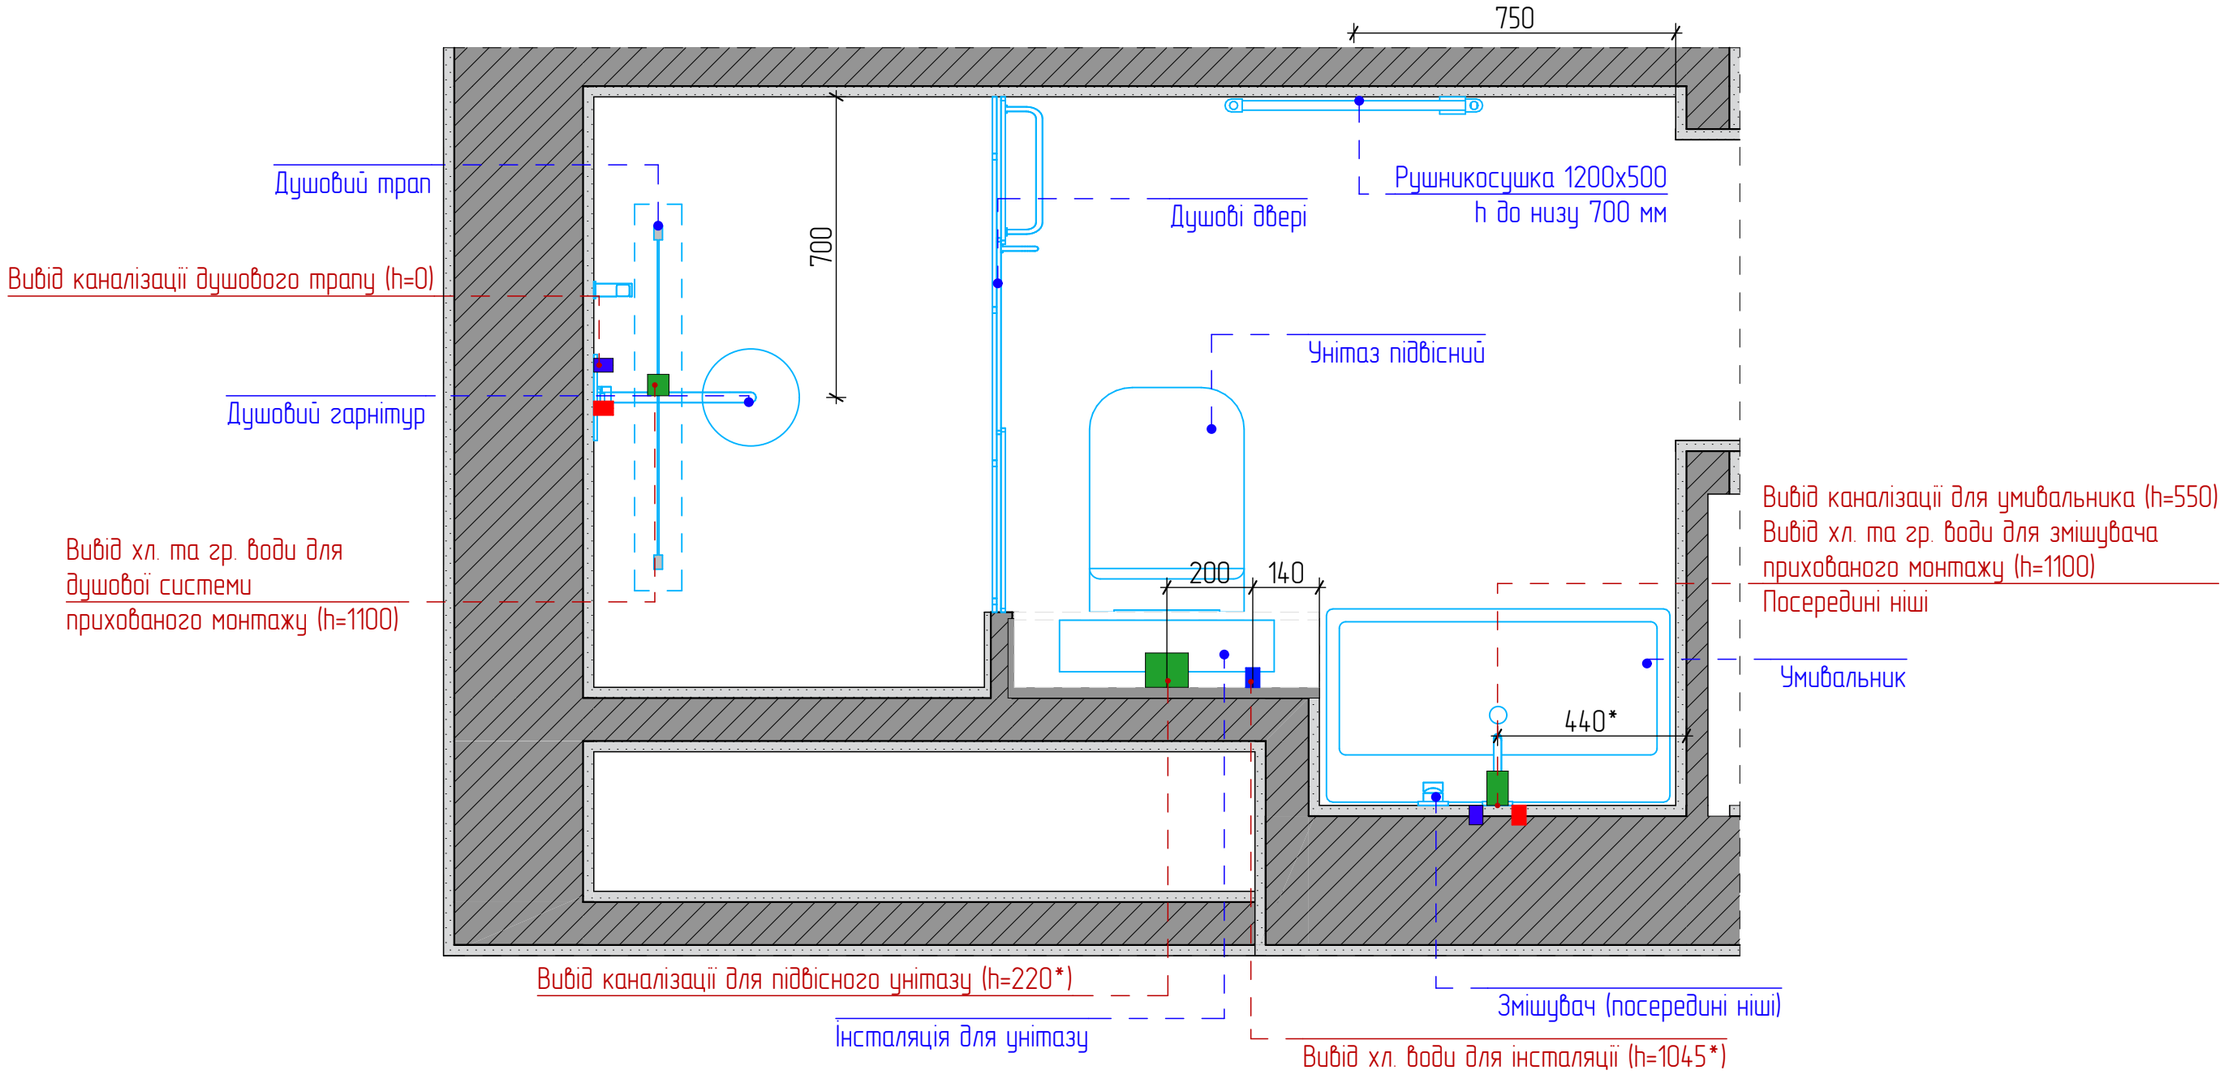

Умовні позначення:

– виводи гарячої та холодної води

– вивід каналізації


– існуючі стіни

Примітки:

1. Усі розміри вказані у мм;
2. Усі висотні відмітки дані від рівня чистової підлоги;
3. Прив'язки подано до центрів обладнання та виводів;
4. Сантехнічна фурнітура (тип, модель) вказані у специфікації;
5. Відстані та місце виводу води для бойлера визначити по факту при наявності бойлера!

IHOR SAYEVICH interior designer	м. Львів, вул. Трускавецька ЖК Парус Smart	Розділ	Аркуш	Аркушів
	План-схема розташування сантехнічного обладнання. Поверх 1	РП-ТК	21	55
	Ihor Sayevich Designer @ihor_sayevich_designer +380 97 585 91 01			

Приміщення 3 (Зона кухні)

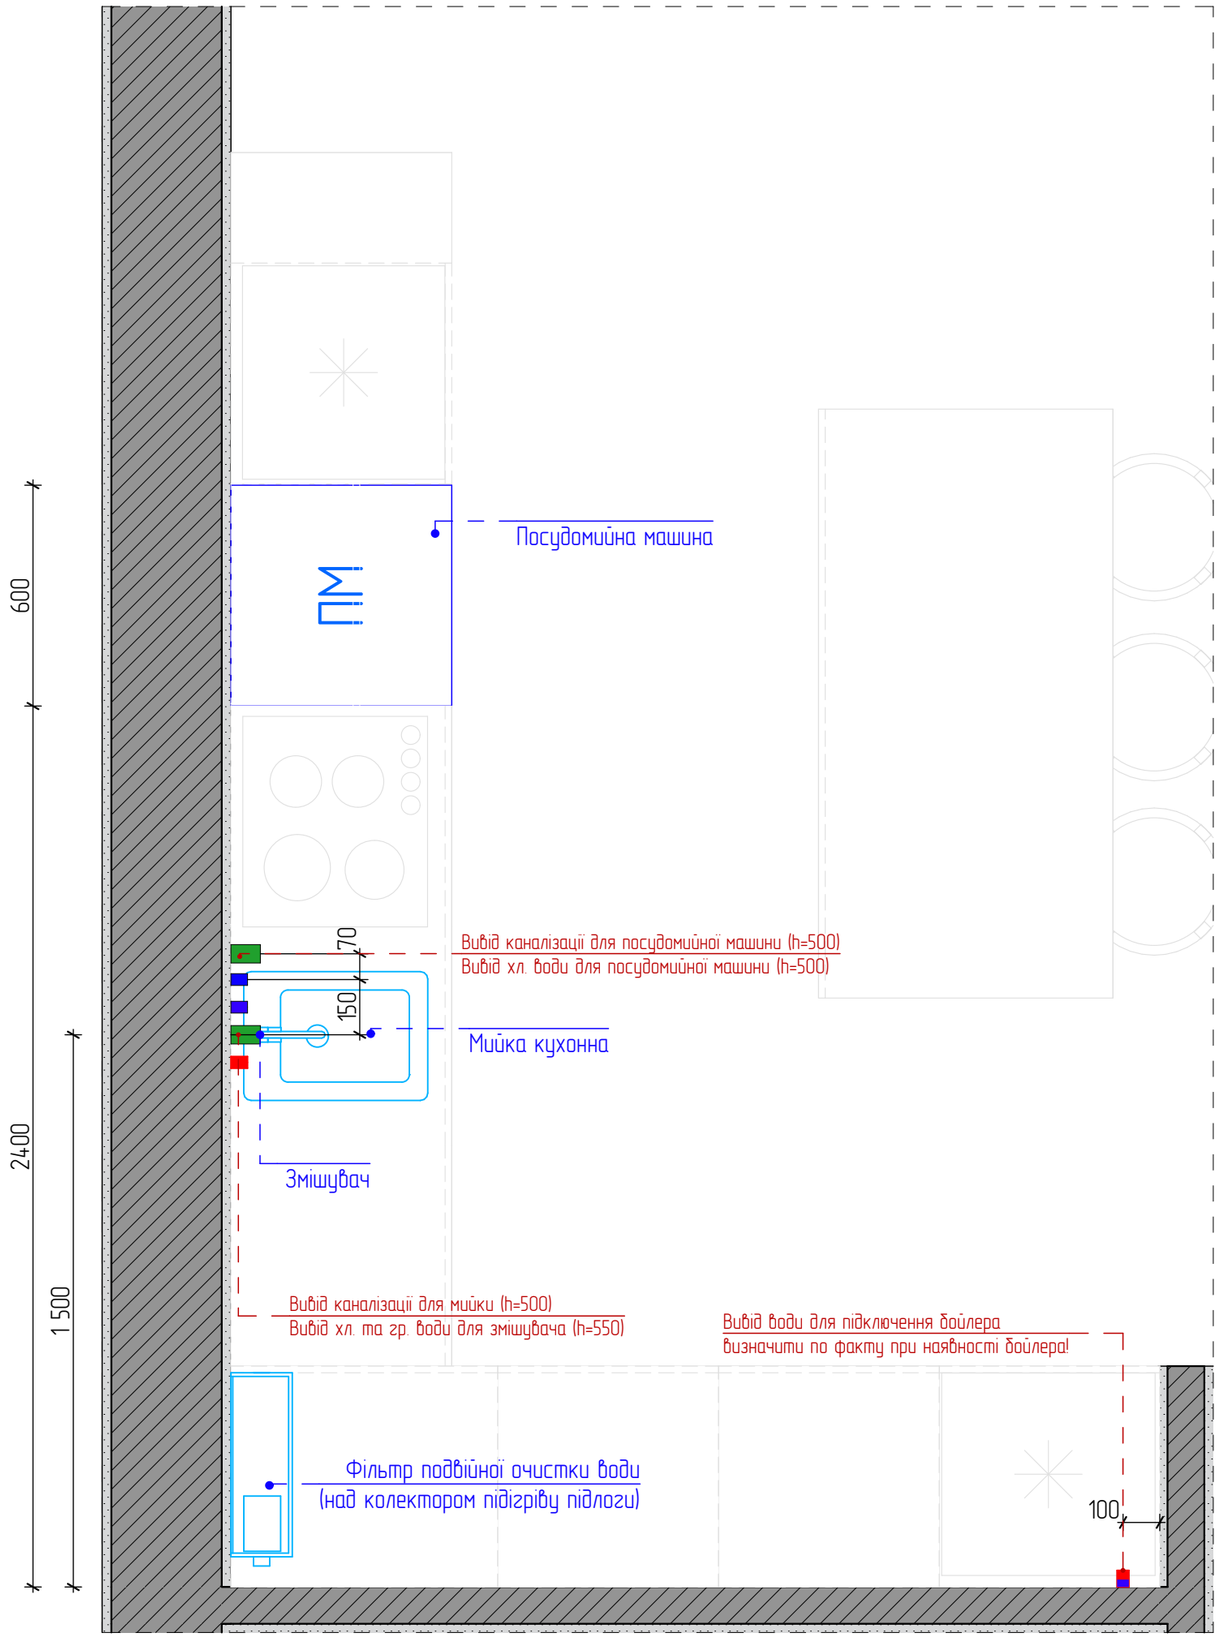

Умовні позначення:

– виводи гарячої та холодної води

– вивід каналізації


– існуючі стіни

Примітки:

1. Усі розміри вказані у мм;
2. Усі висотні відмітки дані від рівня чистової підлоги;
3. Прив'язки подано до центрів обладнання та виводів;
4. Сантехнічна фурнітура (тип, модель) вказані у специфікації;
5. Відстані та місце виводу води для бойлера визначити по факту при наявності бойлера!

iSD IHOR SAYEVICH interior designer	м. Львів, вул. Трускавецька ЖК Парус Smart	Розділ	Аркуш	Аркушів
	План-схема розташування сантехнічного обладнання. Поверх 1	РП-ТК	22	55
	Ihor Sayevich Designer	@ihor_sayevich_designer	+380 97 585 91 01	

Приміщення 7 (Ванна кімната)

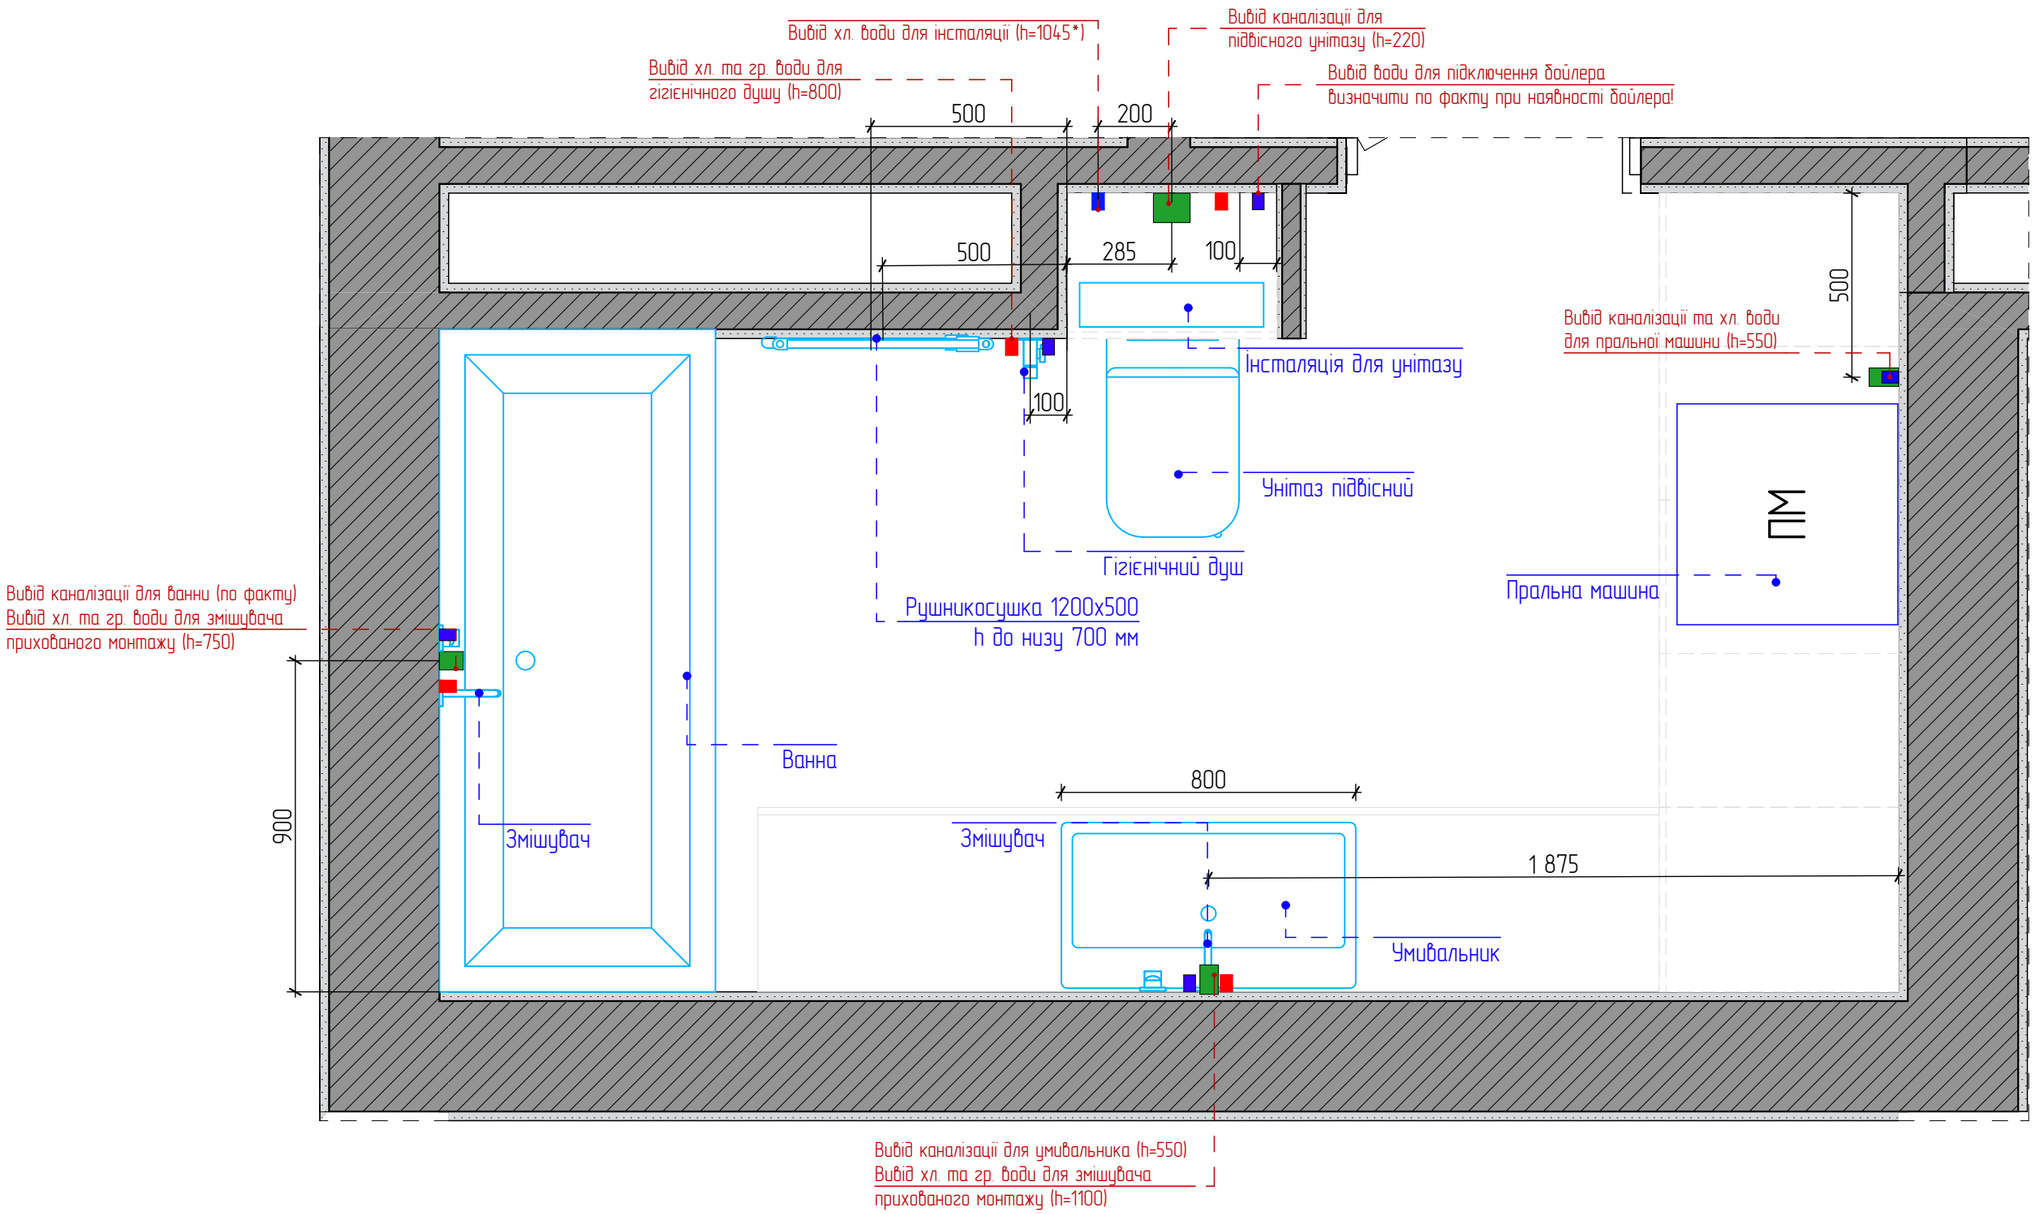

Умовні позначення:

– виводи гарячої та холодної води

– вивід каналізації


– існуючі стіни

Примітки:

1. Усі розміри вказані у мм;
2. Усі висотні відмітки дані від рівня чистової підлоги;
3. Прив'язки подано до центрів обладнання та виводів;
4. Сантехнічна фурнітура (тип, модель) вказані у специфікації;
5. Відстані та місце виводу води для бойлера визначити по факту при наявності бойлера!

IHOR SAYEVICH interior designer	м. Львів, вул. Трускавецька ЖК Парус Smart	Розділ	Аркуш	Аркушів
	План-схема розташування сантехнічного обладнання. Поверх 2	РП-ТК	23	55
	Ihor Sayevich Designer	@ihor_sayevich_designer	+380 97 585 91 01	

План розташування електрофурнітури
М1:35

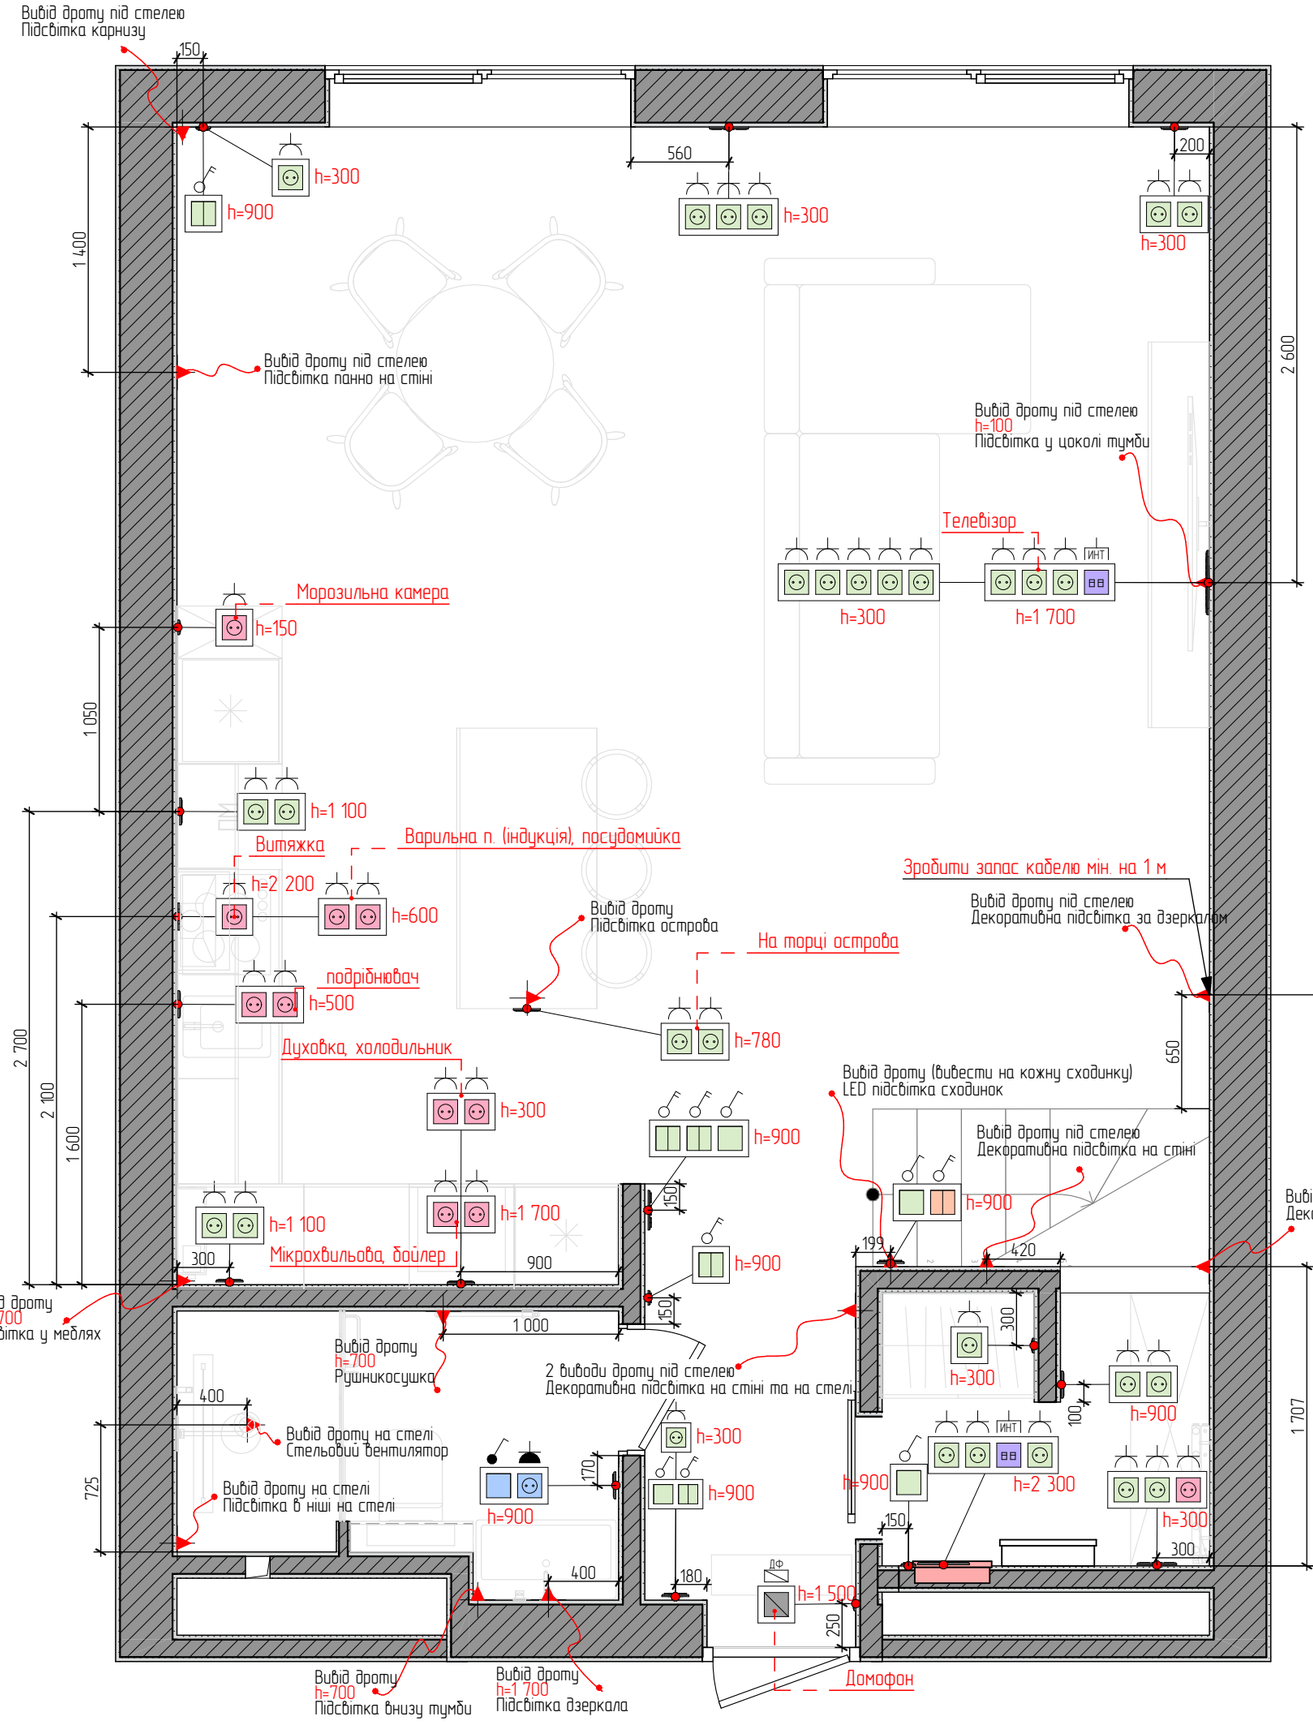

Специфікація рамок			
Тип рамки (блока)	Рамка орієнтація	К-сть	Примітки
Рамка х1			
	Горизонтальна	20	
Рамка х2			
	Горизонтальна	25	
Рамка х3			
	Горизонтальна	8	
Рамка х4			
	Горизонтальна	4	
Рамка х5			
	Горизонтальна	1	

Умовні позначення:

- – електрощит
- – майстер-вимикач
- – прохідний вимикач одноклавішний
- – прохідний вимикач двоклавішний
- – вимикач одноклавішний
- – вимикач двоклавішний
- – вимикач двоклавішний вологостійкий
- – вимикач одноклавішний вологостійкий
- – розетка
- – розетка із заземленням
- – розетка вологостійка
- – розетка мережева
- – вивід електричного живлення

Примітки:


1. Усі розміри вказані у мм від штукатурки;
2. Усі висотні дані від рівня чистової підлоги;
3. Усі плани електрики розглядати паралельно;
4. Прив'язки подано до центру вимикача, блока;
5. Блоки розташовані горизонтально, якщо не вказано інше!
6. Трансформатори від LED стрічок винести у електричний щит
7. Місце виводу електричного живлення для рушникосушки, а також розетки для бойлера уточнити згідно з характеристиками вибраного обладнання;

IHOR SAYEVICH
interior designer

м. Львів, вул. Трускавецька ЖК Парус Smart	Розділ	Аркуш	Аркушів
План розташування електрофурнітури. Поверх 1	РП-ТК	24	55

Ihor Sayevich Designer @ihor_sayevich_designer +380 97 585 91 01

План розташування електрофурнітури. Поверх 2

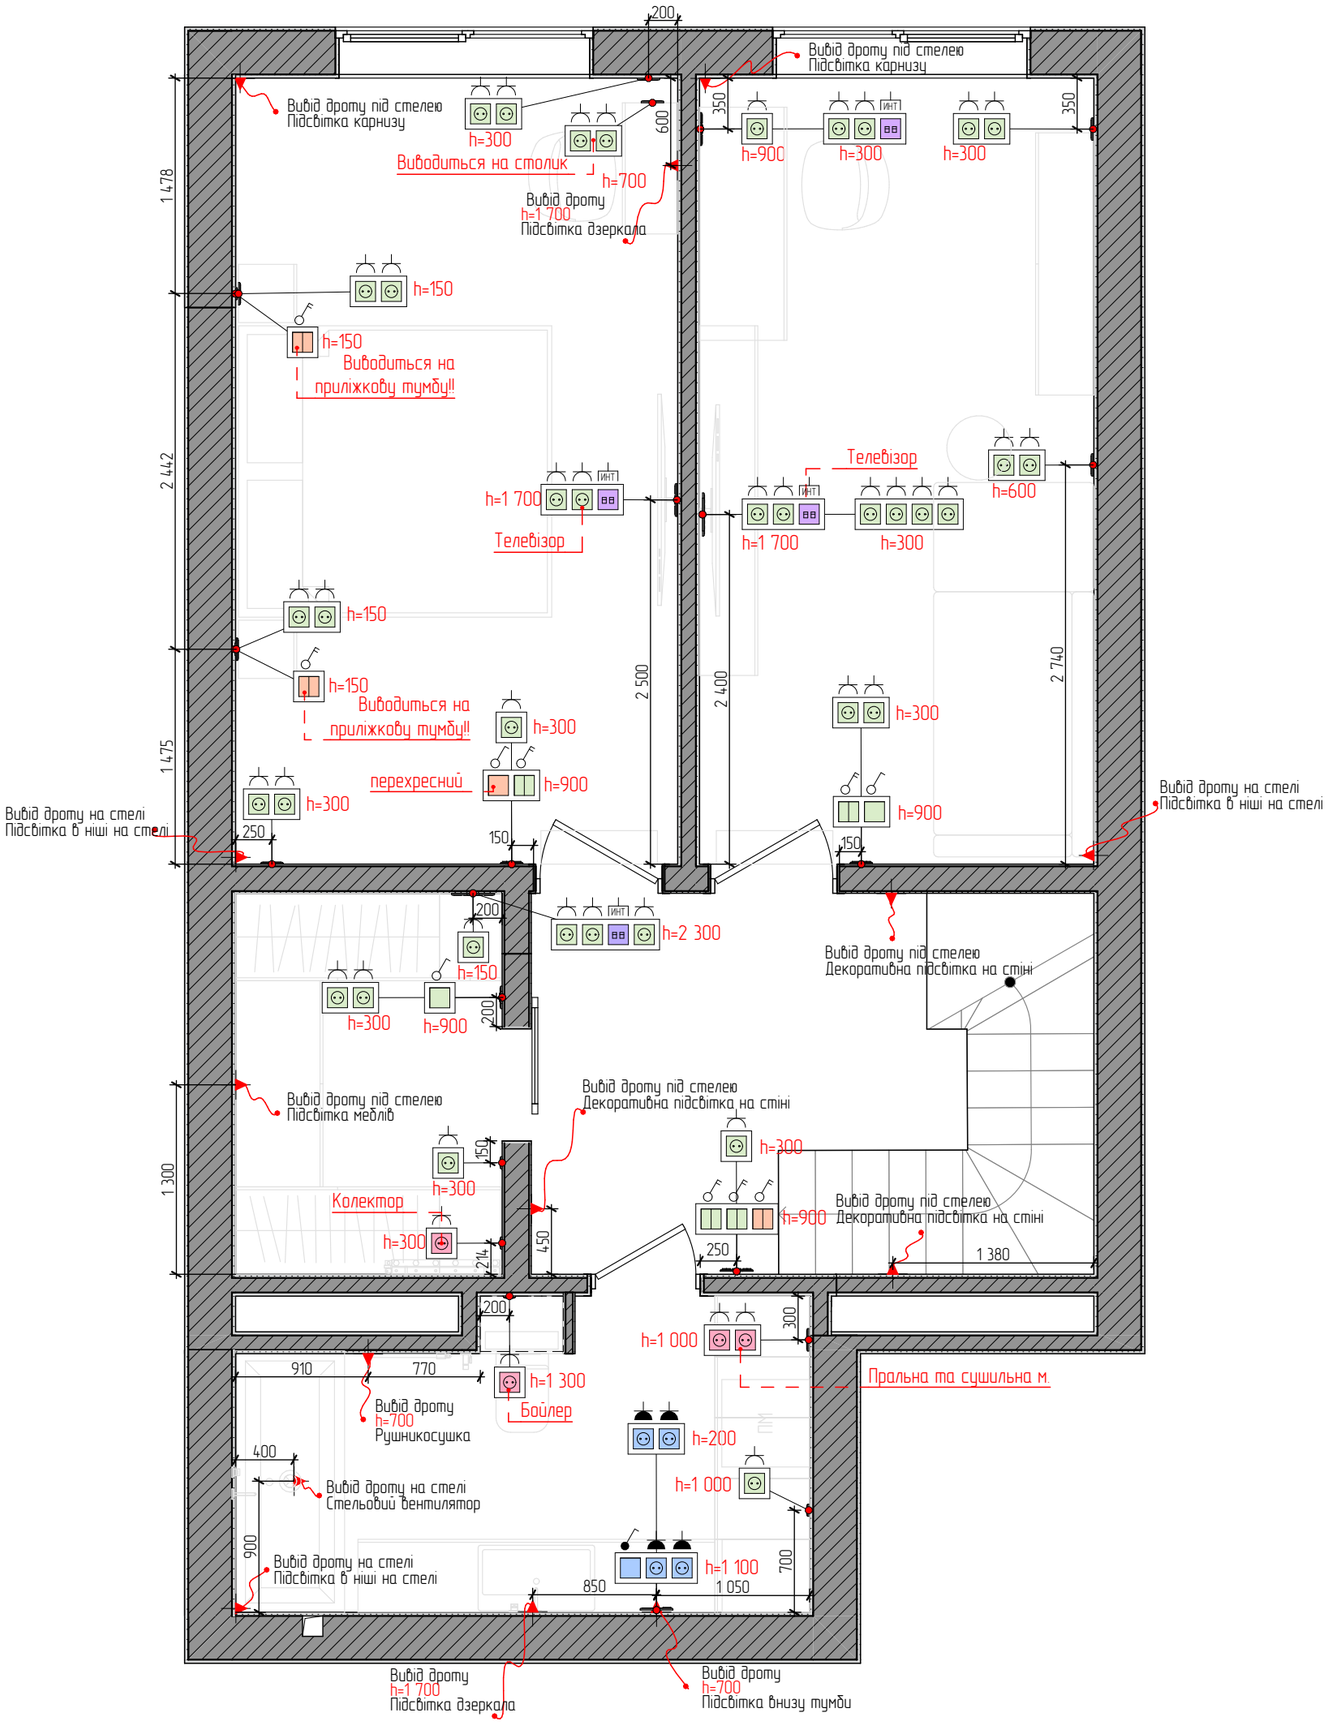

Специфікація рамок			
Тип рамки (блока)	Рамка орієнтація	К-сть	Примітки
Рамка х1			
	Горизонтальна	20	
Рамка х2			
	Горизонтальна	25	
Рамка х3			
	Горизонтальна	8	
Рамка х4			
	Горизонтальна	4	
Рамка х5			
	Горизонтальна	1	

Умовні позначення:

- – електрощит
- – майстер-вимикач
- – прохідний вимикач одноклавішний
- – прохідний вимикач двоклавішний
- – вимикач одноклавішний
- – вимикач двоклавішний
- – вимикач двоклавішний вологостійкий
- – вимикач одноклавішний вологостійкий
- – розетка
- – розетка із заземленням
- – розетка вологостійка
- – розетка мережева
- – вивід електричного живлення

Примітки:

1. Усі розміри вказані у мм від штукатурки;
2. Усі висотні дані від рівня чистової підлоги;
3. Усі плани електрики розглядати паралельно;
4. Прив'язки подано до центру вимикача, блока;
5. Блоки розташовані горизонтально, якщо не вказано інше!
6. Трансформатори від LED стрічок винести у електричний щит
7. Місце виводу електричного живлення для рушникосушки, а також розетки для бойлера уточнити згідно з характеристиками вибраного обладнання;

IHOR SAYEVICH
interior designer

м. Львів, вул. Трускавецька ЖК Парус Smart	Розділ	Аркуш	Аркушів
План розташування електрофурнітури. Поверх 2	РП-ТК	25	55

Ihor Sayevich Designer @ihor_sayevich_designer +380 97 585 91 01

Специфікація вимикачів та розеток

№	Найменування рамки	Тип рамки (блока)	2D зображення	Клас захисту (IP)	Рамка 1	Рамка 2	Рамка 3	Рамка 4	Виробник	Колір	К-сть	Примітки
1	Рамка х1 для горизонтального монтажу	Рамка х1		IP20	Домофон	–	–	–	Shneider/Asfora	Білий	1	
2	Рамка х2 для горизонтального монтажу	Рамка х2		IP20	Вимикач 1 клавішний	Вимикач 2 клавішний	–	–	Shneider/Asfora	Білий	1	
3	Рамка х1 для горизонтального монтажу	Рамка х1		IP20	Розетка 220V	–	–	–	Shneider/Asfora	Білий	1	
4	Рамка х2 для горизонтального монтажу	Рамка х2		IP44	Вимикач 1 клавішний	Розетка 220V	–	–	Shneider/Asfora	Білий	1	
5	Рамка х1 для горизонтального монтажу	Рамка х1		IP20	Вимикач 1 клавішний	–	–	–	Shneider/Asfora	Білий	1	
6	Рамка х4 для горизонтального та вертикального монтажу	Рамка х4		IP20	Розетка 220V	Розетка 220V	Розетка мережева	Розетка 220V	Shneider/Asfora	Білий	1	
7	Рамка х1 для горизонтального монтажу	Рамка х1		IP20	Розетка 220V	–	–	–	Shneider/Asfora	Білий	1	
8	Рамка х2 для горизонтального монтажу	Рамка х2		IP20	Розетка 220V	Розетка 220V	–	–	Shneider/Asfora	Білий	1	
9	Рамка х3 для горизонтального та вертикального монтажу	Рамка х3		IP20	Розетка 220V	Розетка 220V	Розетка 220V	–	Shneider/Asfora	Білий	1	
10	Рамка х2 для горизонтального монтажу	Рамка х2		IP20	Вимикач 1 клавішний	Вимикач 2 клавішний прохідний з 2 місць	–	–	Shneider/Asfora	Білий	1	
11	Рамка х1 для горизонтального монтажу	Рамка х1		IP20	Вимикач 2 клавішний	–	–	–	Shneider/Asfora	Білий	1	
12	Рамка х3 для горизонтального монтажу	Рамка х3		IP20	Вимикач 2 клавішний	Вимикач 2 клавішний	Вимикач 1 клавішний	–	Shneider/Asfora	Білий	1	
13	Рамка х2 для горизонтального та вертикального монтажу	Рамка х2		IP20	Розетка 220V	Розетка 220V	–	–	Shneider/Asfora	Білий	1	
14	Рамка х2 для горизонтального та вертикального монтажу	Рамка х2		IP20	Розетка 220V	Розетка 220V	–	–	Shneider/Asfora	Білий	1	
15	Рамка х2 для горизонтального та вертикального монтажу	Рамка х2		IP20	Розетка 220V	Розетка 220V	–	–	Shneider/Asfora	Білий	1	
16	Рамка х2 для горизонтального та вертикального монтажу	Рамка х2		IP20	Розетка 220V	Розетка 220V	–	–	Shneider/Asfora	Антрацит	1	
17	Рамка х2 для горизонтального та вертикального монтажу	Рамка х2		IP20	Розетка 220V	Розетка 220V	–	–	Shneider/Asfora	Білий	1	
18	Рамка х1 для горизонтального та вертикального монтажу	Рамка х1		IP20	Розетка 220V	–	–	–	Shneider/Asfora	Білий	1	
19	Рамка х2 для горизонтального та вертикального монтажу	Рамка х2		IP20	Розетка 220V	Розетка 220V	–	–	Shneider/Asfora	Білий	1	
20	Рамка х2 для горизонтального та вертикального монтажу	Рамка х2		IP20	Розетка 220V	Розетка 220V	–	–	Shneider/Asfora	Білий	1	
21	Рамка х1 для горизонтального та вертикального монтажу	Рамка х1		IP20	Розетка 220V	–	–	–	Shneider/Asfora	Білий	1	
22	Рамка х1 для горизонтального монтажу	Рамка х1		IP20	Вимикач 2 клавішний	–	–	–	Shneider/Asfora	Білий	1	
23	Рамка х1 для горизонтального монтажу	Рамка х1		IP20	Розетка 220V	–	–	–	Shneider/Asfora	Білий	1	


Специфікація вимикачів та розеток

24	Рамка х3 для горизонтального монтажу	Рамка х3		IP20	Розетка 220V	Розетка 220V	Розетка 220V 100-1000W	–	Shneider/Asfora	Білий	1	
25	Рамка х2 для горизонтального монтажу	Рамка х2		IP20	Розетка 220V	Розетка 220V	–	–	Shneider/Asfora	Білий	1	
26	Рамка х4 для горизонтального та вертикального монтажу	Рамка х4		IP20	Розетка 220V	Розетка 220V	Розетка 220V	Розетка мережева	Shneider/Asfora	Білий	1	
27	Рамка х5 для горизонтального та вертикального монтажу	Рамка х5		IP20	Розетка 220V	Розетка 220V	Розетка 220V	Розетка 220V	Shneider/Asfora	Білий	1	
28	Рамка х1 для горизонтального та вертикального монтажу	Рамка х1		IP20	Розетка 220V	–	–	–	Shneider/Asfora	Антрацит	1	
29	Рамка х3 для горизонтального монтажу	Рамка х3		IP20	Вимикач 2 клавішний	Вимикач 2 клавішний	Вимикач 2 клавішний прохідний з 2 місць	–	Shneider/Asfora	Антрацит	1	
30	Рамка х2 для горизонтального та вертикального монтажу	Рамка х2		IP20	Розетка 220V	Розетка 220V	–	–	Shneider/Asfora	Антрацит	1	
31	Рамка х1 для горизонтального та вертикального монтажу	Рамка х1		IP20	Розетка 220V	–	–	–	Shneider/Asfora	Антрацит	1	
32	Рамка х3 для горизонтального монтажу	Рамка х3		IP44	Вимикач 1 клавішний	Розетка 220V	Розетка 220V	–	Shneider/Asfora	Антрацит	1	
33	Рамка х2 для горизонтального монтажу	Рамка х2		IP44	Розетка 220V	Розетка 220V	–	–	Shneider/Asfora	Антрацит	1	
34	Рамка х1 для горизонтального та вертикального монтажу	Рамка х1		IP20	Розетка 220V	–	–	–	Shneider/Asfora	Антрацит	1	
35	Рамка х1 для горизонтального та вертикального монтажу	Рамка х1		IP20	Розетка 220V	–	–	–	Shneider/Asfora	Антрацит	1	
36	Рамка х1 для горизонтального та вертикального монтажу	Рамка х1		IP20	Розетка 220V	–	–	–	Shneider/Asfora	Антрацит	1	
37	Рамка х1 для горизонтального монтажу	Рамка х1		IP20	Вимикач 1 клавішний	–	–	–	Shneider/Asfora	Антрацит	1	
38	Рамка х2 для горизонтального та вертикального монтажу	Рамка х2		IP20	Розетка 220V	Розетка 220V	–	–	Shneider/Asfora	Антрацит	1	
39	Рамка х1 для горизонтального та вертикального монтажу	Рамка х1		IP20	Розетка 220V	–	–	–	Shneider/Asfora	Антрацит	1	
40	Рамка х4 для горизонтального та вертикального монтажу	Рамка х4		IP20	Розетка 220V	Розетка 220V	Розетка мережева	Розетка 220V	Shneider/Asfora	Антрацит	1	
41	Рамка х2 для горизонтального монтажу	Рамка х2		IP20	Вимикач 1 клавішний (перемикач) перехресний	Вимикач 2 клавішний	–	–	Shneider/Asfora	Антрацит	1	
42	Рамка х1 для горизонтального та вертикального монтажу	Рамка х1		IP20	Розетка 220V	–	–	–	Shneider/Asfora	Антрацит	1	
43	Рамка х2 для горизонтального та вертикального монтажу	Рамка х2		IP20	Розетка 220V	Розетка 220V	–	–	Shneider/Asfora	Антрацит	1	
44	Рамка х1 для горизонтального монтажу	Рамка х1		IP20	Вимикач 2 клавішний прохідний з 3 місць	–	–	–	Shneider/Asfora	Антрацит	1	
45	Рамка х2 для горизонтального та вертикального монтажу	Рамка х2		IP20	Розетка 220V	Розетка 220V	–	–	Shneider/Asfora	Антрацит	1	
46	Рамка х1 для горизонтального монтажу	Рамка х1		IP20	Вимикач 2 клавішний прохідний з 3 місць	–	–	–	Shneider/Asfora	Антрацит	1	

Специфікація вимикачів та розеток

47	Рамка х2 для горизонтального та вертикального монтажу	Рамка х2		IP20	Розетка 220V	Розетка 220V	–	–	Shneider/Asfora	Антрацит	1	
48	Рамка х2 для горизонтального та вертикального монтажу	Рамка х2		IP20	Розетка 220V	Розетка 220V	–	–	Shneider/Asfora	Антрацит	1	
49	Рамка х2 для горизонтального та вертикального монтажу	Рамка х2		IP20	Розетка 220V	Розетка 220V	–	–	Shneider/Asfora	Антрацит	1	
50	Рамка х3 для горизонтального та вертикального монтажу	Рамка х3		IP20	Розетка 220V	Розетка 220V	Розетка мережева	–	Shneider/Asfora	Антрацит	1	
51	Рамка х2 для горизонтального монтажу	Рамка х2		IP20	Вимикач 2 клавішний	Вимикач 1 клавішний	–	–	Shneider/Asfora	Антрацит	1	
52	Рамка х2 для горизонтального та вертикального монтажу	Рамка х2		IP20	Розетка 220V	Розетка 220V	–	–	Shneider/Asfora	Антрацит	1	
53	Рамка х3 для горизонтального та вертикального монтажу	Рамка х3		IP20	Розетка 220V	Розетка 220V	Розетка мережева	–	Shneider/Asfora	Антрацит	1	
54	Рамка х4 для горизонтального та вертикального монтажу	Рамка х4		IP20	Розетка 220V	Розетка 220V	Розетка 220V	Розетка 220V	Shneider/Asfora	Антрацит	1	
55	Рамка х2 для горизонтального та вертикального монтажу	Рамка х2		IP20	Розетка 220V	Розетка 220V	–	–	Shneider/Asfora	Антрацит	1	
56	Рамка х2 для горизонтального та вертикального монтажу	Рамка х2		IP20	Розетка 220V	Розетка 220V	–	–	Shneider/Asfora	Антрацит	1	
57	Рамка х3 для горизонтального та вертикального монтажу	Рамка х3		IP20	Розетка 220V	Розетка 220V	Розетка мережева	–	Shneider/Asfora	Антрацит	1	
58	Рамка х1 для горизонтального та вертикального монтажу	Рамка х1		IP20	Розетка 220V	–	–	–	Shneider/Asfora	Антрацит	1	
											58	

План розташування освітлювальних приладів
М1:35

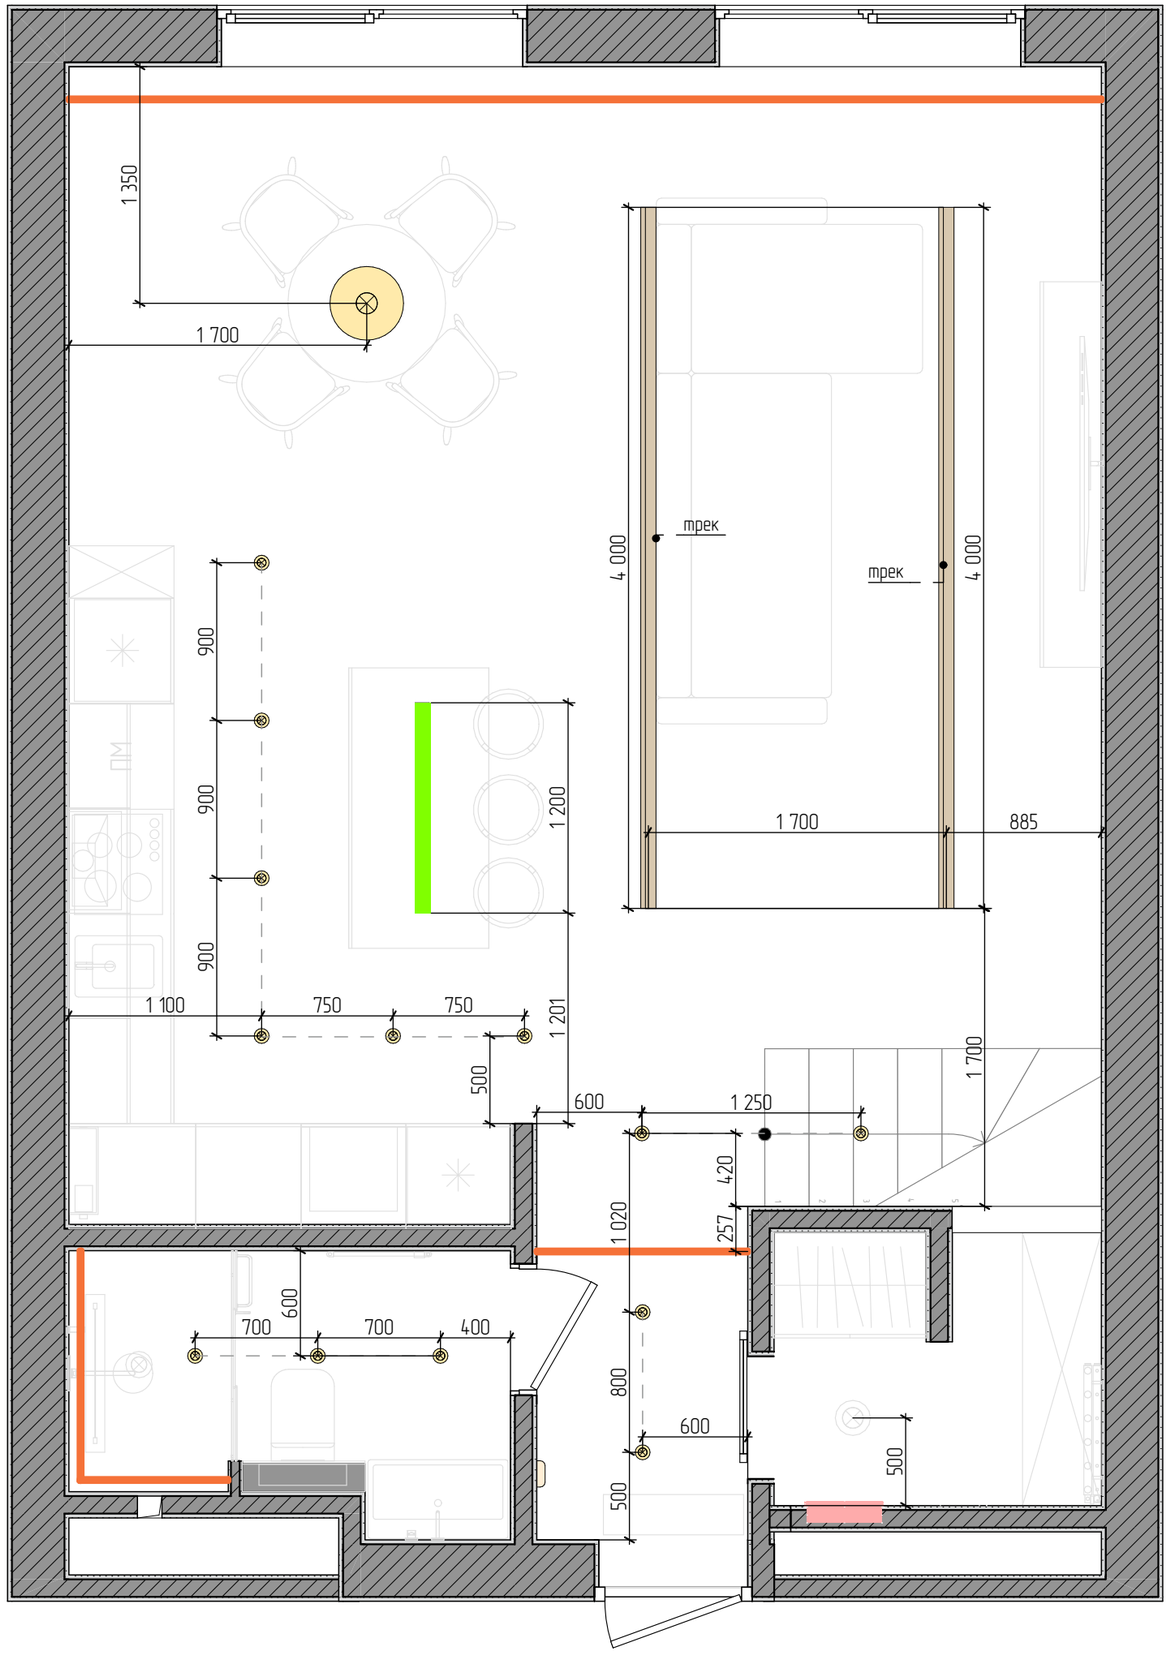

Умовні позначення:


- електрощит
- точковий світильник
- підвісний світильник
- люстра
- магнітний шинопровід трекової системи
- LED підсвітка 12V
- бра, настінний світильник
- група освітлення

Примітки:

1. Усі розміри вказані у мм від штукатурки;
2. Усі плани освітлення та розеток розглядати паралельно;
3. Трансформатори від LED стрічок винести у електричний щит;
4. Комплектуючі до шинопроводів закупити разом із шинопроводами;

IHOR SAYEVICH interior designer	м. Львів, вул. Трускавецька ЖК Парус Smart	Розділ	Аркуш	Аркушів
	План розташування освітлювальних приладів. Поверх 1	РП-ТК	29	55
	Ihor Sayevich Designer	@ihor_sayevich_designer	+380 97 585 91 01	

План розташування освітлювальних приладів. Поверх 2
М1:40

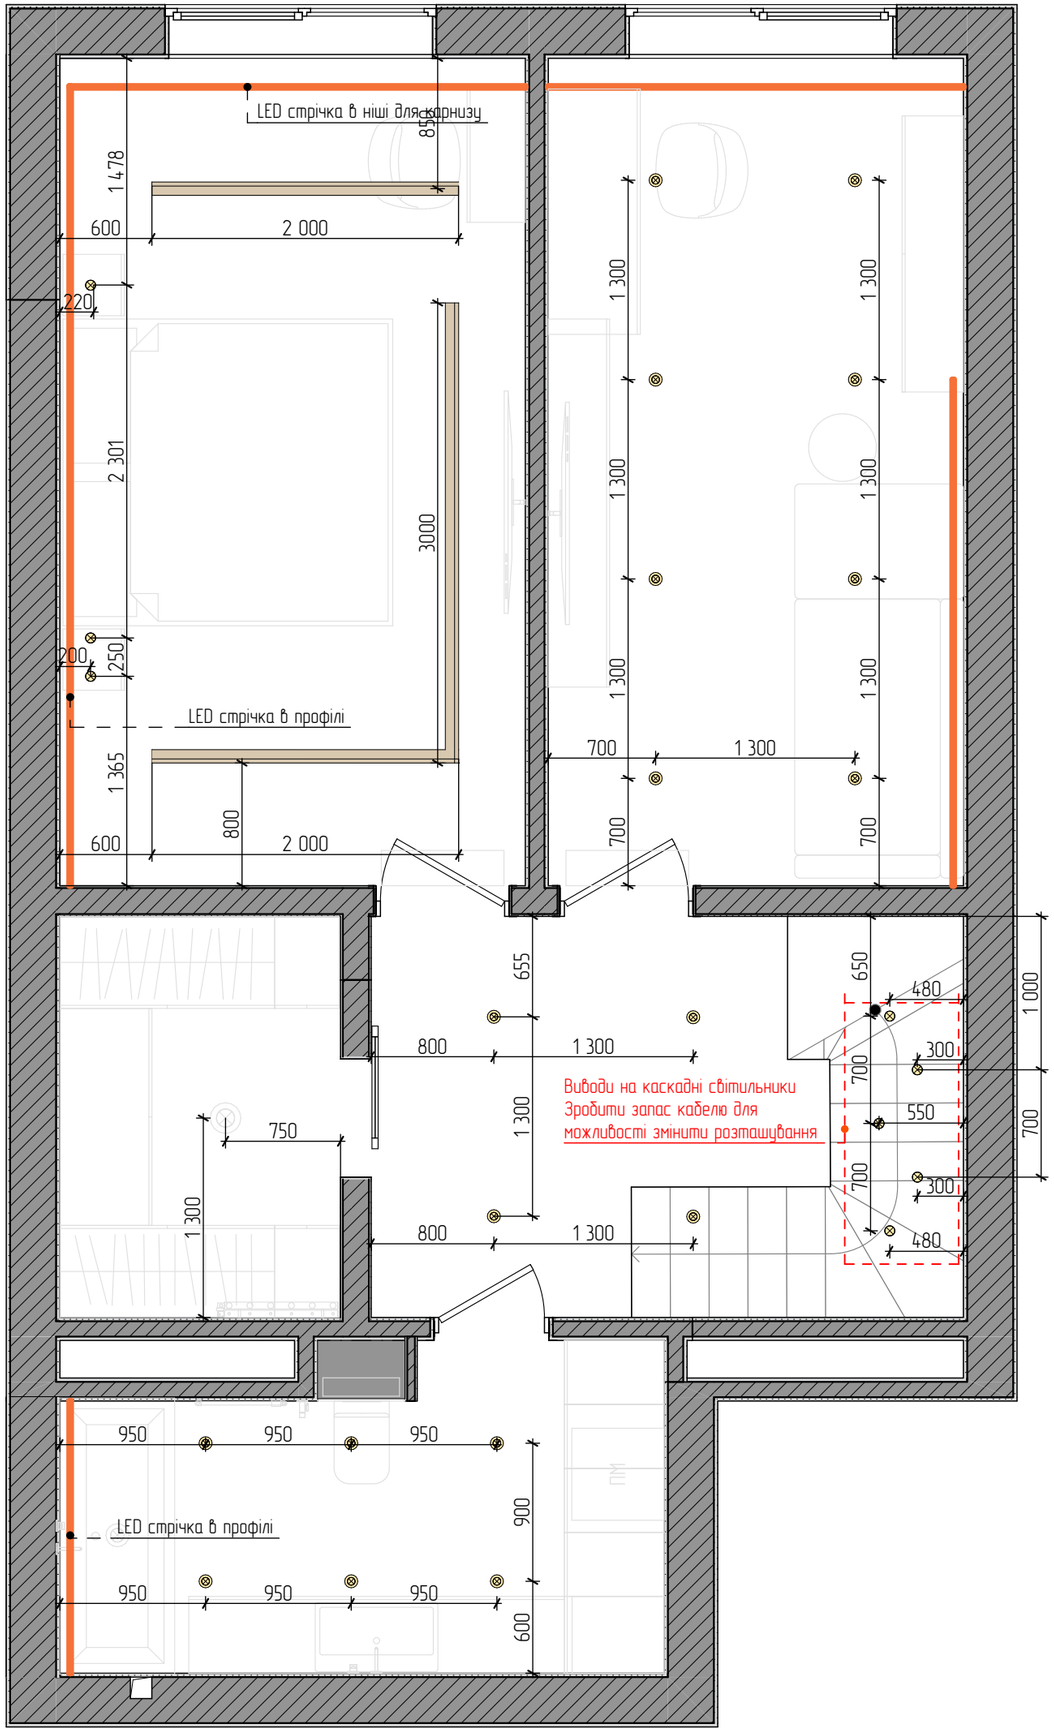

Умовні позначення:


- – електрощит
- – точковий світильник
- – підвісний світильник
- – люстра
- – магнітний шинопровід трекової системи
- – LED підсвітка 12V
- – бра, настінний світильник
- – група освітлення

Примітки:

1. Усі розміри вказані у мм від штукатурки;
2. Усі плани освітлення та розеток розглядати паралельно;
3. Трансформатори від LED стрічок винести у електричний щит;
4. Комплектуючі до шинопроводів закупити разом із шинопроводами;

IHOR SAYEVICH interior designer	м. Львів, вул. Трускавецька ЖК Парус Smart	Розділ	Аркуш	Аркушів
	План розташування освітлювальних приладів. Поверх 2	РП-ТК	30	55
	Ihor Sayevich Designer	@ihor_sayevich_designer	+380 97 585 91 01	

План управління освітленням
М1:35

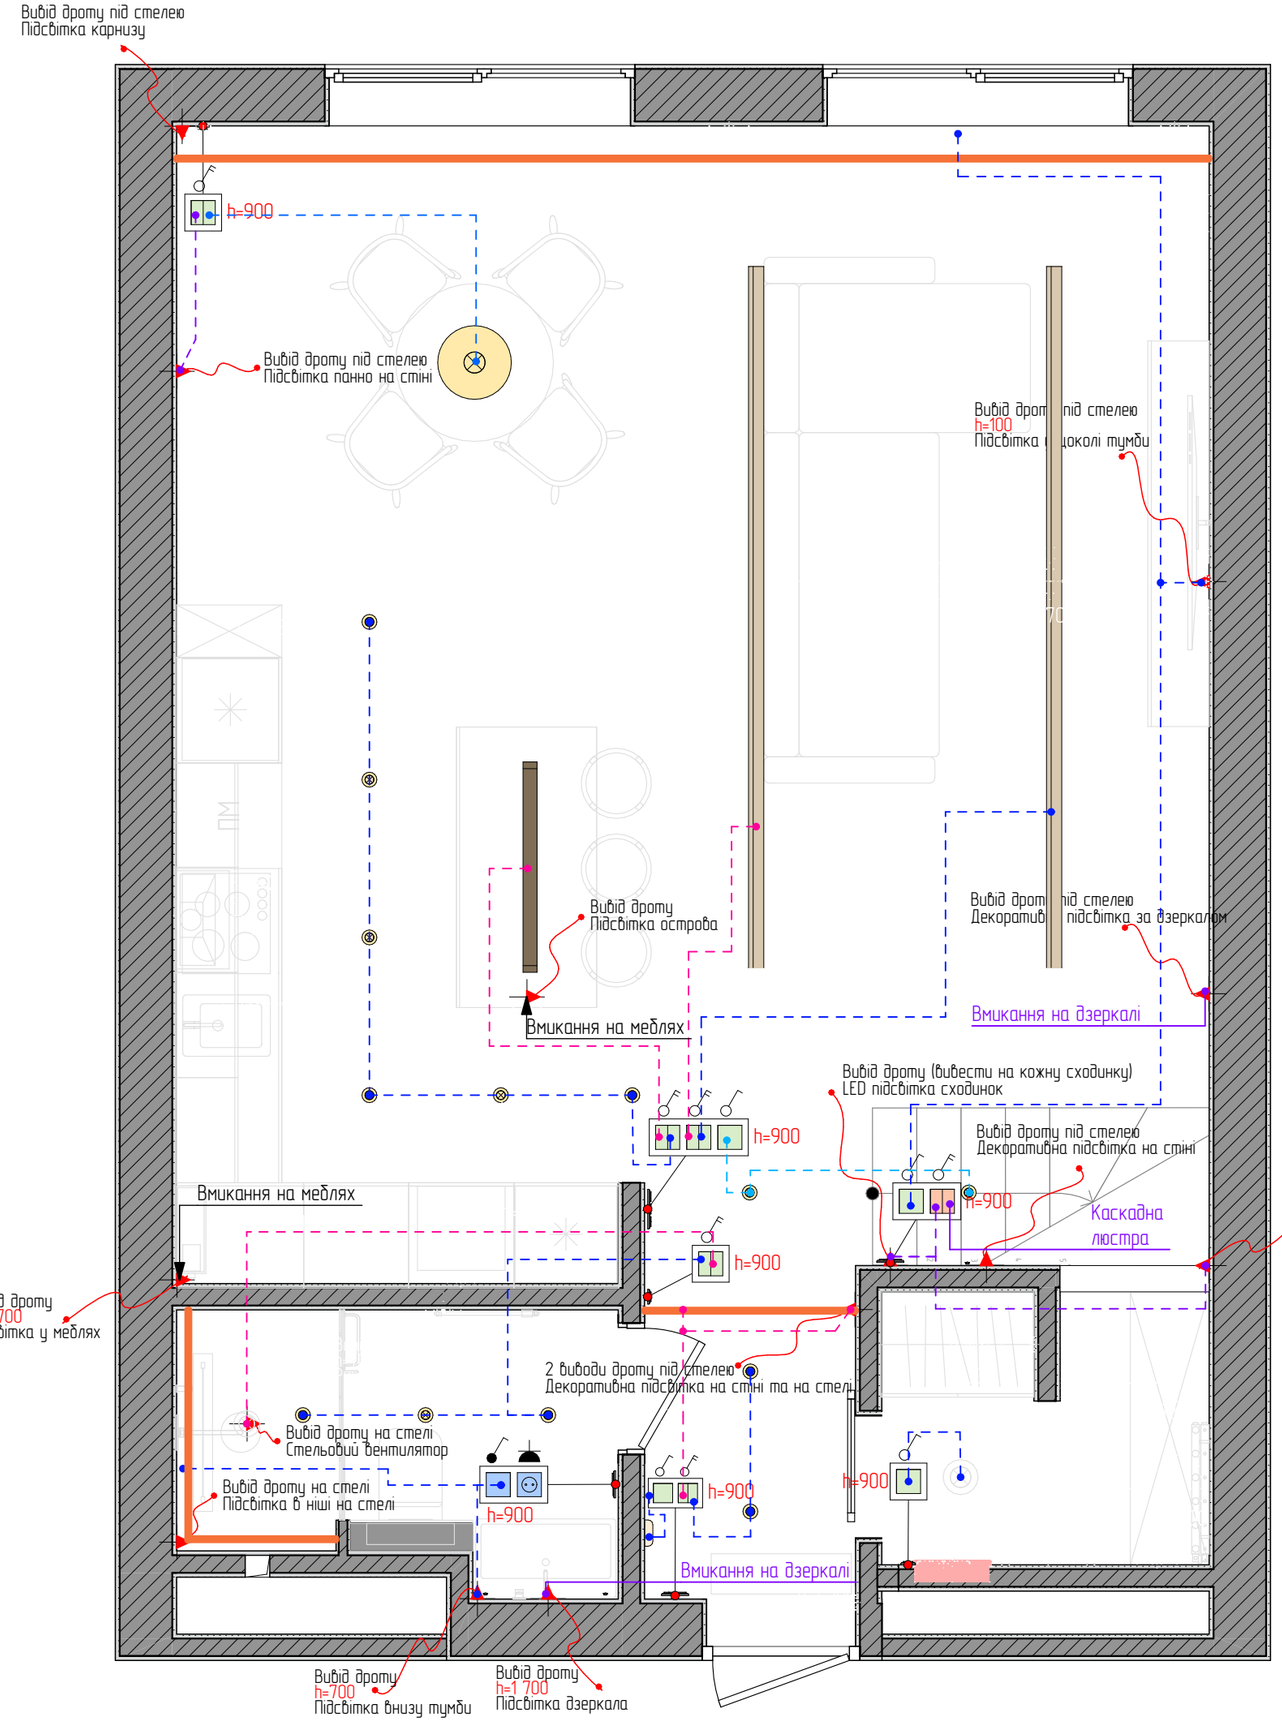

Умовні позначення:


- – електрощит
- h=0 – майстер-вимикач
- h=0 – прохідний вимикач одноклавішний
- h=0 – прохідний вимикач двоклавішний
- h=0 – вимикач одноклавішний
- h=0 – вимикач двоклавішний
- h=0 – вимикач двоклавішний вологостійкий
- h=0 – вимикач одноклавішний вологостійкий
- h=0 – розетка
- h=0 – розетка із заземленням
- h=0 – розетка вологостійка
- h=0 – розетка мережева
- – вивід електричного живлення
- – точковий світильник
- – підвісний світильник
- – люстра
- – магнітний шинопровід трекової системи
- – LED підсвітка 12V
- – бра, настінний світильник
- – група освітлення

Примітки:

1. Усі розміри вказані у мм від штукатурки;
2. Усі усі плани освітлення та розеток розглядати паралельно;
3. Трансформатори від LED стрічок винести у електричний щит;
4. Комплектуючі до шинопроводів закупити разом із шинопроводами;

iSD IHOR SAYEVICH interior designer	м. Львів, вул. Трускавецька ЖК Парус Smart	Розділ	Аркуш	Аркушів
	План управління освітленням. Поверх 1	РП-ТК	31	55
	Ihor Sayevich Designer	@ihor_sayevich_designer	+380 97 585 91 01	

План управління освітленням. Поверх 2

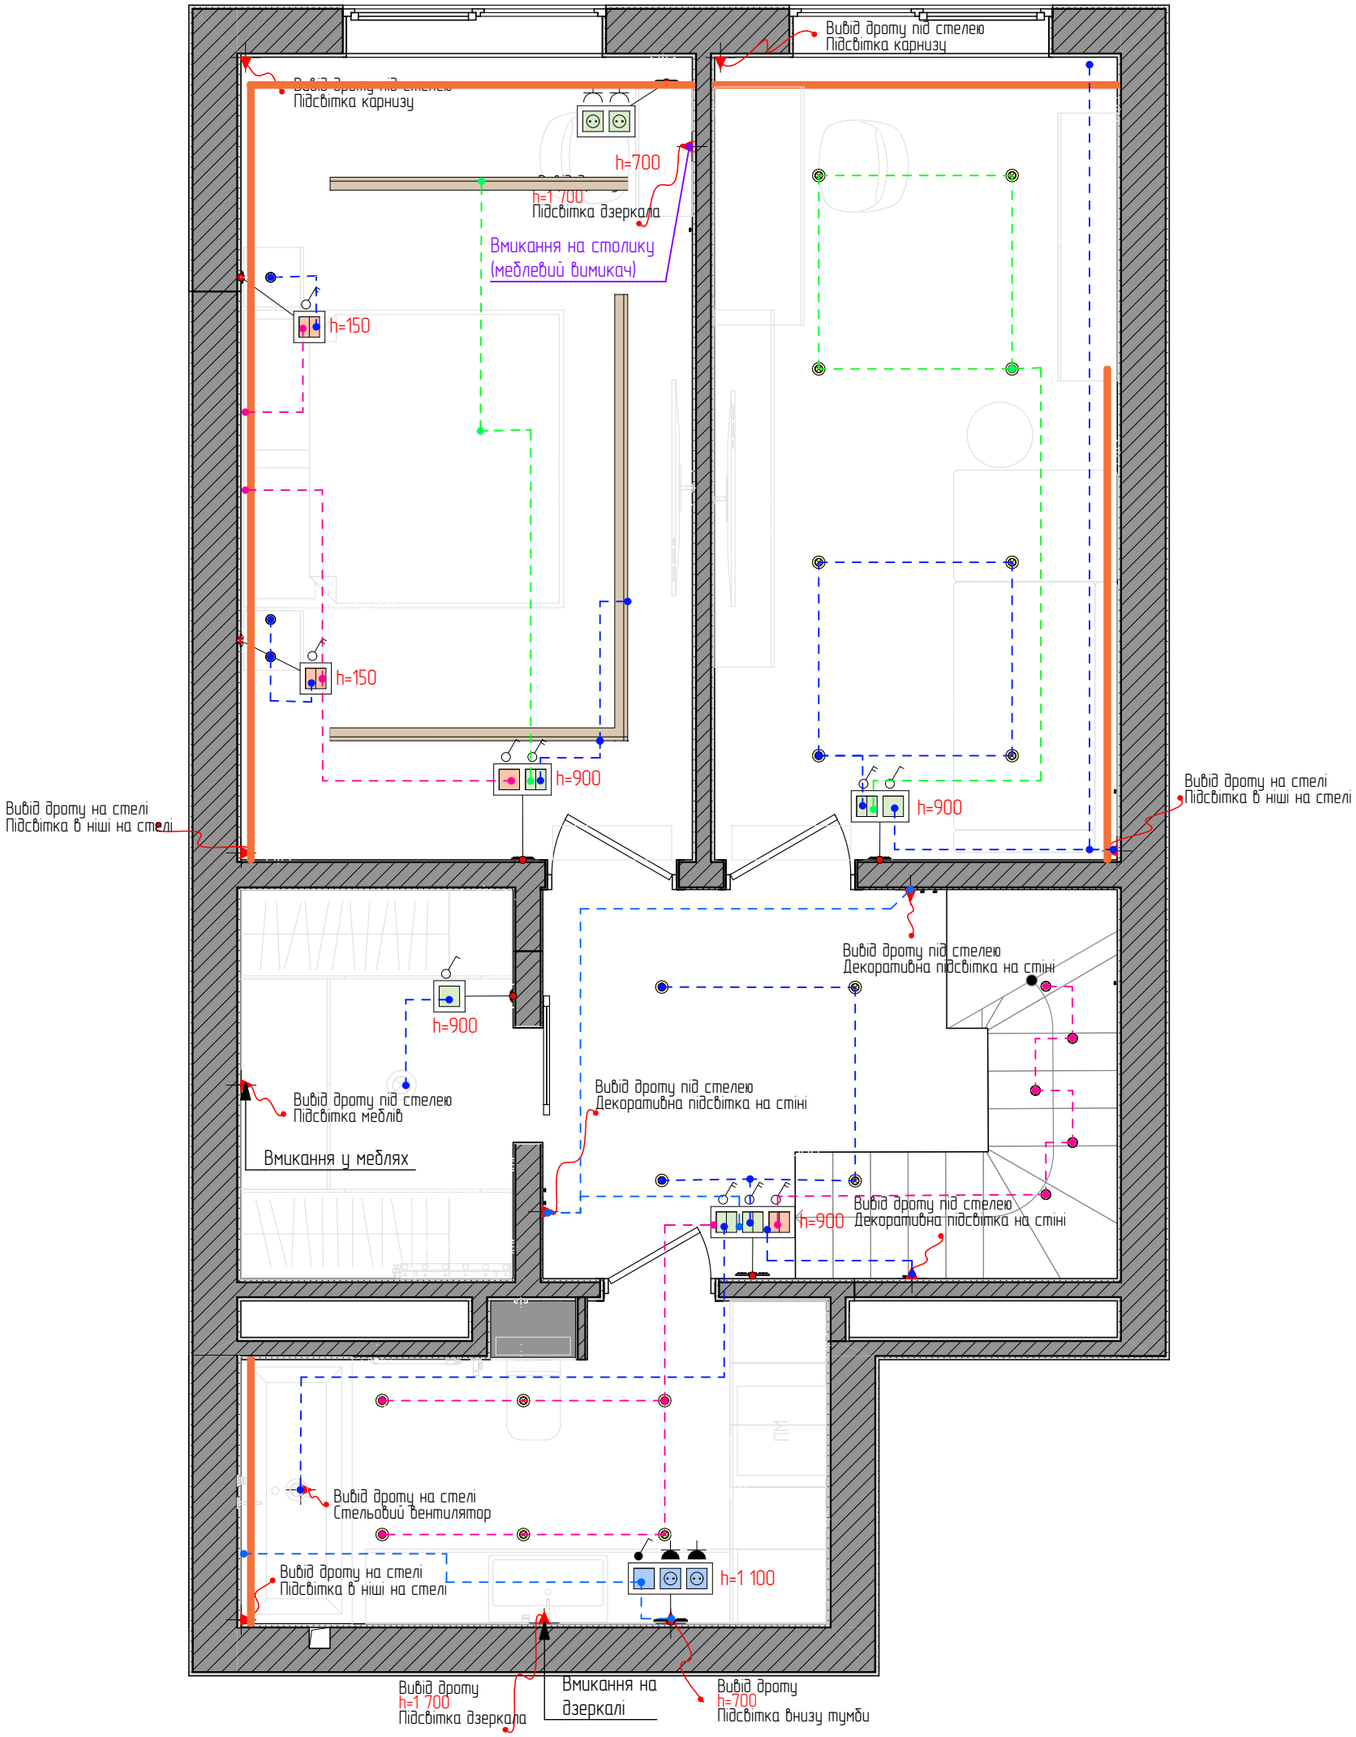

Умовні позначення:


- – електрощит
- h=0 – майстер-вимикач
- h=0 – прохідний вимикач одноклавішний
- h=0 – прохідний вимикач двоклавішний
- h=0 – вимикач одноклавішний
- h=0 – вимикач двоклавішний
- h=0 – вимикач двоклавішний вологостійкий
- h=0 – вимикач одноклавішний вологостійкий
- h=0 – розетка
- h=0 – розетка із заземленням
- h=0 – розетка вологостійка
- h=0 – розетка мережева
- – вивід електричного живлення
- – точковий світильник
- – підвісний світильник
- – люстра
- – магнітний шинопровід трекової системи
- – LED підсвітка 12V
- – бра, настінний світильник
- – група освітлення

Примітки:

1. Усі розміри вказані у мм від штукатурки;
2. Усі усі плани освітлення та розеток розглядати паралельно;
3. Трансформатори від LED стрічок винести у електричний щит;
4. Комплектуючі до шинопроводів закупити разом із шинопроводами;

iSD IHOR SAYEVICH interior designer	м. Львів, вул. Трускавецька ЖК Парус Smart	Розділ	Аркуш	Аркушів
	План управління освітленням. Поверх 2	РП-ТК	32	55
	Ihor Sayevich Designer	@ihor_sayevich_designer	+380 97 585 91 01	

План оздоблення стелі
М1:35

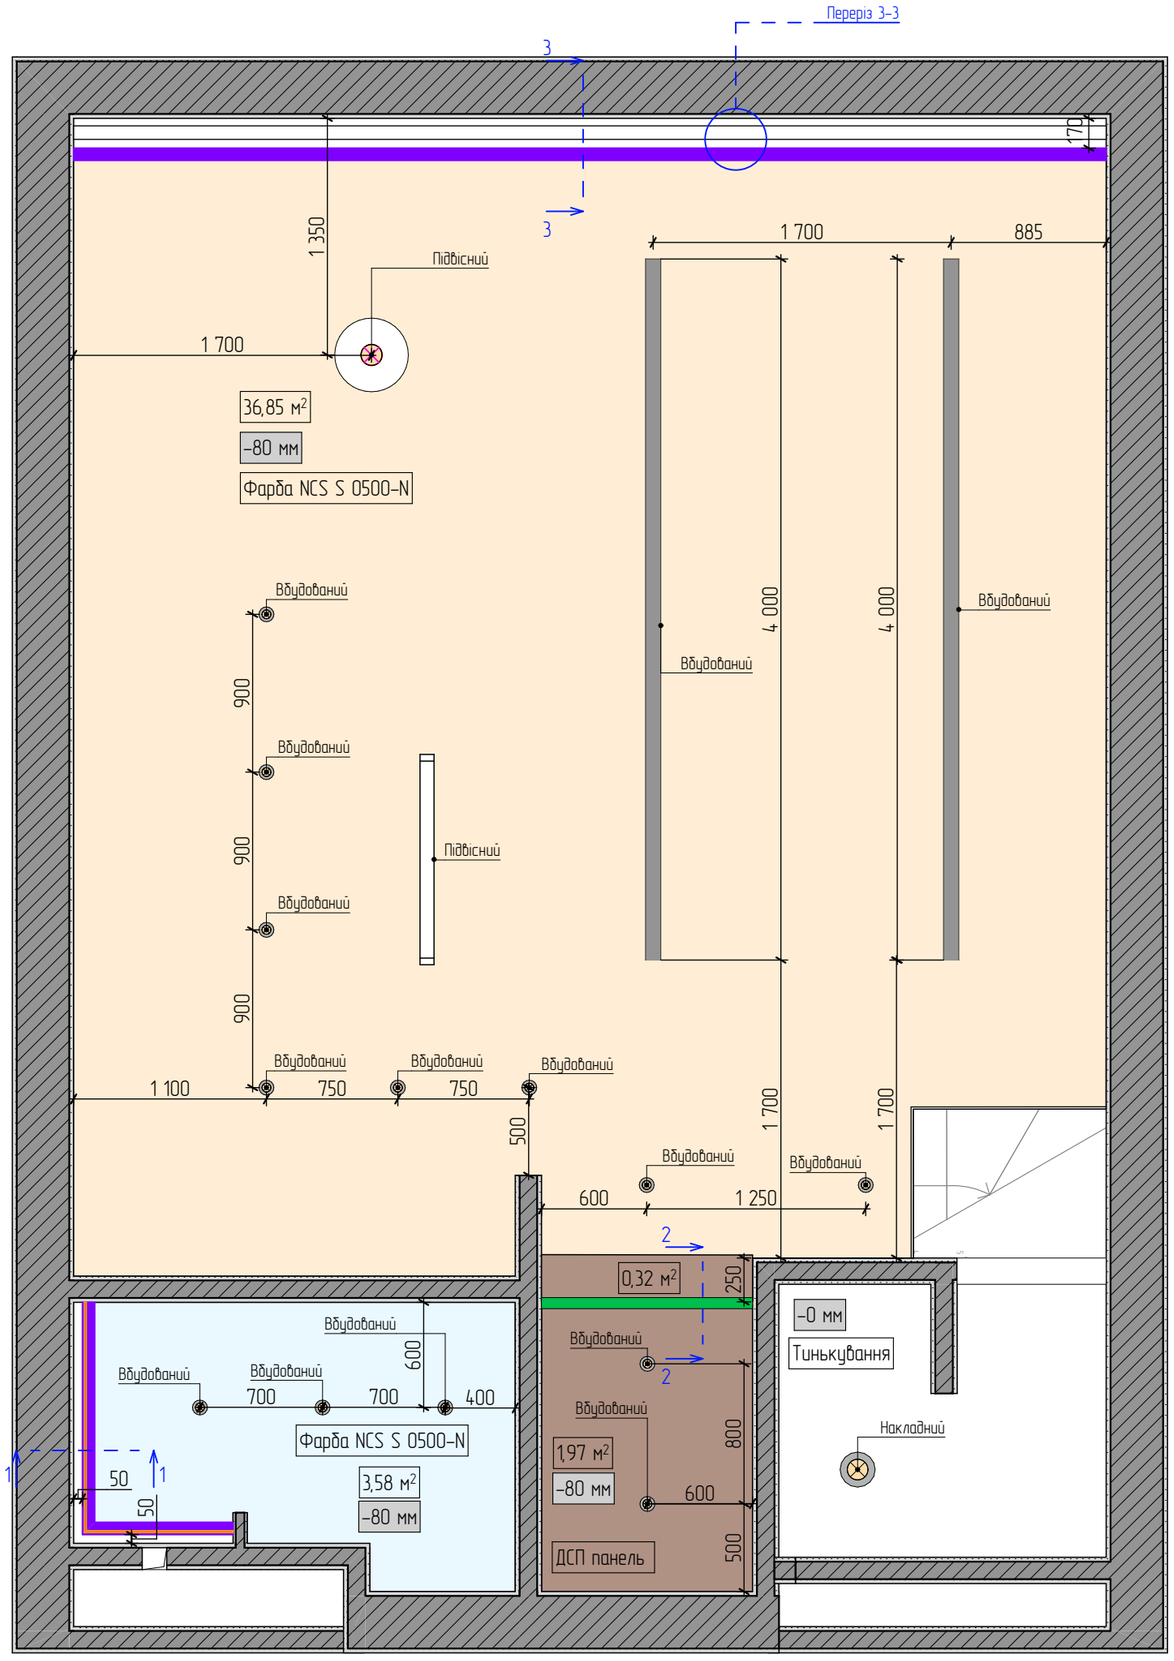

Умовні позначення:

- – натяжна стеля
- -80 мм – рівень опуску стелі
- – профіль тіньового шва для LED стрічки
- – профіль тіньового шва роздільний для LED стрічки (світлова лінія)
- – LED стрічка
- – карниз для штор
- – магнітний трек (вбудований)

І6 Відомість профілів для монтажу стель

Поз.	Відображення на плані	Ескіз	Довжина, мм.	Примітки
1			24 069	
2			1 204	

Відомість карнизів

Поз.	Відображення на плані	Ескіз	Довжина, мм.	Примітки
3			11 634	

Примітки:

1. Усі розміри вказані у мм;
2. Магнітні шинопроводи змонтувати на етапі монтажу стелі;
3. В місці розташування підвісних світильників передбачити закладну деталь;
4. Перерізи стелі дивитись на наступному аркуші
5. Можлива заміна на натяжну стелю! Вид оздоблення стелі обирає замовник після консультації спеціаліста!


Опуск стелі має становити максимально до 100 мм!

IHOR SAYEVICH
interior designer

м. Львів, вул. Трускавецька ЖК Парус Smart	Розділ	Аркуш	Аркушів
План оздоблення стель. Поверх 1	РП-ТК	33	55

Ihor Sayevich Designer @ihor_sayevich_designer +380 97 585 91 01

План оздоблення стелі. Поверх 2

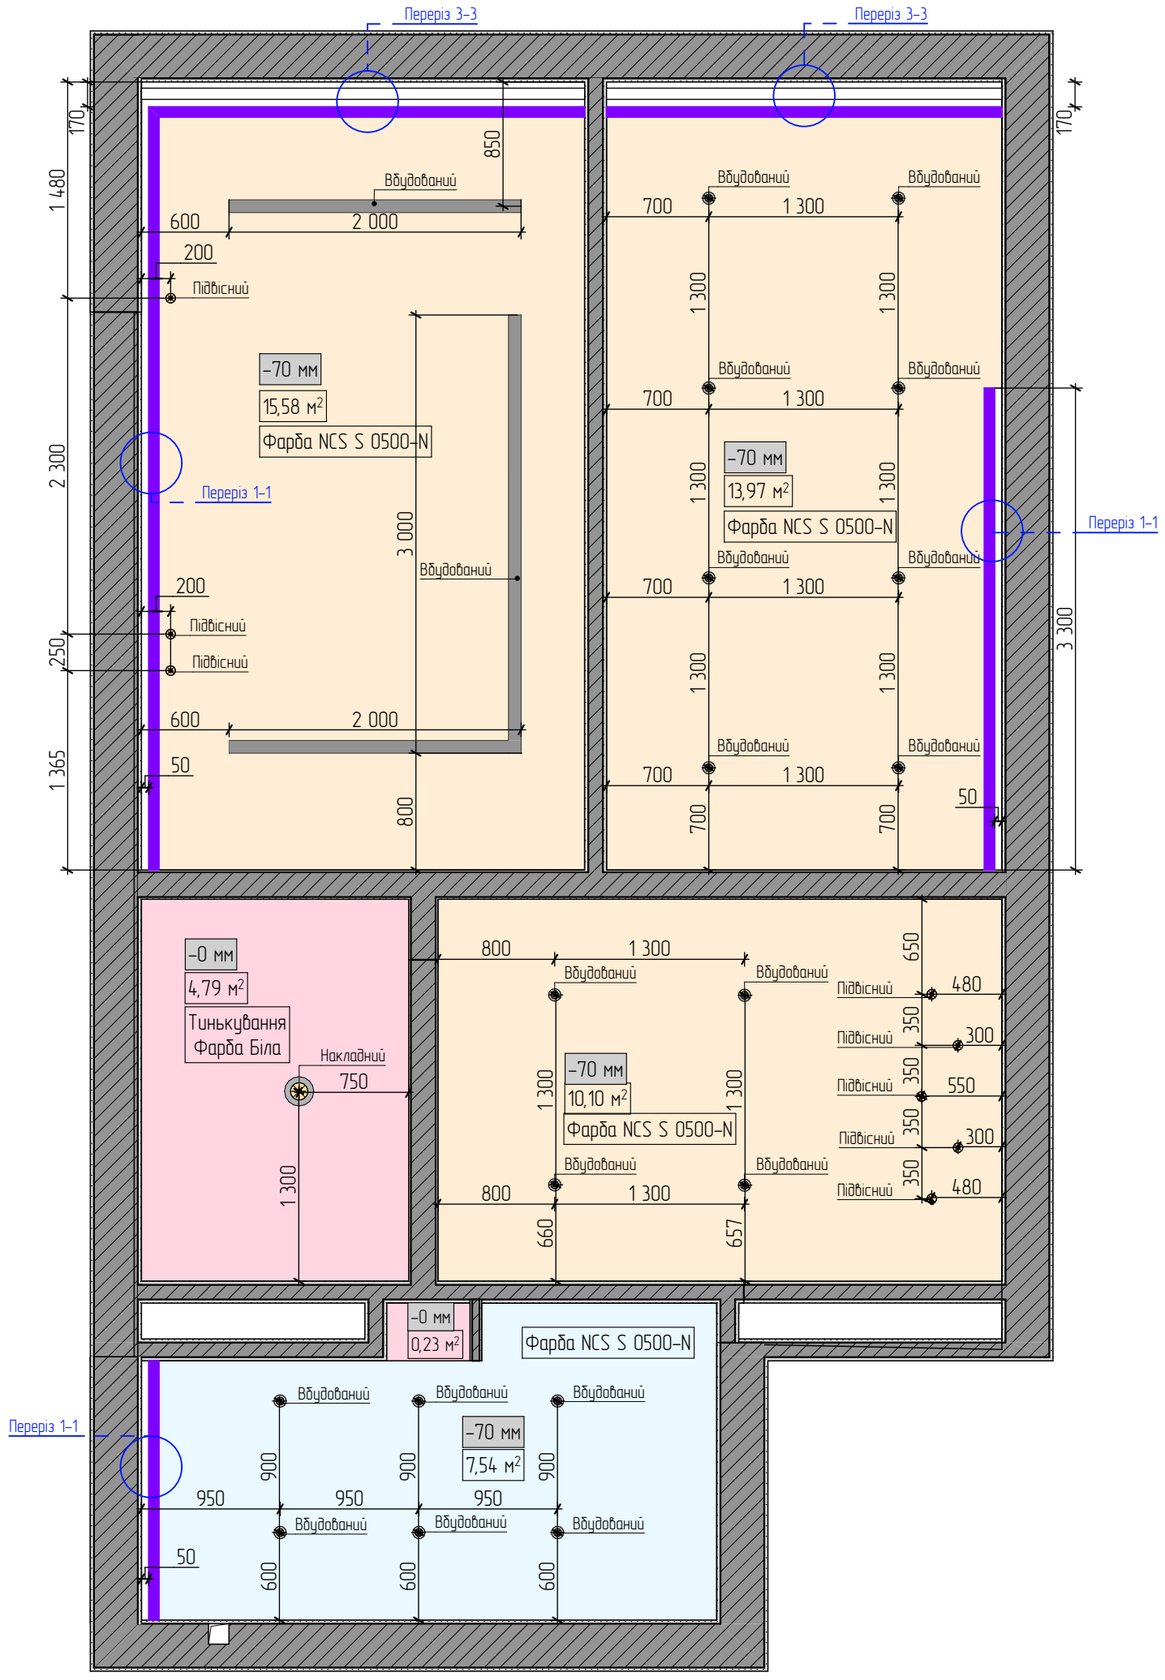

Умовні позначення:

- – натяжна стеля
- -80 мм – рівень опуску стелі
- – профіль тіньового шва для LED стрічки
- – профіль тіньового шва роздільний для LED стрічки (світлова лінія)
- – LED стрічка
- – карниз для штор
- – магнітний трек (вбудований)

І6 Відомість профілів для монтажу стель

Поз.	Відображення на плані	Ескіз	Довжина, мм.	Примітки
1			24 069	
2			1 204	

Відомість карнизів

Поз.	Відображення на плані	Ескіз	Довжина, мм.	Примітки
3			11 634	


Примітки:

1. Усі розміри вказані у мм;
2. Магнітні шинопроводи змонтувати на етапі монтажу стелі;
3. В місці розташування підвісних світильників передбачити закладну деталь;
4. Перерізи стелі дивитись на наступному аркуші
5. Можлива заміна на натяжну стелю! Вид оздоблення стелі обирає замовник після консультації спеціаліста!


Опуск стелі має становити максимально до 100 мм!

IHOR SAYEVICH interior designer	м. Львів, вул. Трускавецька ЖК Парус Smart	Розділ	Аркуш	Аркушів
	План оздоблення стель. Поверх 1	РП-ТК	34	55
	Ihor Sayevich Designer	@ihor_sayevich_designer	+380 97 585 91 01	


Переріз 1–1

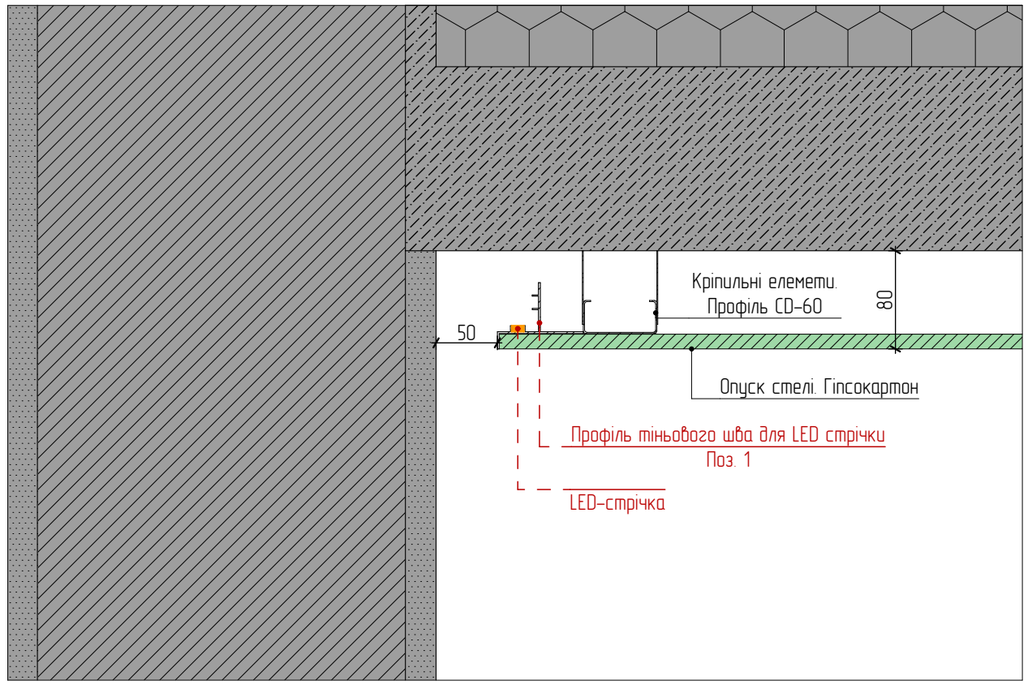


Переріз 3–3

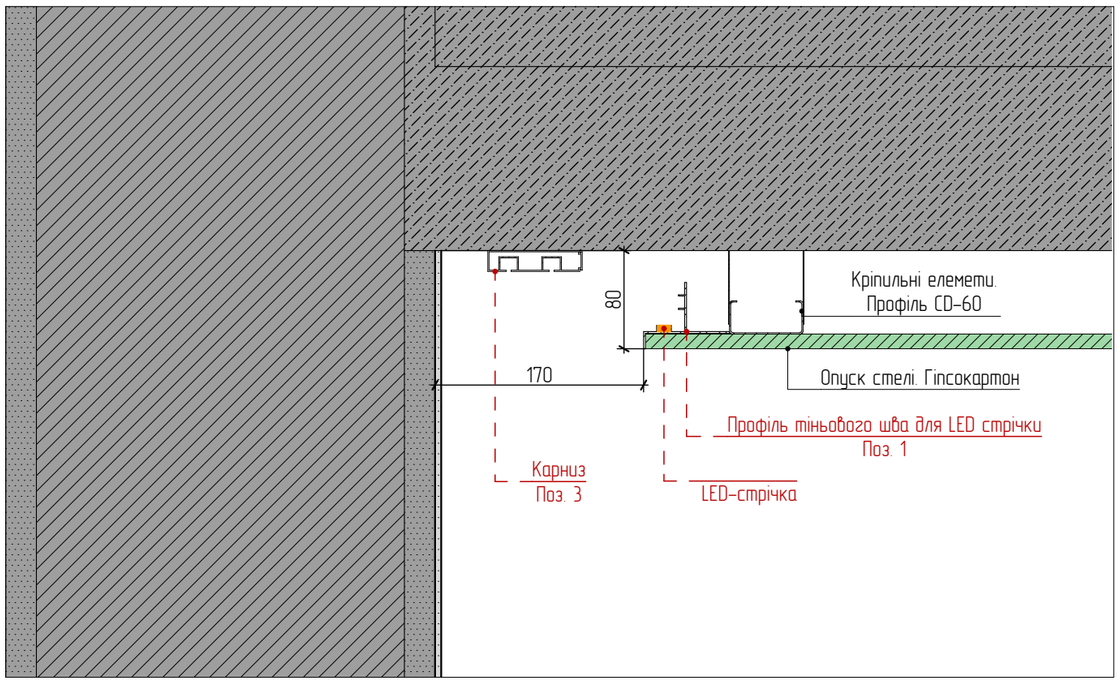

Універсальний профіль тіньового шва АПТШ 50 мм LED

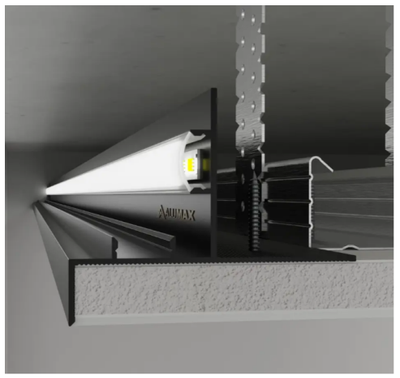


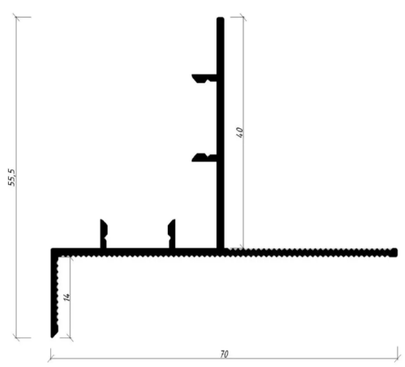


Поз.	Відображення на плані	Ескіз	Довжина, мм.
1			24 069
2			1 204

Профіль тіньового шва (роздільний) 15 мм с LED каналом



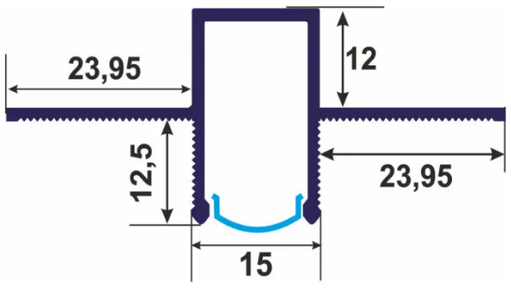


Переріз 2–2

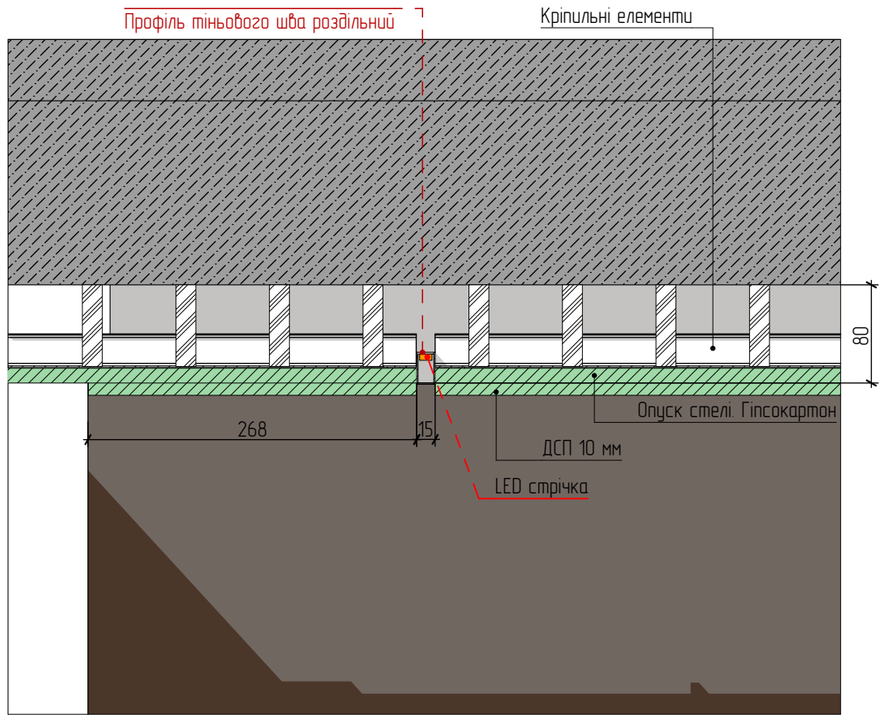

IHOR SAYEVICH interior designer	м. Львів, вул. Трускавецька ЖК Парус Smart	Розділ	Аркуш	Аркушів
	Перерізи стель	РП-ТК	35	55
	Ihor Sayevich Designer	@ihor_sayevich_designer	+380 97 585 91 01	

План оздоблення підлоги. Поверх 1

М1:35

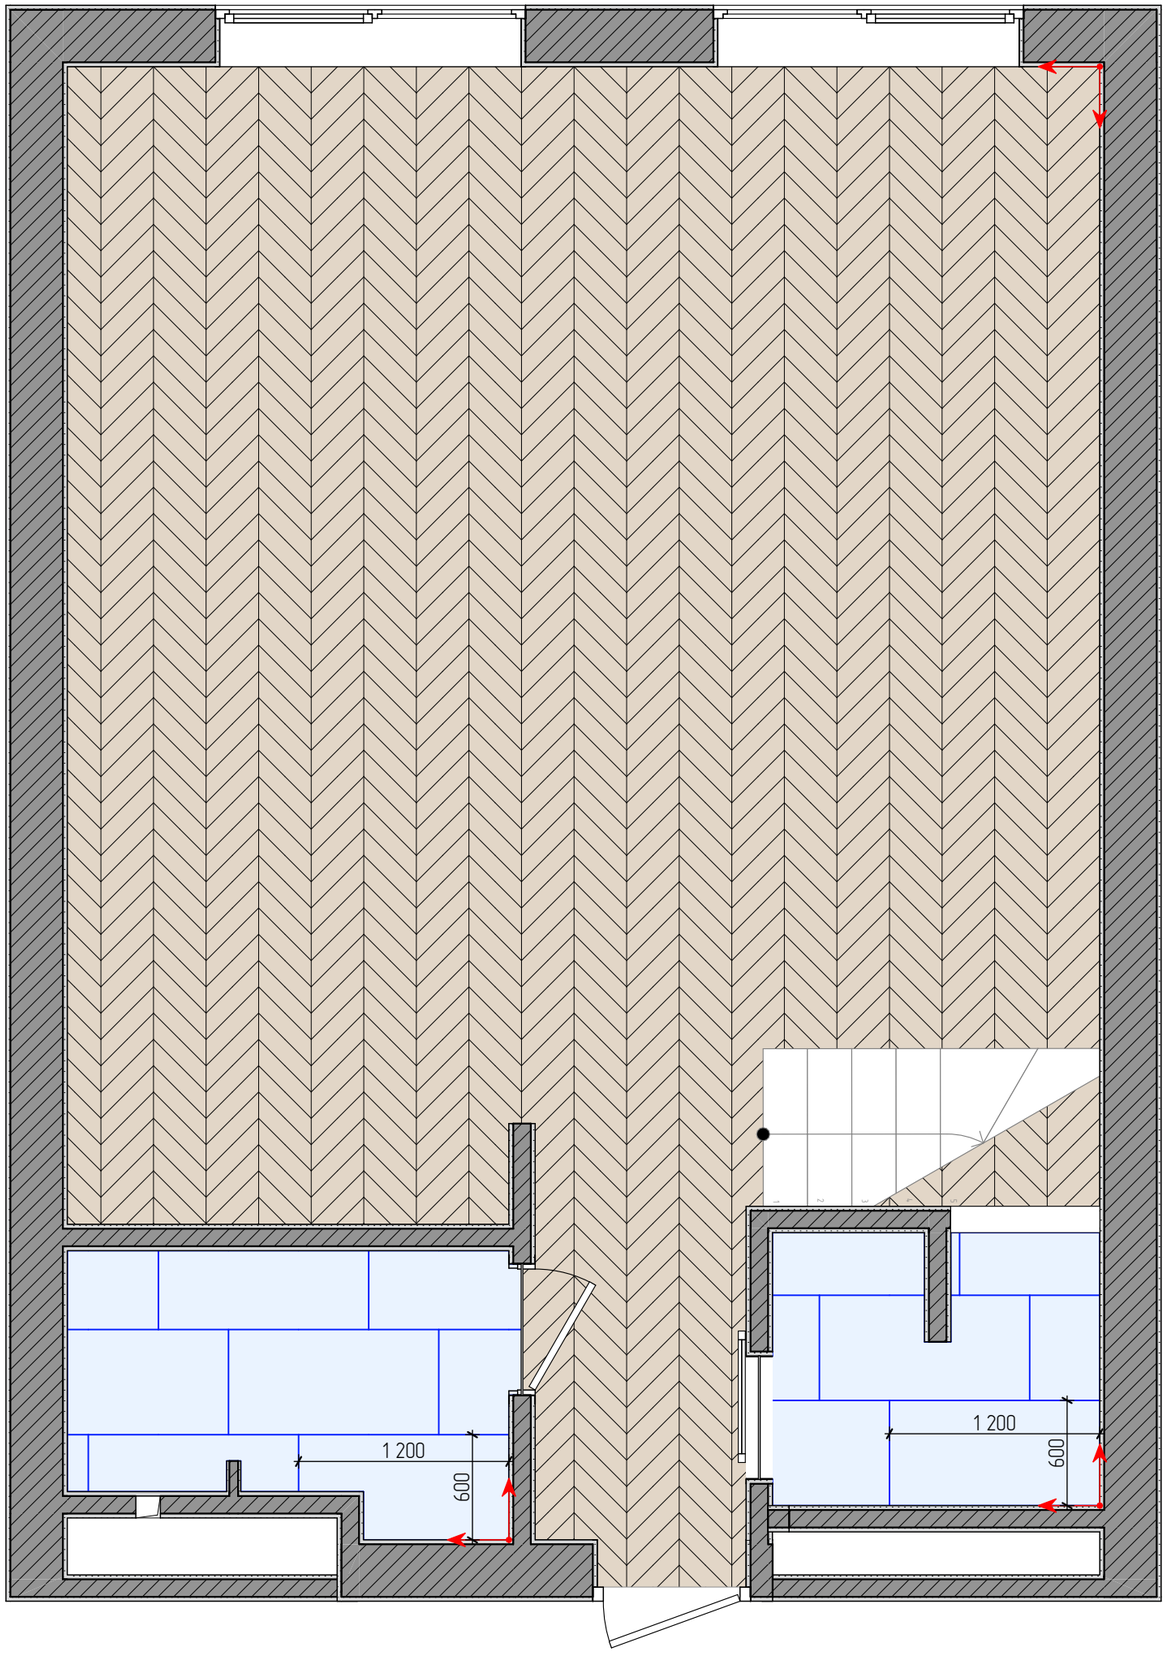

Умовні позначення:

– керамограніт

– Ламінат, французька ялинка ("шеврон")

– початок розкладки плитки

Площа підлогового покриття

№	Вигляд	Мат. Оздобле...	Найменування оздоблення	Площа, м. кв.
1		Керамограніт	Almera Ceramica (Spain) Ec.Candy Blanco 120x60	14,54
2		Ламінат	Поверх 1	41,13
3		Ламінат	Поверх 2	42,74

Примітки:


1. Усі розміри вказані у мм;
2. Стик підлогових покриттів влаштувати за допомогою силіконового стику;
3. Рівень підлог у всіх приміщеннях повинен бути однаковим;
4. Розкладку плитки здійснювати зі зміщенням на 1/3.

Розміри вказані для прорахунку основних будівельних та оздоблювальних матеріалів. Перед початком роботи і закупівлею матеріалів провести обміри на об'єкті!

Можлива заміна укладки ламінату на палубну зі зміщенням на 1/3 (2 поверх)!

IHOR SAYEVICH interior designer	м. Львів, вул. Трускавецька ЖК Парус Smart	Розділ	Аркуш	Аркушів
	План оздоблення підлоги. Поверх 1	РП-ТК	36	55
	Ihor Sayevich Designer @ihor_sayevich_designer +380 97 585 91 01			

План оздоблення підлоги. Поверх 2

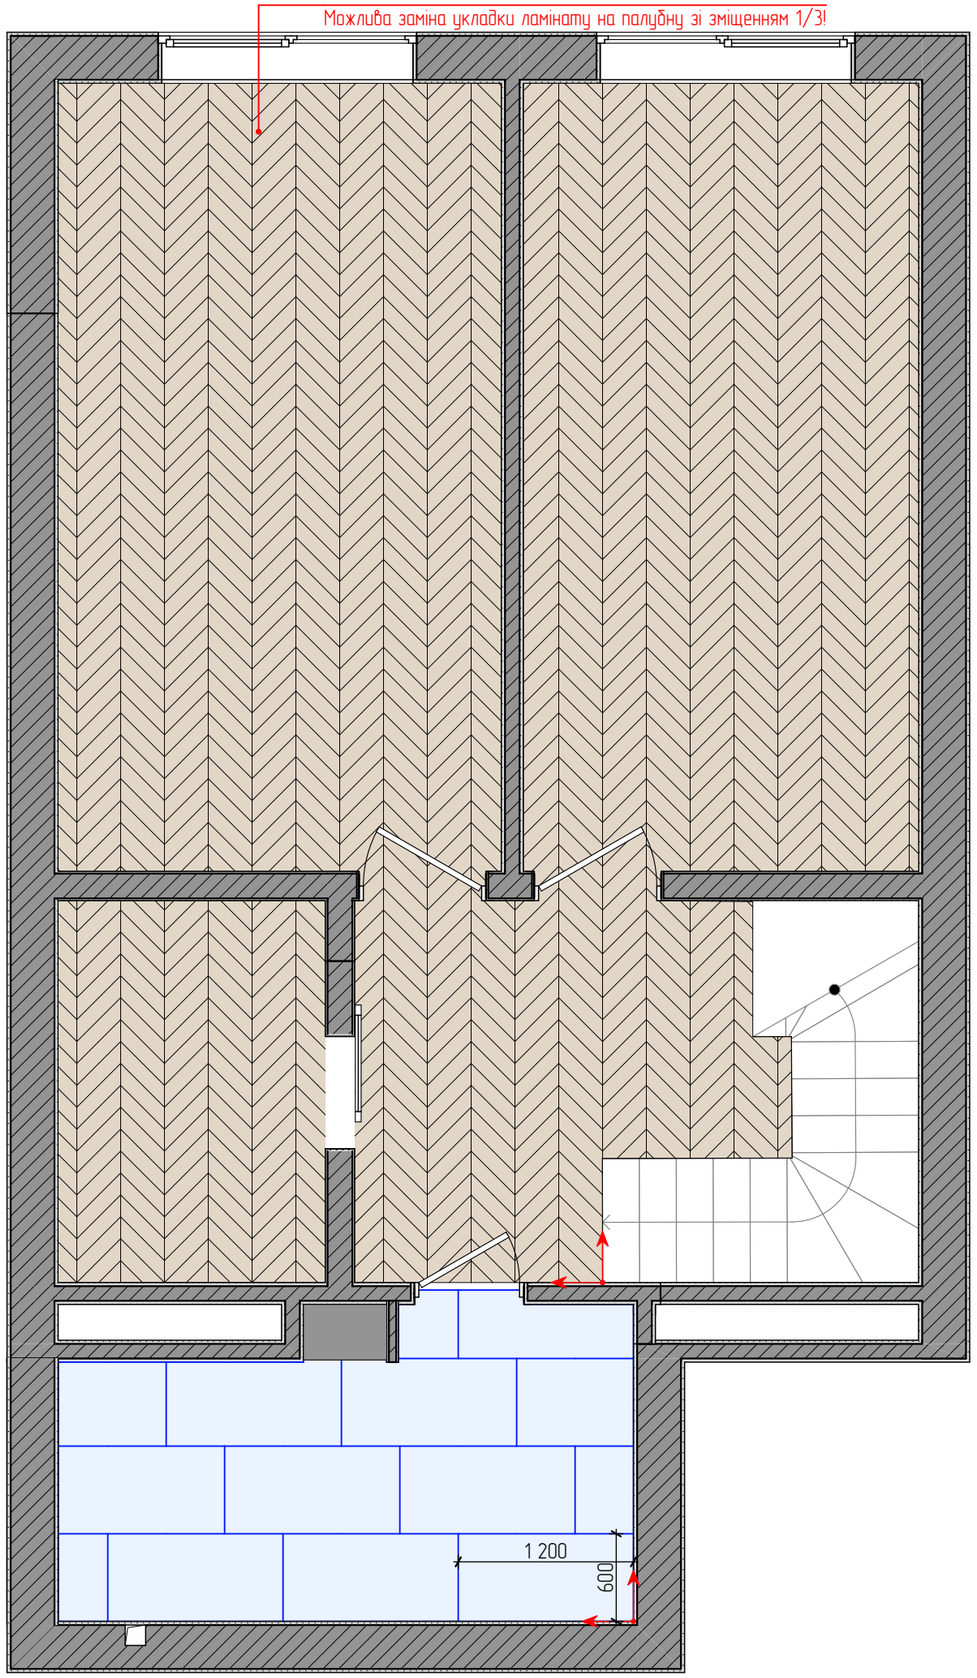

Умовні позначення:

– керамограніт

– Ламінат, французька ялинка ("шеврон")

– початок розкладки плитки

Площа підлогового покриття				
№	Вигляд	Мат. Оздоблє...	Найменування оздоблення	Площа, м. кв.
1		Керамограніт	Almera Ceramica (Spain) Ec.Candy Blanco 120x60	14,54
2		Ламінат	Поверх 1	41,13
3		Ламінат	Поверх 2	42,74

Примітки:


1. Усі розміри вказані у мм;
2. Стик підлогових покриттів влаштувати за допомогою силіконового стику;
3. Рівень підлог у всіх приміщеннях повинен бути однаковим;
4. Розкладку плитки здійснювати зі зміщенням на 1/3.

Розміри вказані для прорахунку основних будівельних та оздоблювальних матеріалів. Перед початком роботи і закупівлею матеріалів провести обміри на об'єкті!

Можлива заміна укладки ламінату на палубну зі зміщенням на 1/3 (2 поверх)!

iSD IHOR SAYEVICH interior designer	м. Львів, вул. Трускавецька ЖК Парус Smart	Розділ	Аркуш	Аркушів
	План оздоблення підлоги. Поверх 1	РП-ТК	37	55
	Ihor Sayevich Designer	@ihor_sayevich_designer	+380 97 585 91 01	

План відкривання дверей та влаштування плінтусів
М1:35

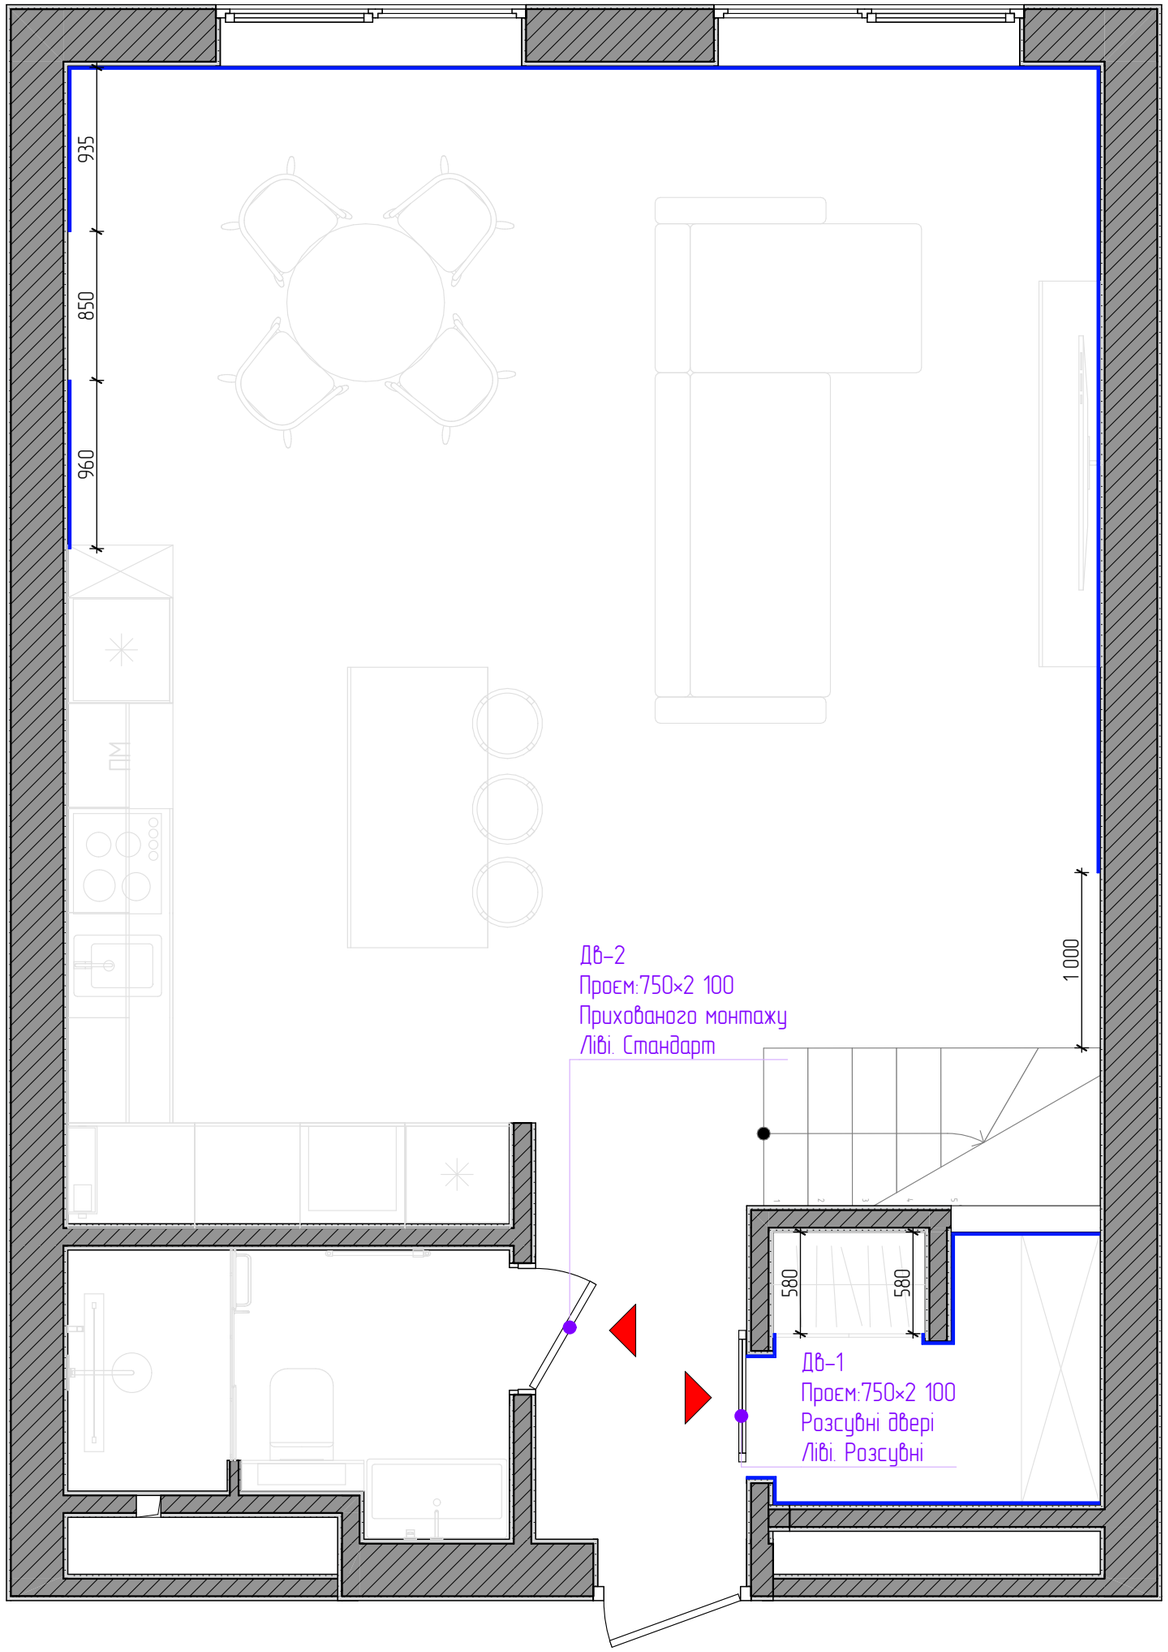


– лицева сторона дверей

Відомість плінтусів				
Поз.	Відображення на плані	Ескіз	Довжина, мм.	Примітки
1			43 032	

! Заміри дверних проємів провести відразу після формування дверного проєму та заливки стяжки представником виробника дверей. Відповідно надається супровідний лист від виробника дверей !

IHOR SAYEVICH interior designer	м. Львів, вул. Трускавецька ЖК Парус Smart	Розділ	Аркуш	Аркушів
	План відкривання дверей та влаштування плінтусів. Поверх 1	РП-ТК	38	55
	Ihor Sayevich Designer @ihor_sayevich_designer +380 97 585 91 01			

План відкривання дверей та влаштування плінтусів. Поверх 2











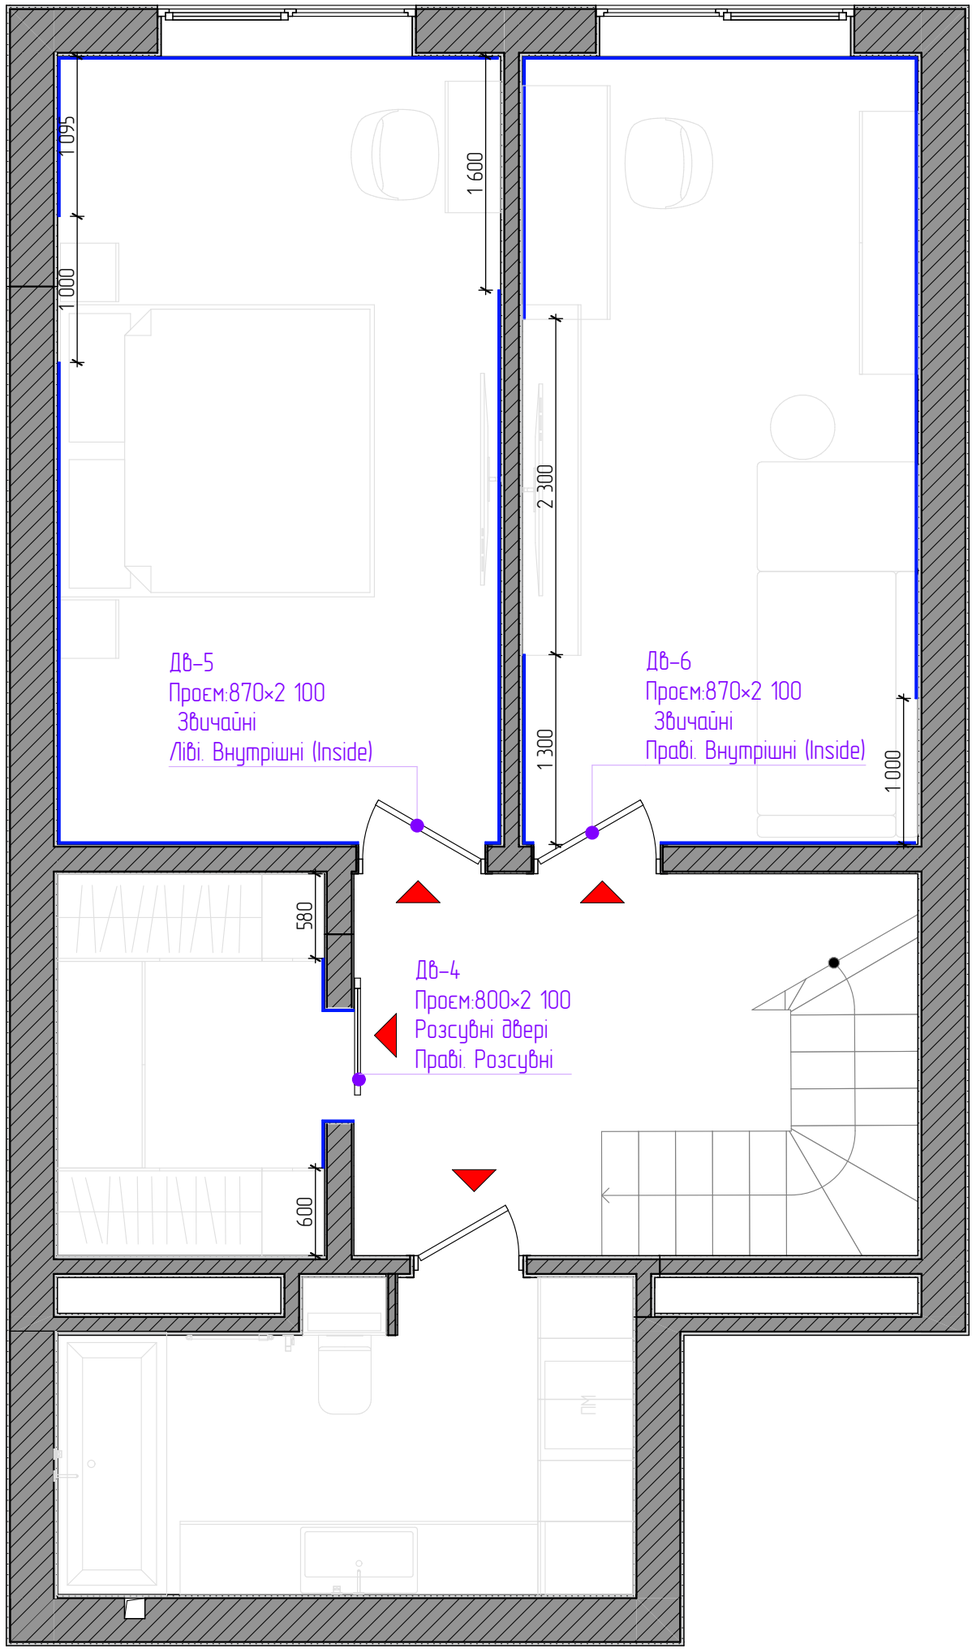


– лицева сторона дверей

Відомість плінтусів				
Поз.	Відображення на плані	Ескіз	Довжина, мм.	Примітки
1			43 032	

! Заміри дверних проємів провести відразу після формування дверного проєму та заливки стяжки представником виробника дверей. Відповідно надається супровідний лист від виробника дверей !

iSD IHOR SAYEVICH interior designer	м. Львів, вул. Трускавецька ЖК Парус Smart	Розділ	Аркуш	Аркушів
	План відкривання дверей та влаштування плінтусів. Поверх 1	РП-ТК	39	55
	Ihor Sayevich Designer @ihor_sayevich_designer +380 97 585 91 01			

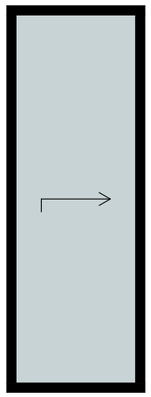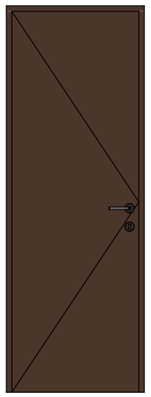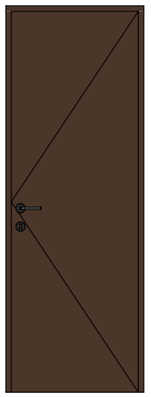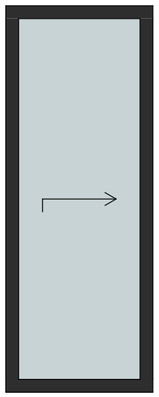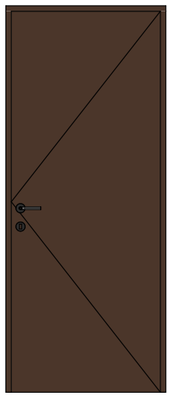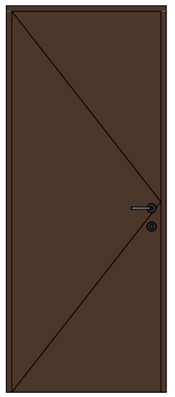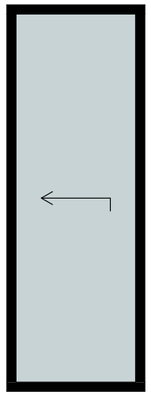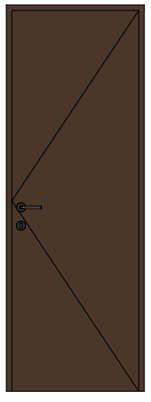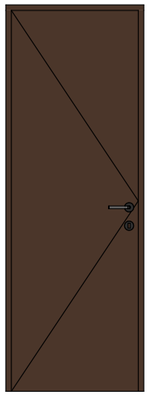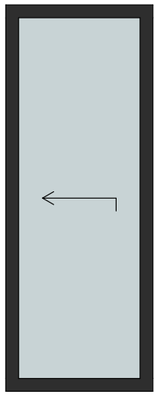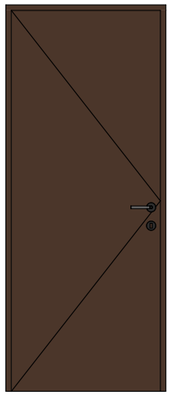Відомість дверей						
Марка дверей	Дв-1	Дв-2	Дв-3	Дв-4	Дв-5	Дв-6
К-сть	1	1	1	1	1	1
Розмір проєму	750×2 100	750×2 100	750×2 100	800×2 100	870×2 100	870×2 100
Вигляд з лицьової сторони						
Вигляд з тильної сторони						
Відкривання	Розсувні	Стандарт	Стандарт	Розсувні	Внутрішні (Inside)	Внутрішні (Inside)
Колір						


Відомість плінтусів				
Поз.	Відображення на плані	Ескіз	Довжина, мм.	Примітки
1			43 032	

Колір покриття підібрати відповідно до ДСП плити.

Матеріал та вигляд рами у розсувних дверях, а також систему відкривання обирає замовник!

IHOR SAYEVICH interior designer	м. Львів, вул. Трускавецька ЖК Парус Smart	Розділ	Аркуш	Аркушів
	Відомість дверних полотен	РП-ТК	40	55
	Ihor Sayevich Designer	@ihor_sayevich_designer	+380 97 585 91 01	

План розташування розгорток
M1:35

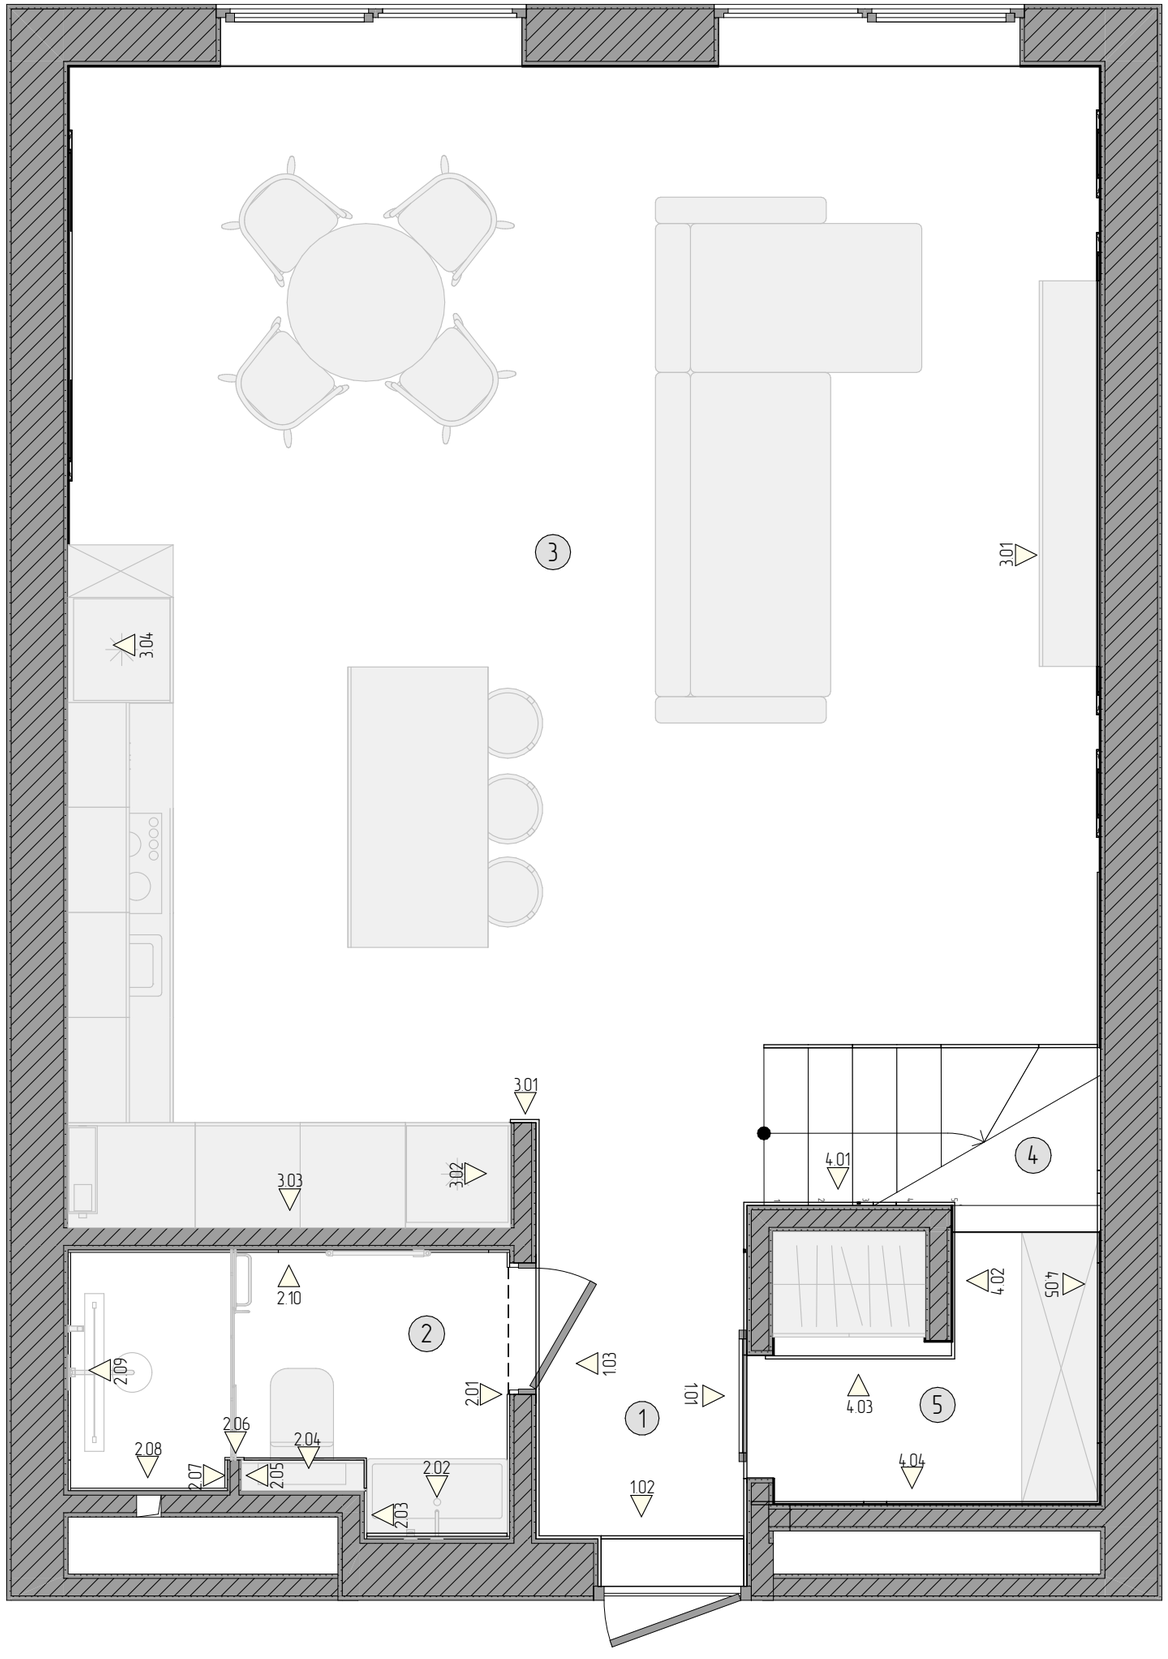

Площа матеріалів для оздоблення стін				
№	Матеріал	Найменування оздоблення	Площа, м. кв	Примітки
	Фарба	NCS S 1002-Y50R	124,95	Основне покриття. Може бути замінене на декоративну штукатурку в тому ж кольорі
	Фарба	Технічна	15,03	У кладовій
	Фарба	Технічна	16,75	За вбудованими шафами
	HPL плита		1,90	Зашиття інсталяцій у ванних кімнатах
	ДСП панель	Egger F206 ST9 Камінь П'єтра Гріджія чорний	1,96	Чорні декоративні вставки на стінах
	ДСП панель	SAVIOLA Valiant/Valiant P68 Горіх шоколадний	59,45	Основна стінова панель
	Керамограніт	Almera Ceramica (Spain) Ec.Candy Blanco 120x60	12,95	Акцентна (світла) плитка у ванних кімнатах
	Керамограніт	Almera Ceramica-2 Paula Black 60x120	34,23	Основна (темна) плитка у ванних кімнатах


Примітки:

Розміри вказані для прорахунку основних будівельних та оздоблювальних матеріалів.
Перед початком роботи і закупівлею матеріалів розміри перевірити на об'єкті!

У проекті вказана пропозиція! Всі оздоблювальні матеріали затверджує замовник!

iSD IHOR SAYEVICH interior designer	м. Львів, вул. Трускавецька ЖК Парус Smart	Розділ	Аркуш	Аркушів
	План розташування розгорток. Поверх 1	РП-ТК	41	55
	Ihor Sayevich Designer @ihor_sayevich_designer +380 97 585 91 01			

План розташування розгорток. Поверх 2

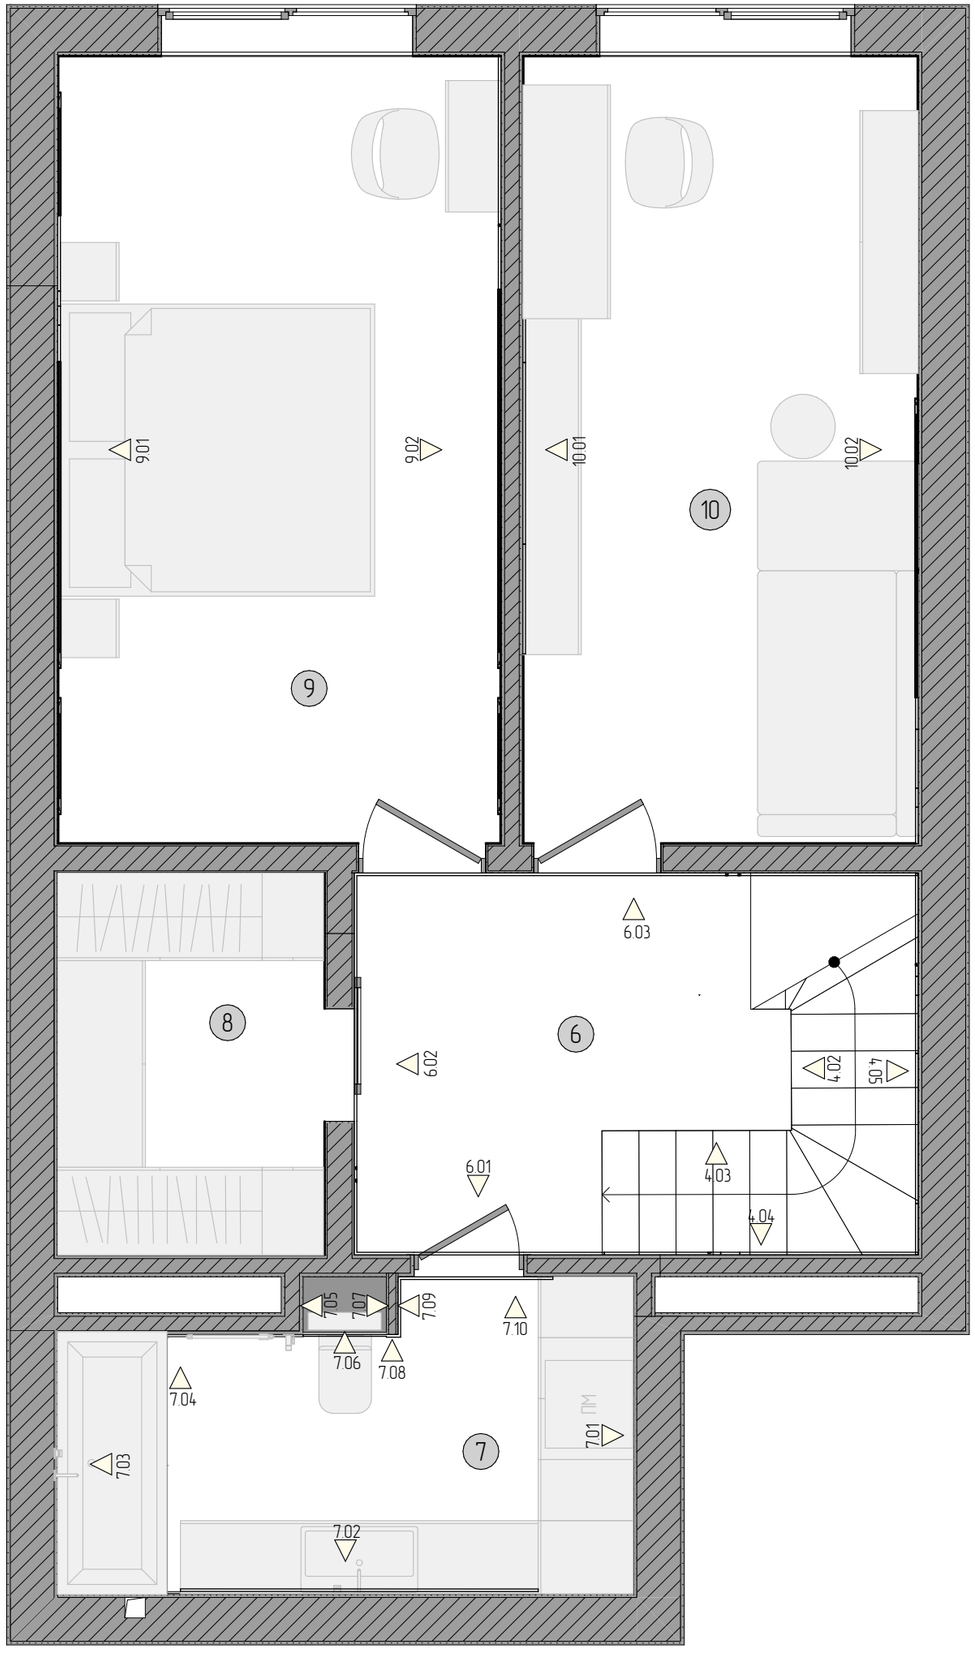

Площа матеріалів для оздоблення стін				
№	Матеріал	Найменування оздоблення	Площа, м. кв	Примітки
	Фарба	NCS S 1002-Y50R	124,95	Основне покриття. Може бути замінене на декоративну штукатурку в тому ж кольорі
	Фарба	Технічна	15,03	У кладовій
	Фарба	Технічна	16,75	За вбудованими шафами
	HPL плита		1,90	Зашиття інсталяцій у ванних кімнатах
	ДСП панель	Egger F206 ST9 Камінь П'єтра Гріджія чорний	1,96	Чорні декоративні вставки на стінах
	ДСП панель	SAVIOLA Valiant/Valiant P68 Горіх шоколадний	59,45	Основна стінова панель
	Керамограніт	Almera Ceramica (Spain) Ec.Candy Blanco 120x60	12,95	Акцентна (світла) плитка у ванних кімнатах
	Керамограніт	Almera Ceramica-2 Paula Black 60x120	34,23	Основна (темна) плитка у ванних кімнатах

Примітки:

Розміри вказані для прорахунку основних будівельних та оздоблювальних матеріалів.
Перед початком роботи і закупівлею матеріалів розміри перевірити на об'єкті!

У проекті вказана пропозиція! Всі оздоблювальні матеріали затверджує замовник!

iSD IHOR SAYEVICH interior designer	м. Львів, вул. Трускавецька ЖК Парус Smart	Розділ	Аркуш	Аркушів
	План розташування розгорток. Поверх 2	РП-ТК	42	55
	Ihor Sayevich Designer @ihor_sayevich_designer +380 97 585 91 01			

Розгортки приміщення 1 (передпокій)

1.01



1.02



1.03



У проекті вказана пропозиція! Всі оздоблювальні матеріали затверджує замовник!

Умовні позначення

– ДСП плити


IHOR SAYEVICH interior designer	м. Львів, вул. Трускавецька ЖК Парус Smart	Розділ	Аркуш	Аркушів
	Розгортки приміщення 1 (передпокій)	РП-ТК	43	55
	Ihor Sayevich Designer	@ihor_sayevich_designer	+380 97 585 91 01	

Розгортки приміщення 2 (ванна кімната, поверх 1)


2.01




2.02

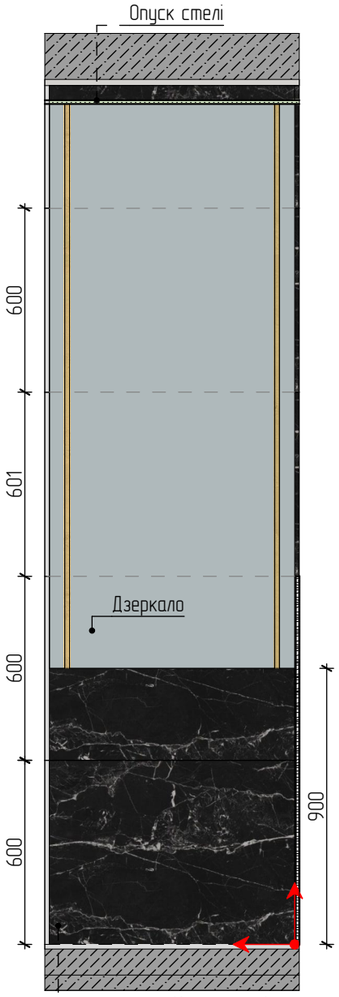


2.03

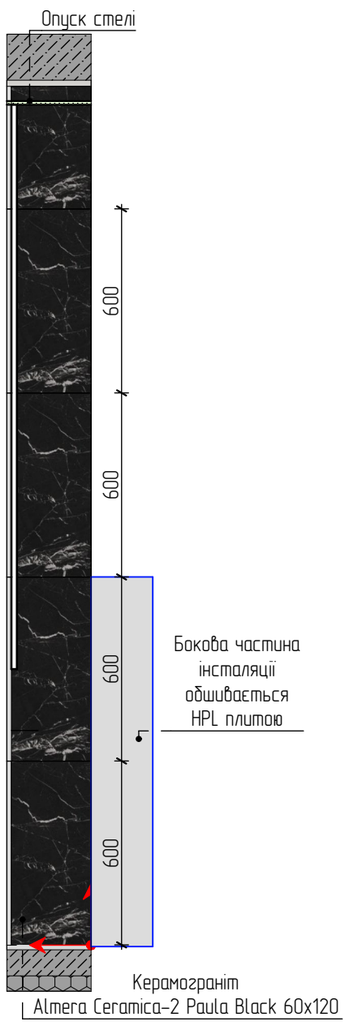


2.04

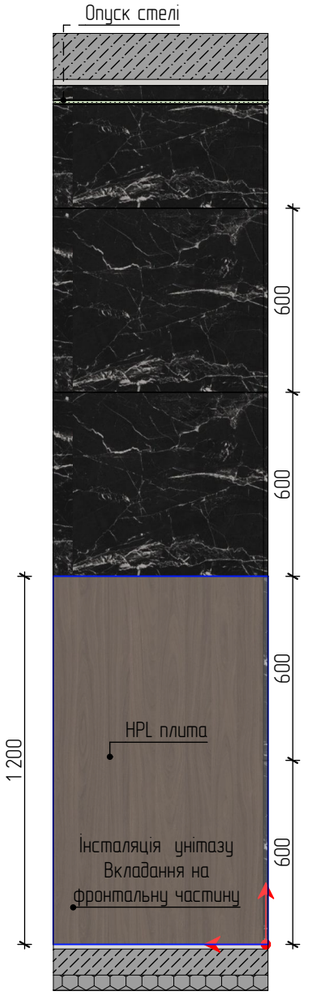

2.05

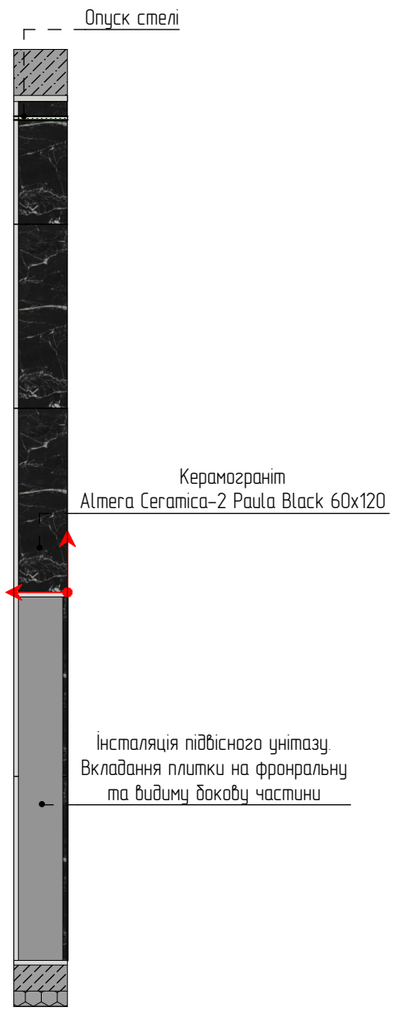


2.06

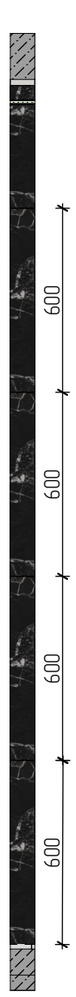

Умовні позначення



– керамограніт Almera Ceramica (Spain) Ec.Candy Blanco 120x60

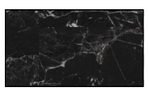

– керамограніт Almera Ceramica-2 Paula Black 60x120




– рекомендований початок та напрямок розкладки плитки

У проекті вказана пропозиція! Всі оздоблювальні матеріали затверджує замовник!


IHOR SAYEVICH interior designer	м. Львів, вул. Трускавецька ЖК Парус Smart	Розділ	Аркуш	Аркушів
	Розгортки приміщення 2 (ванна кімната)	РП-ТК	44	55
	Ihor Sayevich Designer	@ihor_sayevich_designer	+380 97 585 91 01	

Розгортки приміщення 2 (ванна кімната, поверх 1)


2.07

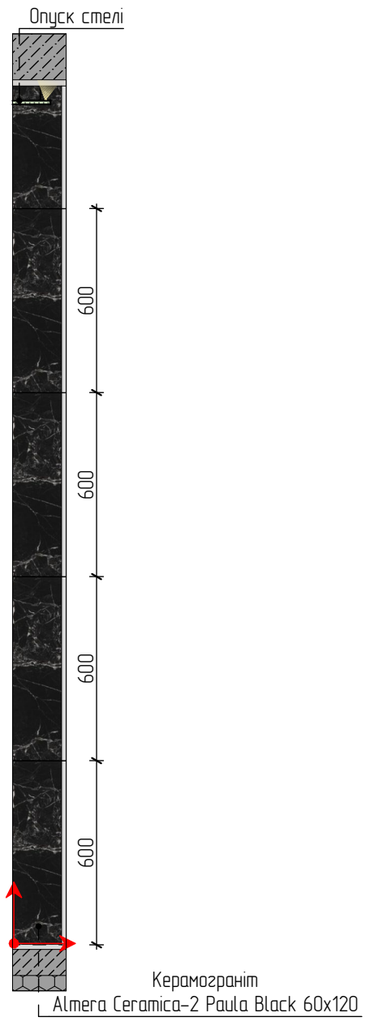

2.08

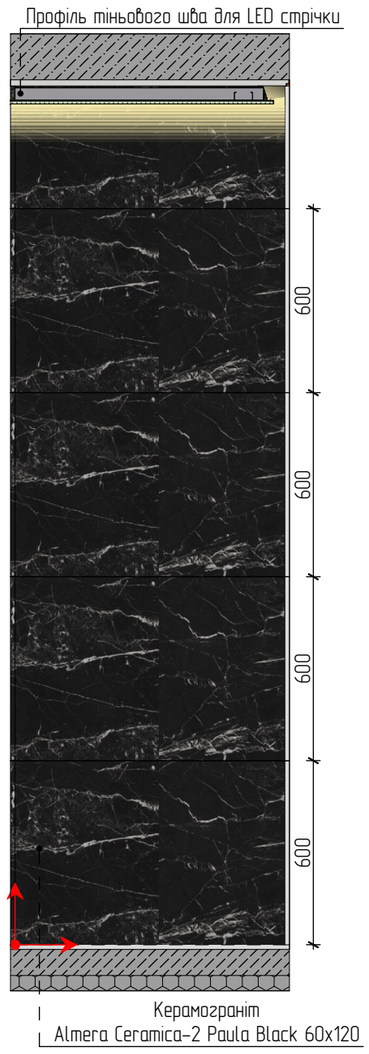

2.09

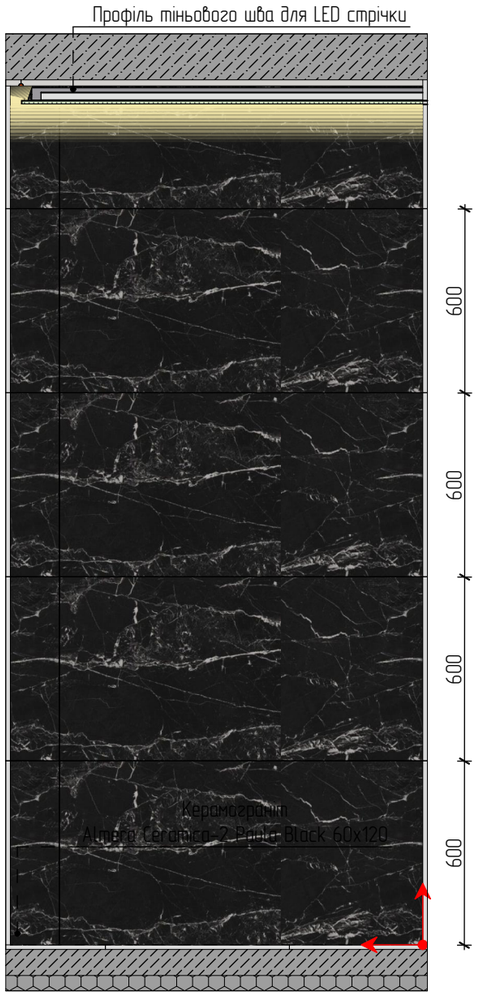


2.10



Умовні позначення



– керамограніт Almera Ceramica (Spain) Ec.Candy Blanco 120x60

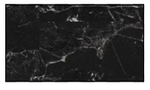

– керамограніт Almera Ceramica-2 Paula Black 60x120



– рекомендований початок та напрямок розкладки плитки

У проекті вказана пропозиція! Всі оздоблювальні матеріали затверджує замовник!


iSD IHOR SAYEVICH interior designer	м. Львів, вул. Трускавецька ЖК Парус Smart	Розділ	Аркуш	Аркушів
	Розгортки приміщення 2 (ванна кімната)	РП-ТК	45	55
	Ihor Sayevich Designer	@ihor_sayevich_designer	+380 97 585 91 01	

Розгортки приміщення 3 (кухня-вітальня)


3.01



3.02

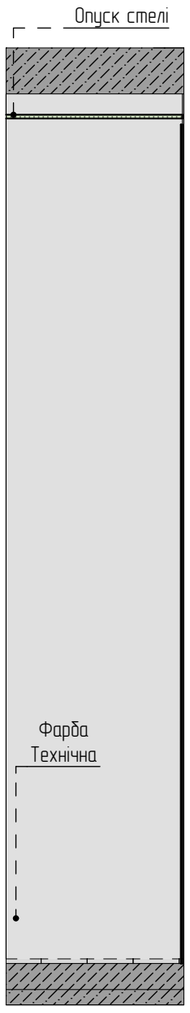

3.03

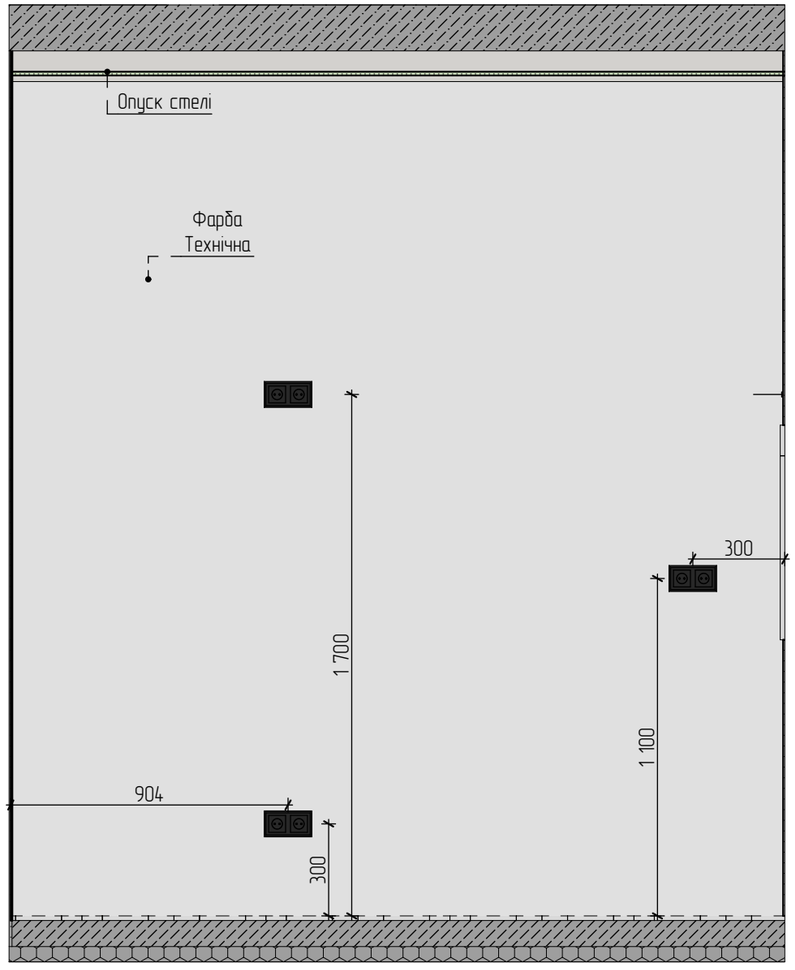

У проекті вказана пропозиція! Всі оздоблювальні матеріали затверджує замовник!


Умовні позначення

– ДСП плити


iSD IHOR SAYEVICH interior designer	м. Львів, вул. Трускавецька ЖК Парус Smart	Розділ	Аркуш	Аркушів
	Розгортки приміщення 3 (кухня-вітальня)	РП-ТК	46	55
	Ihor Sayevich Designer @ihor_sayevich_designer +380 97 585 91 01			

Розгортки приміщення 3 (кухня-вітальня)

3.04

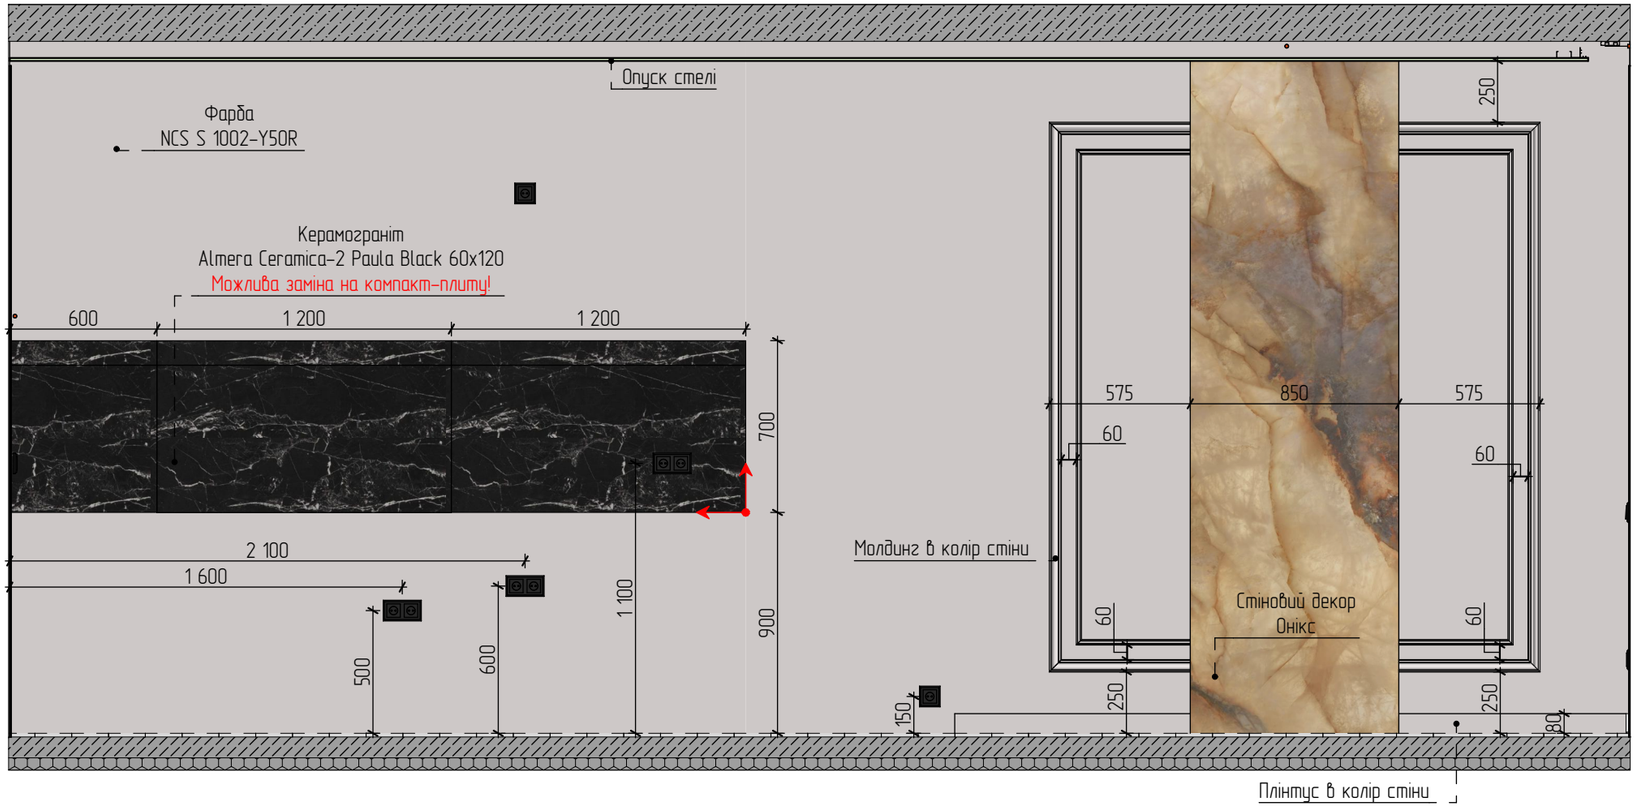

3.05

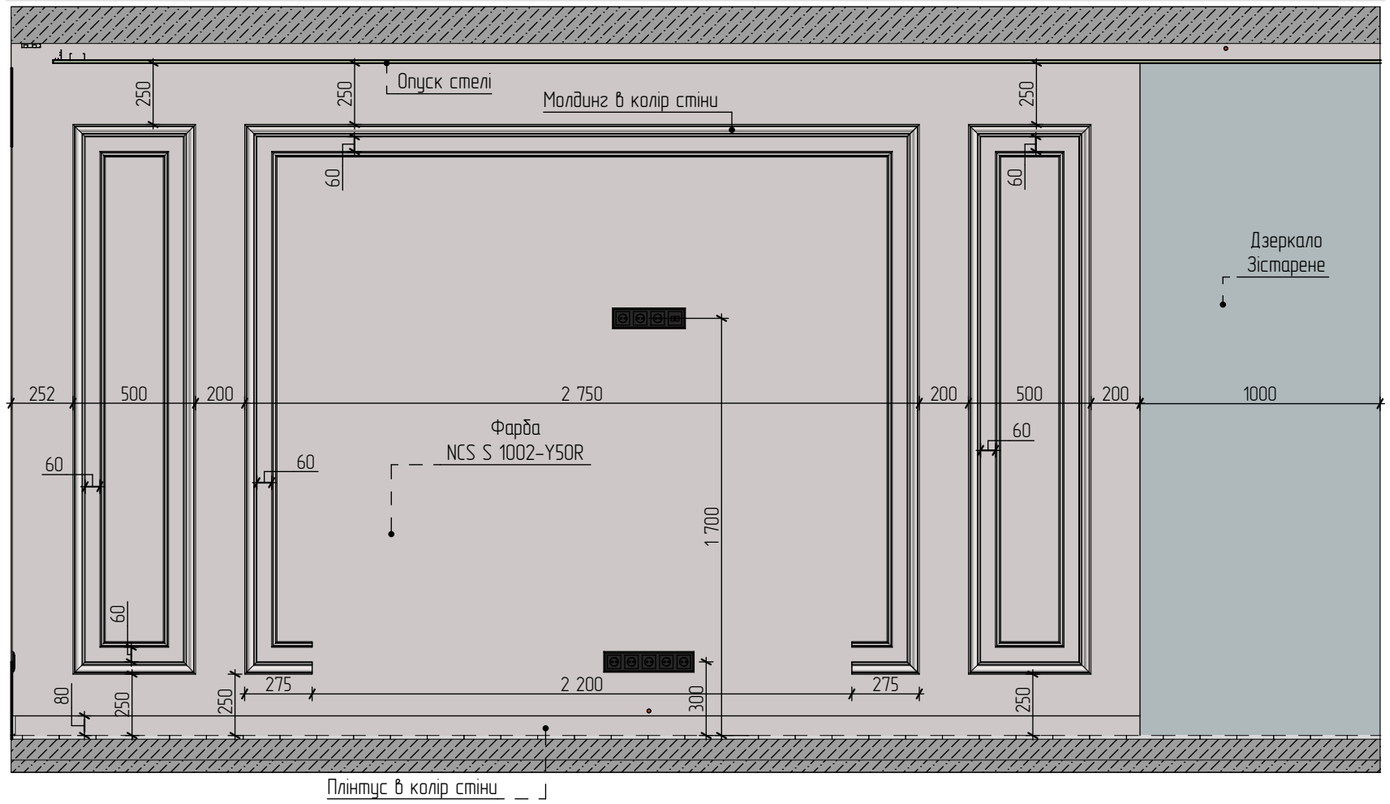

Умовні позначення

- керамогранiт Almera Ceramica (Spain) Ec.Candy Blanco 120x60
- керамогранiт Almera Ceramica-2 Paula Black 60x120
- рекомендований початок та напрямок розкладки плитки

У проекті вказана пропозиція! Всі оздоблювальні матеріали затверджує замовник!

IHOR SAYEVICH interior designer	м. Львів, вул. Трускавецька ЖК Парус Smart	Розділ	Аркуш	Аркушів
	Розгортки приміщення 3 (кухня-вітальня)	РП-ТК	47	55
	Ihor Sayevich Designer	@ihor_sayevich_designer	+380 97 585 91 01	

Розгортки приміщення 4 (сходова частина)


4.01



4.02



4.03

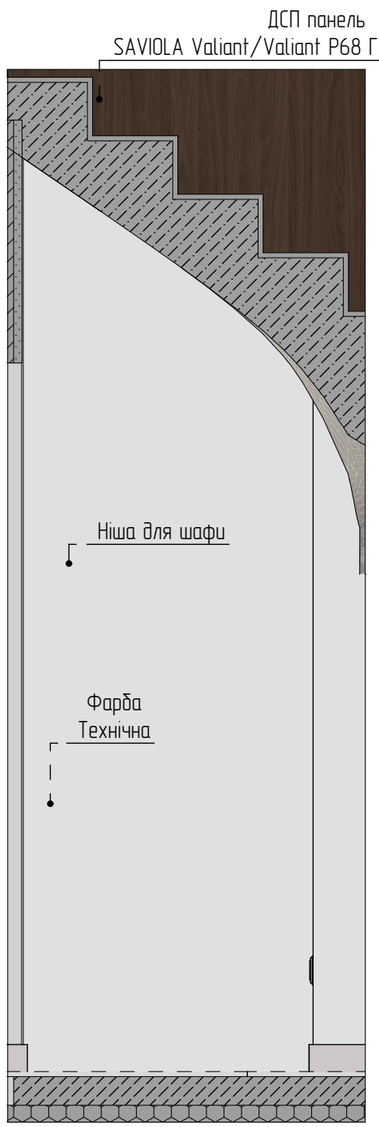

У проекті вказана пропозиція! Всі оздоблювальні матеріали затверджує замовник!


Умовні позначення

– ДСП плити


iSD IHOR SAYEVICH interior designer	м. Львів, вул. Трускавецька ЖК Парус Smart	Розділ	Аркуш	Аркушів
	Розгортки приміщення 4 (сходова частина)	РП-ТК	48	55
	Ihor Sayevich Designer @ihor_sayevich_designer +380 97 585 91 01			

Розгортки приміщення 4 (сходова частина)


5.01

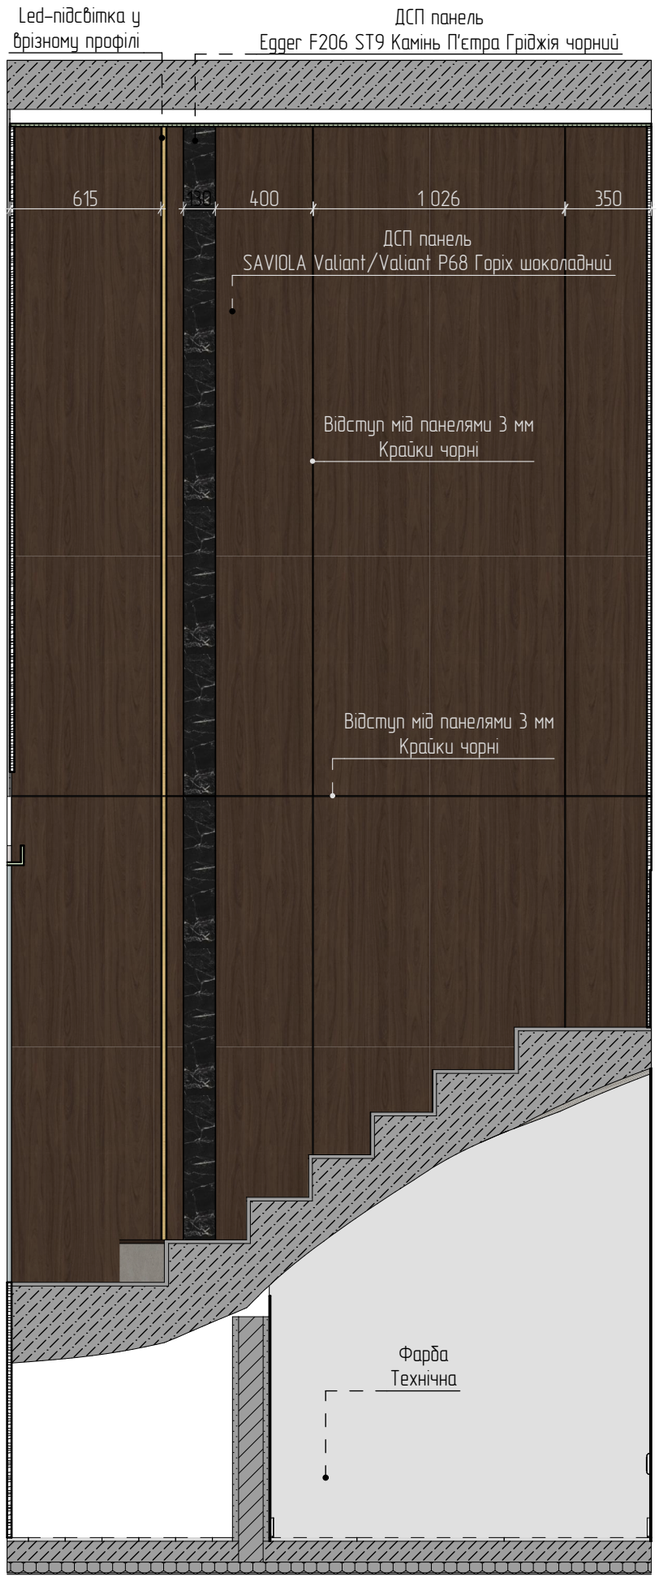

4.02

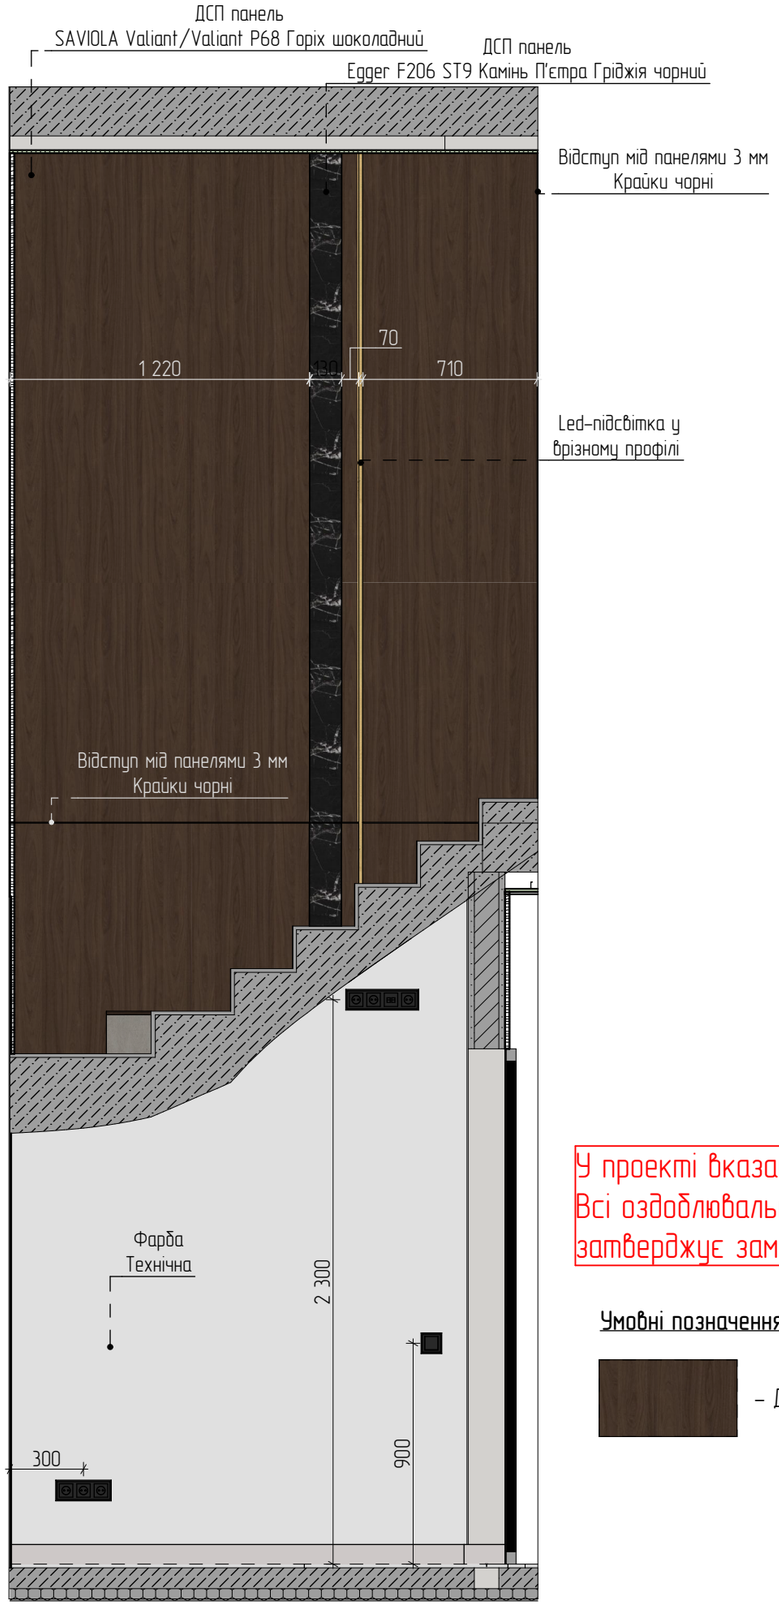

Сходова (варіант оздоблення декоративною штукатуркою)

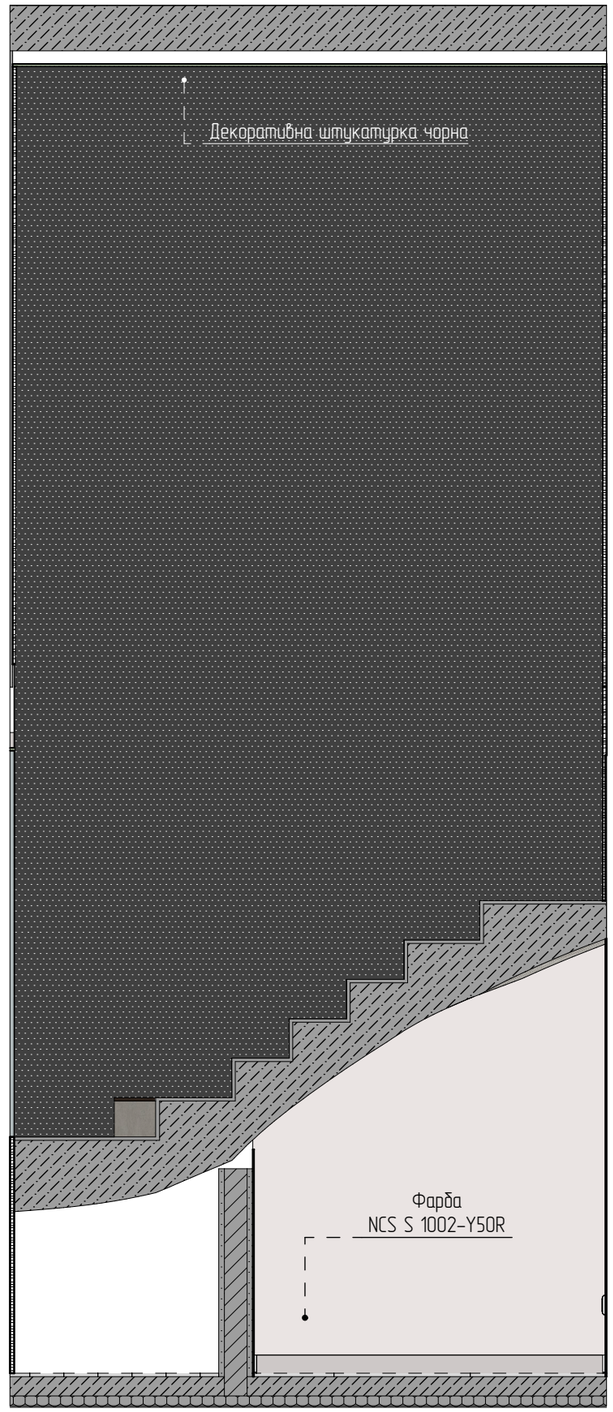

У проекті вказана пропозиція!
Всі оздоблювальні матеріали затверджує замовник!


Умовні позначення

– ДСП плити


iSD IHOR SAYEVICH interior designer	м. Львів, вул. Трускавецька ЖК Парус Smart	Розділ	Аркуш	Аркушів
	Розгортки приміщення 4 (сходова частина)	РП-ТК	49	55
	Ihor Sayevich Designer @ihor_sayevich_designer +380 97 585 91 01			

Розгортки приміщення 6 (коридор, 2 поверх)


6.01

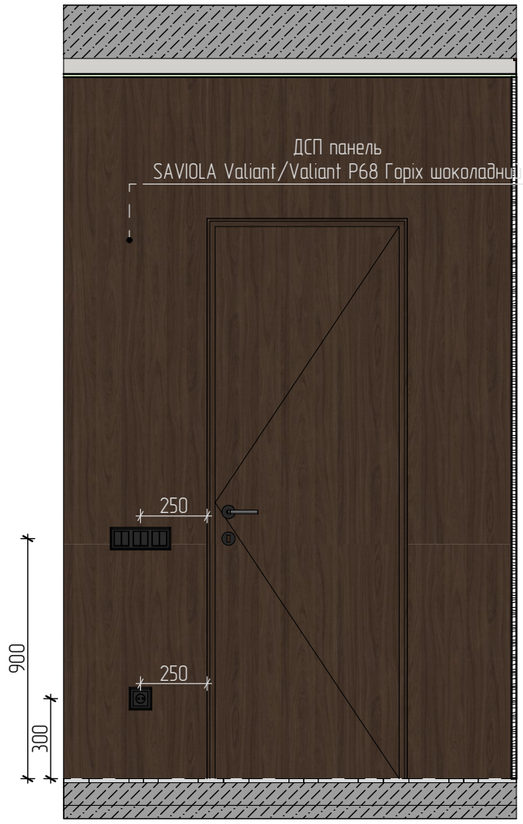

6.02

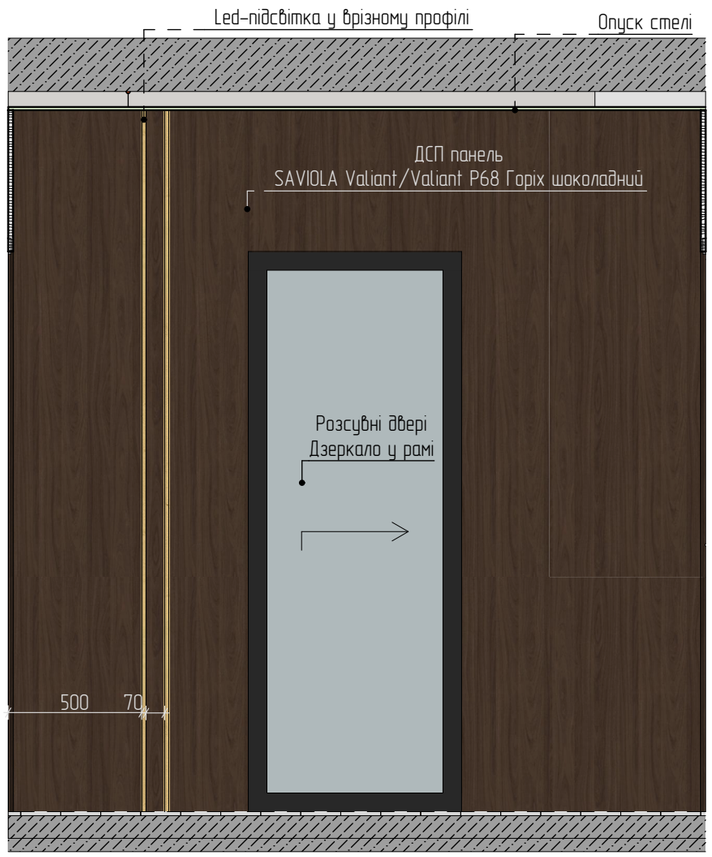

6.03

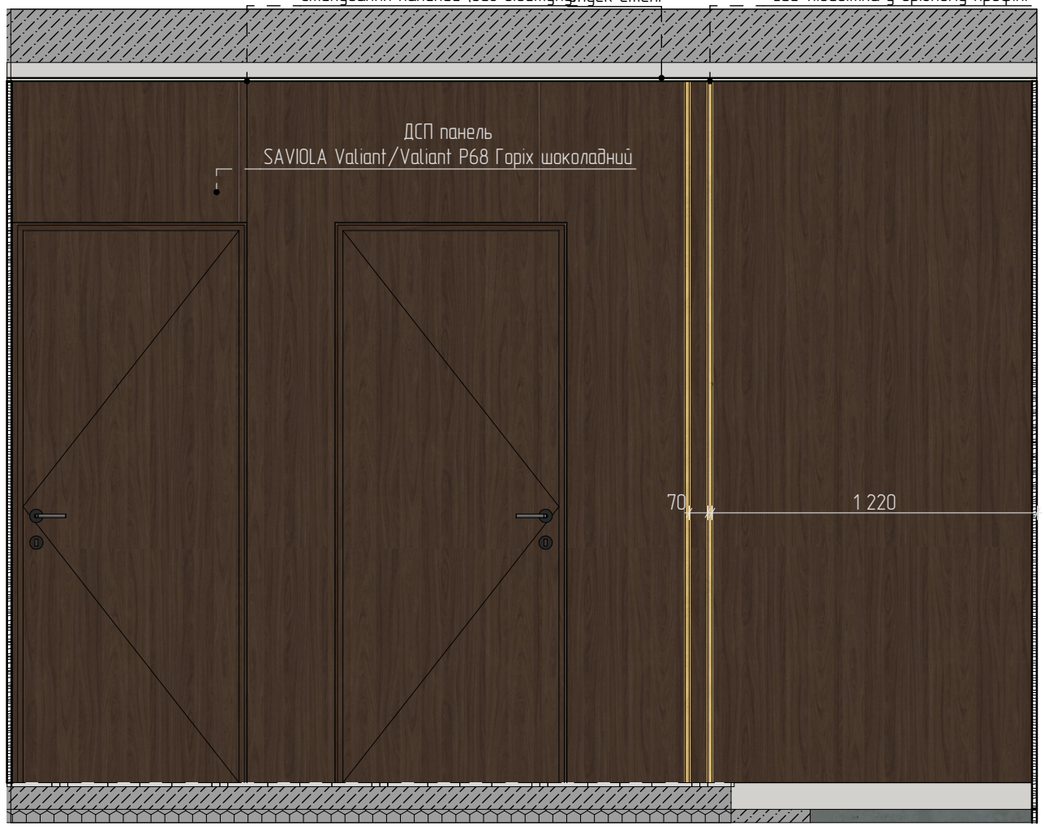

У проекті вказана пропозиція! Всі оздоблювальні матеріали затверджує замовник!


Умовні позначення

– ДСП плити


IHOR SAYEVICH interior designer	м. Львів, вул. Трускавецька ЖК Парус Smart	Розділ	Аркуш	Аркушів
	Розгортки приміщення 6 (коридор, 2 поверх)	РП-ТК	50	55
	Ihor Sayevich Designer	@ihor_sayevich_designer	+380 97 585 91 01	

Розгортки приміщення 7 (ванна кімната, 2 поверх)

7.01

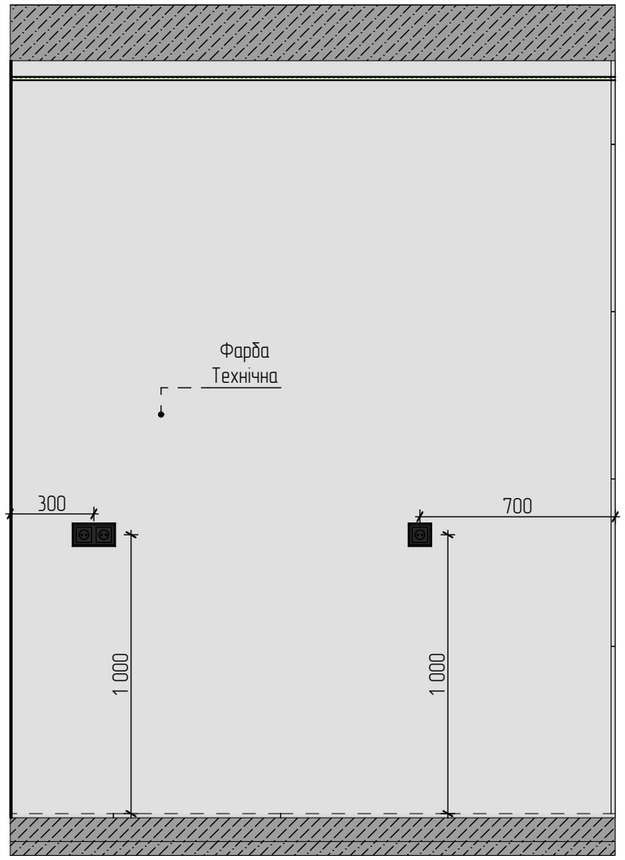


7.02

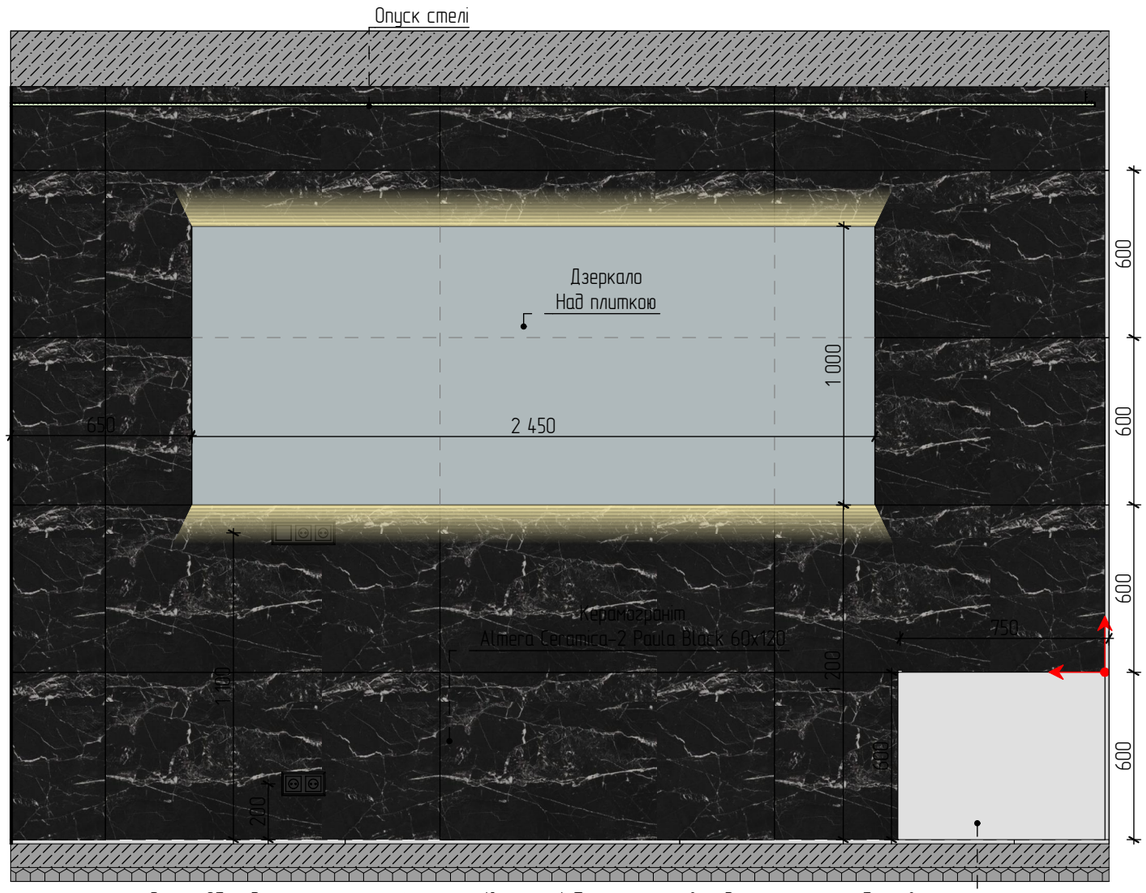

Ванна. Облицювання плиткою на фронтальній стороні. По периметру вкладання плитки на борт ванни

7.03

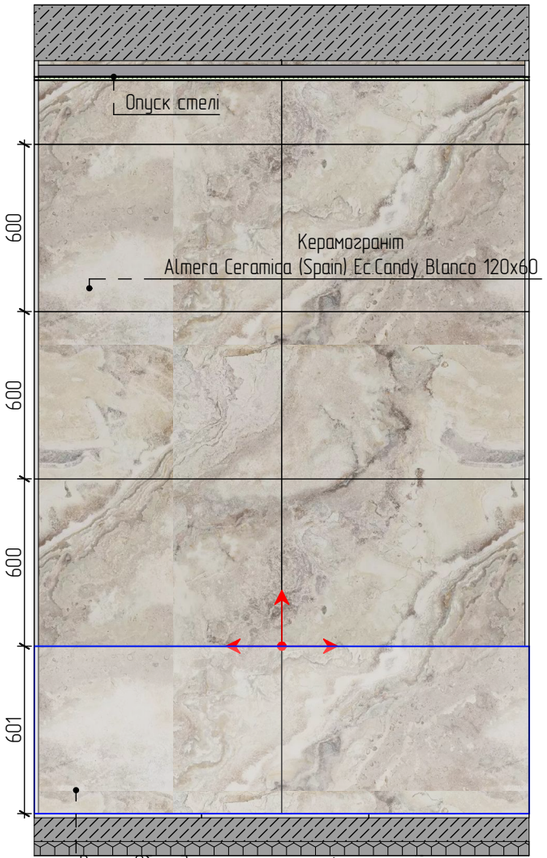


Ванна. Облицювання плиткою на фронтальній стороні. По периметру вкладання плитки на борт ванни

Умовні позначення



– керамограніт Almera Ceramica (Spain) Ec.Candy Blanco 120x60

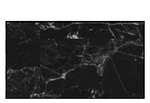

– керамограніт Almera Ceramica-2 Paula Black 60x120




– рекомендований початок та напрямок розкладки плитки

У проекті вказана пропозиція! Всі оздоблювальні матеріали затверджує замовник!

IHOR SAYEVICH interior designer	м. Львів, вул. Трускавецька ЖК Парус Smart	Розділ	Аркуш	Аркушів
	Розгортки приміщення 7 (ванна кімната, 2 поверх)	РП-ТК	51	55
	Ihor Sayevich Designer	@ihor_sayevich_designer	+380 97 585 91 01	


Розгортки приміщення 7 (ванна кімната, 2 поверх)

7.04

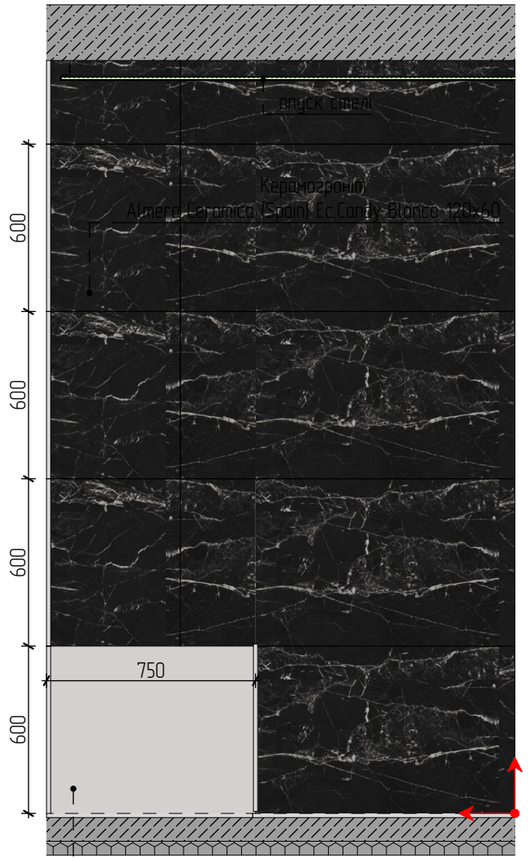


Ванна. Облицювання плиткою на фронтальній стороні.
По периметру вкладання плитки на борт ванни


7.05

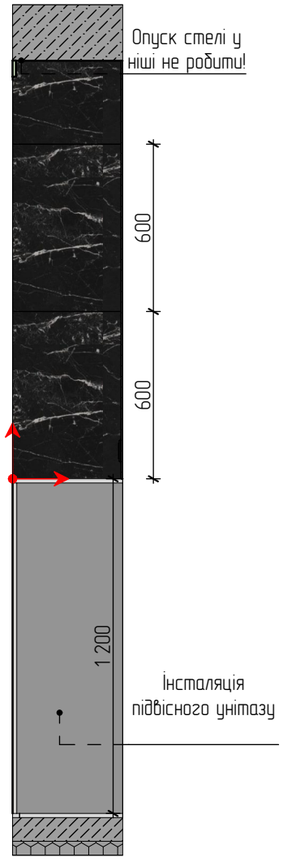


7.06

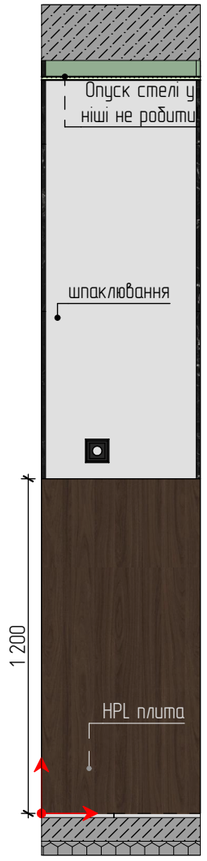

7.07

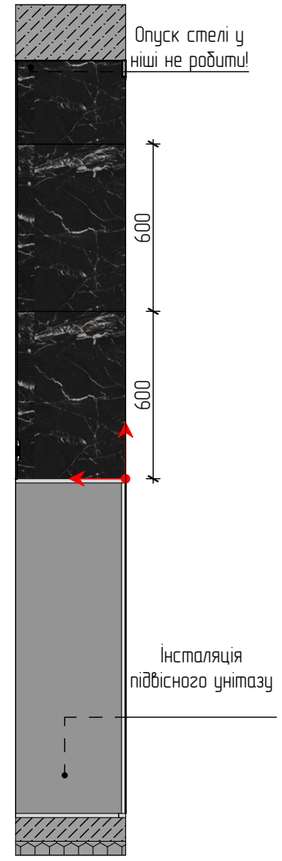

7.08

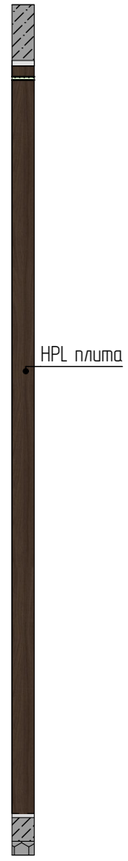

7.09



7.10



Умовні позначення

- керамограніт Almera Ceramica (Spain) Ec.Candy Blanco 120x60
- керамограніт Almera Ceramica-2 Paula Black 60x120
- рекомендований початок та напрямок розкладки плитки

Умовні позначення


- ДСП плити

У проекті вказана пропозиція! Всі оздоблювальні матеріали затверджує замовник!


IHOR SAYEVICH interior designer	м. Львів, вул. Трускавецька ЖК Парус Smart	Розділ	Аркуш	Аркушів
	Розгортки приміщення 7 (ванна кімната, 2 поверх)	РП-ТК	52	55
	Ihor Sayevich Designer @ihor_sayevich_designer +380 97 585 91 01			

Розгортки приміщення 9 (спальня)

9.01

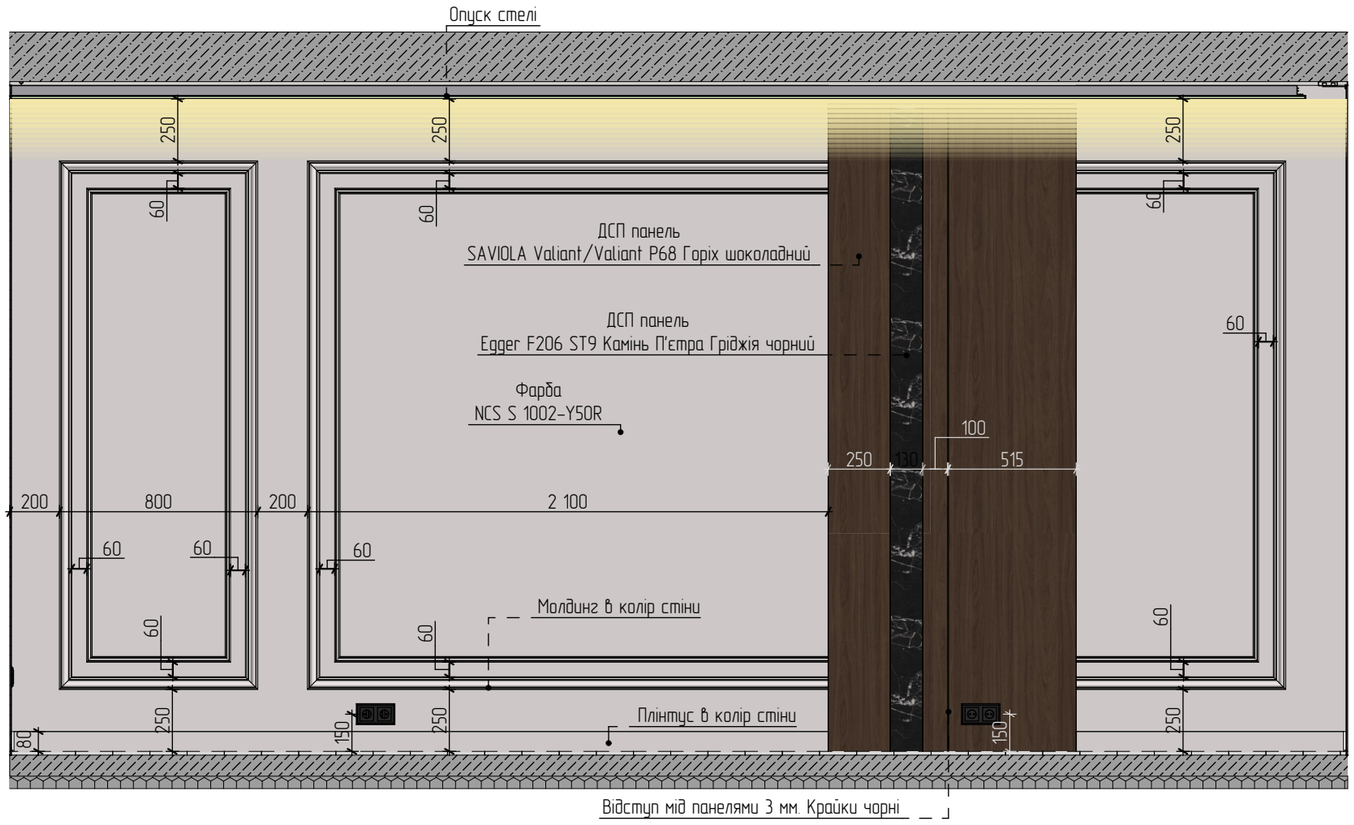

9.02

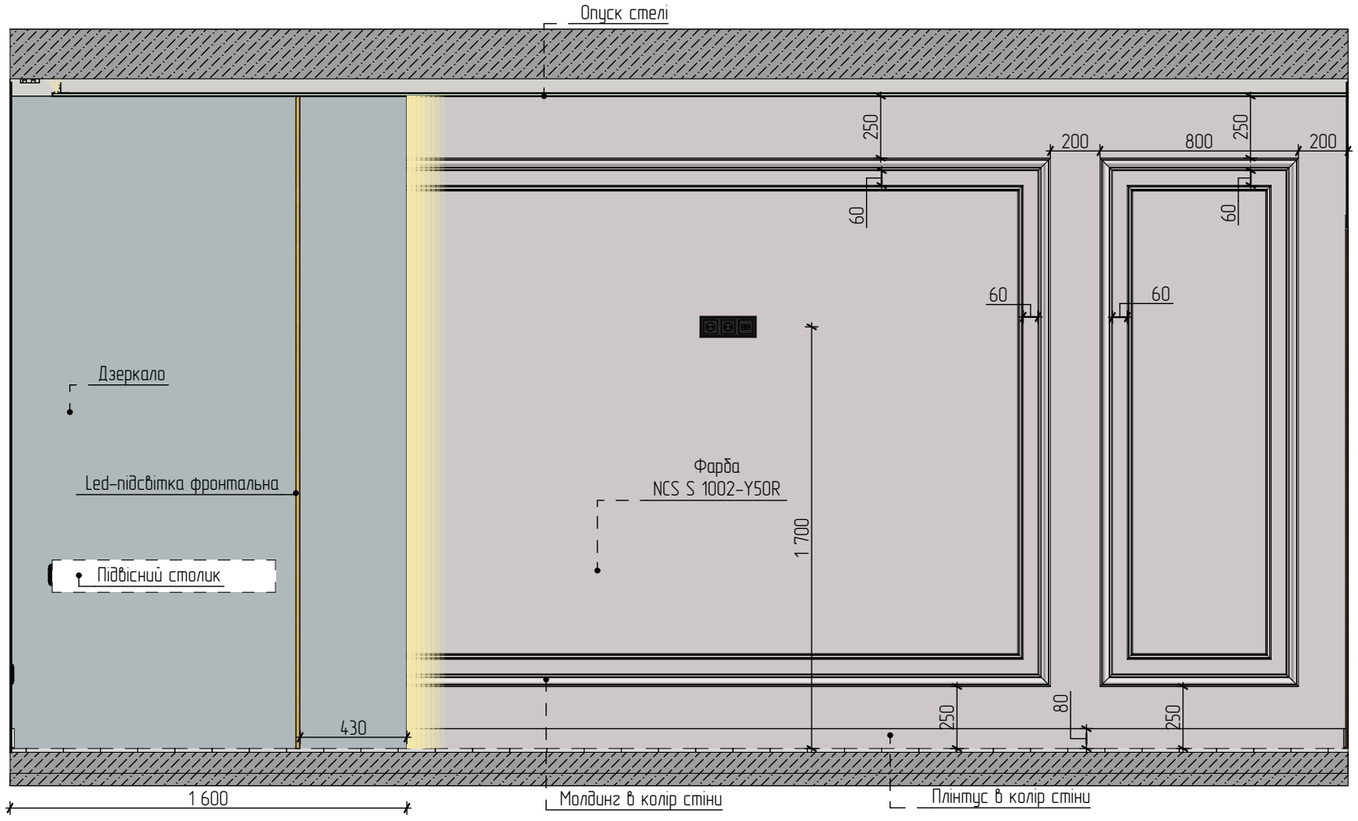

Умовні позначення


– ДСП плити

У проекті вказана пропозиція! Всі оздоблювальні матеріали затверджує замовник!


IHOR SAYEVICH interior designer	м. Львів, вул. Трускавецька ЖК Парус Smart	Розділ	Аркуш	Аркушів
	Розгортки приміщення 9 (спальня)	РП-ТК	53	55
	Ihor Sayevich Designer @ihor_sayevich_designer +380 97 585 91 01			

Розгортки приміщення 10 (кабінет)

10.01

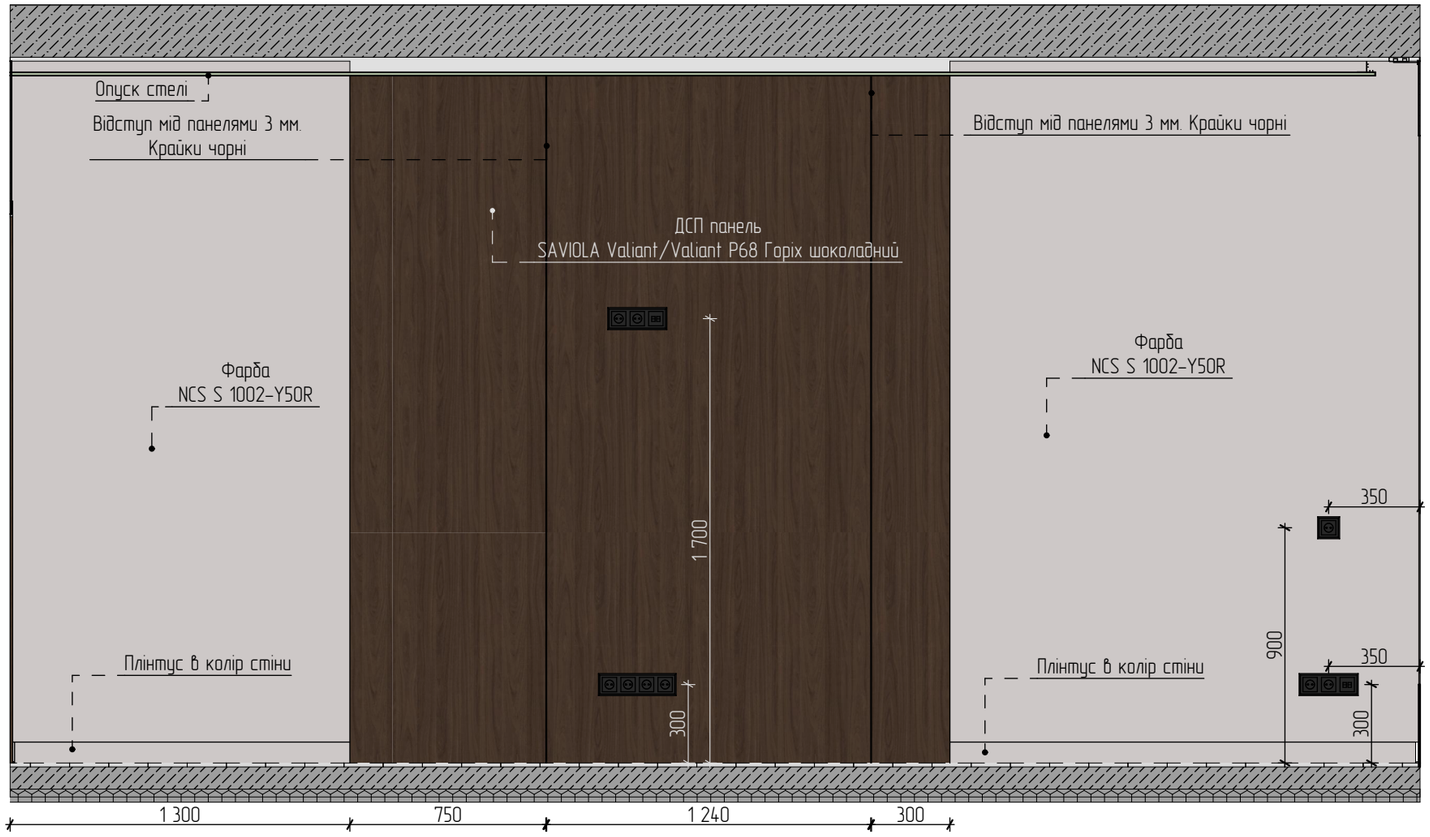

10.02

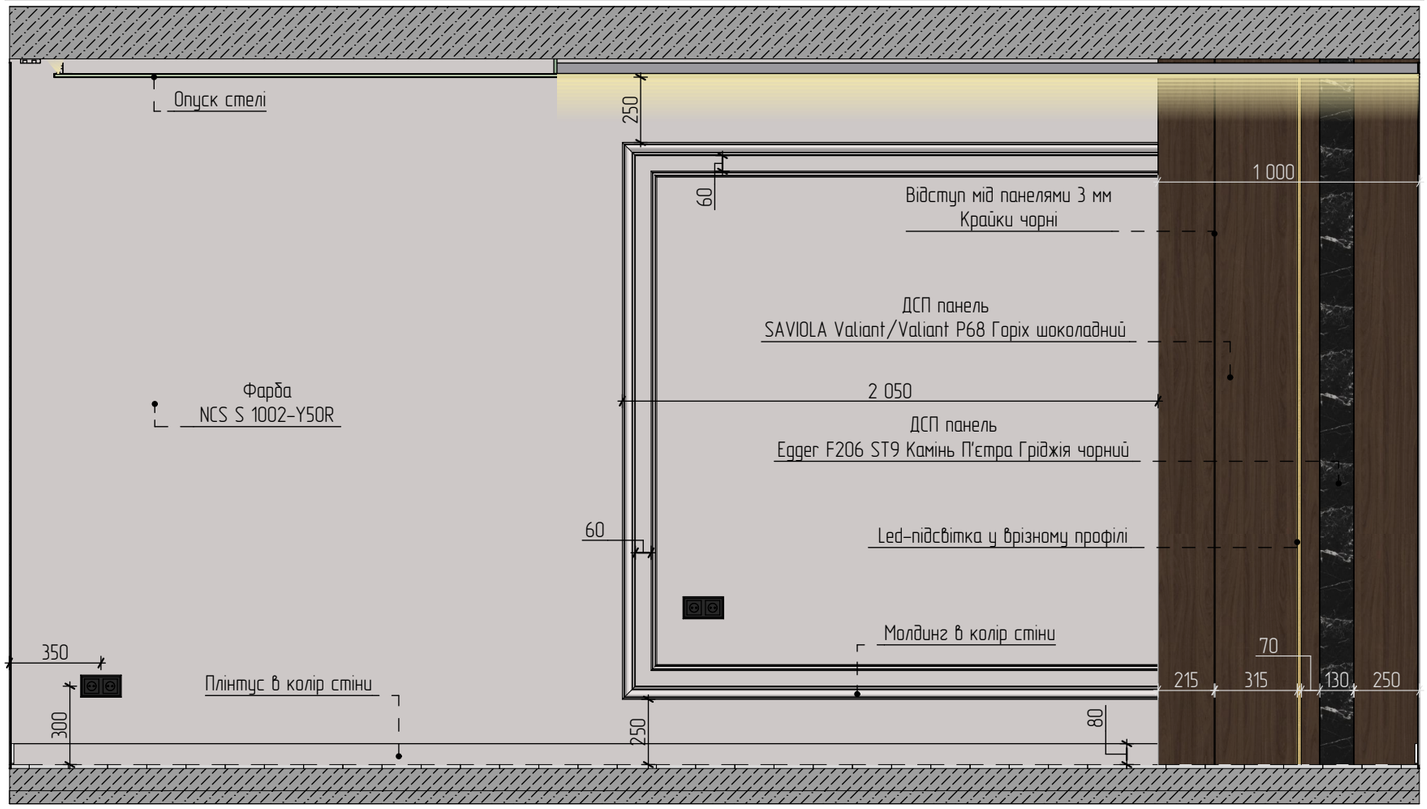

Умовні позначення

– ДСП плити

У проекті вказана пропозиція! Всі оздоблювальні матеріали затверджує замовник!

IHOR SAYEVICH interior designer	м. Львів, вул. Трускавецька ЖК Парус Smart	Розділ	Аркуш	Аркушів
	Розгортки приміщення 10 (кабінет)	РП-ТК	54	55
	Ihor Sayevich Designer @ihor_sayevich_designer +380 97 585 91 01			